



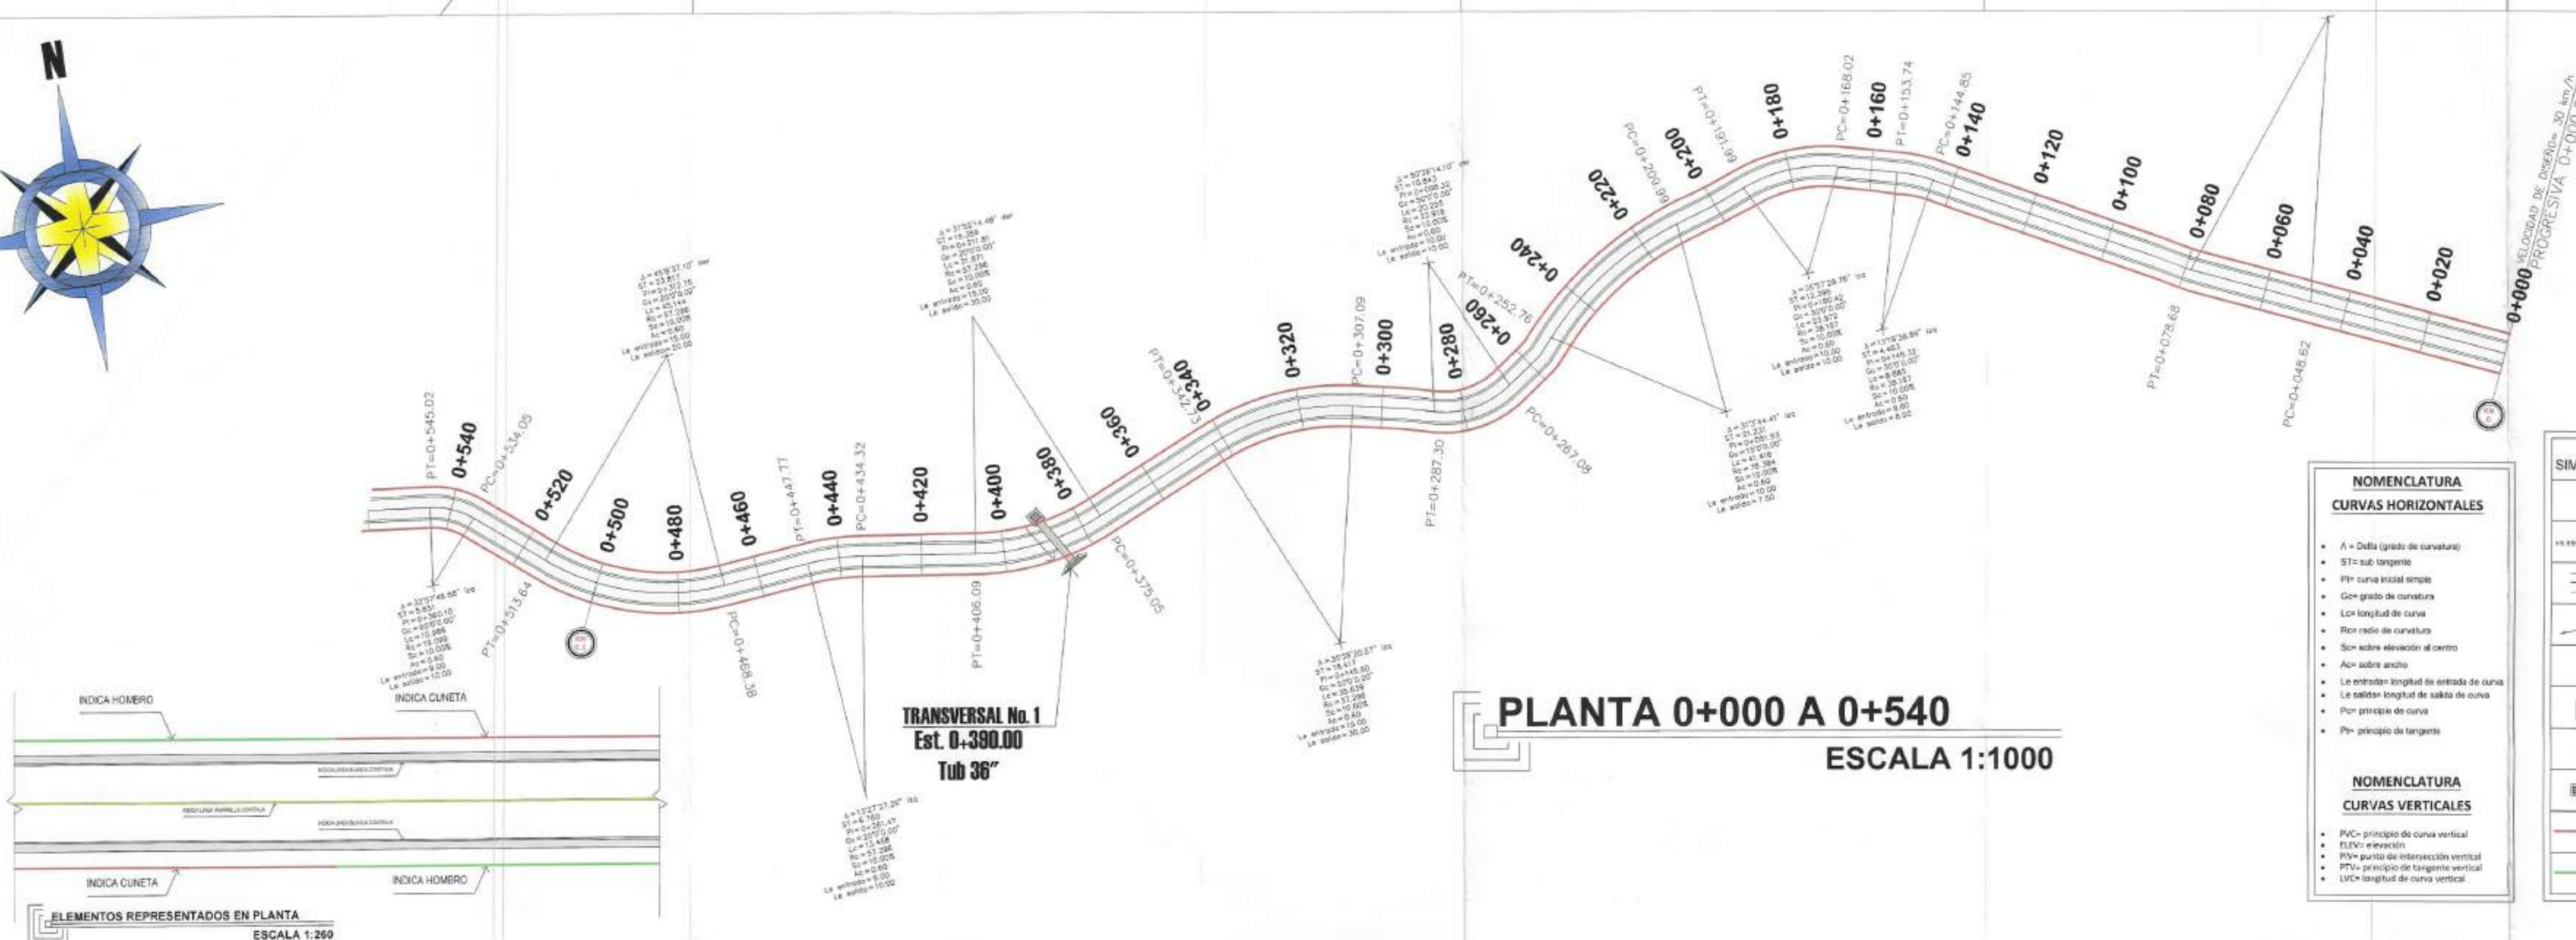

PLANTA 0+000 A 0+540
ESCALA 1:1000

- NOMENCLATURA CURVAS HORIZONTALES**
- A = Delta (grados de curvatura)
 - ST = sub tangente
 - PI = curva inicial simple
 - G = grado de curvatura
 - L = longitud de curva
 - R = radio de curvatura
 - S = sobre elevación al centro
 - A = sobre ancho
 - Le = entrada longitud de entrada de curva
 - Ls = salida longitud de salida de curva
 - Pm = principio de curva
 - Pt = principio de tangente
- NOMENCLATURA CURVAS VERTICALES**
- PVC = principio de curva vertical
 - ELV = elevación
 - PIV = punto de intersección vertical
 - PTV = principio de tangente vertical
 - LVC = longitud de curva vertical

SIMBOLOGIA	DESCRIPCIÓN
0+000.00	Estacionamiento
+5.556 % en 164.05m	Pendiente en perfil
INDICA CUNETA	Caminamiento en planta
INDICA HOMBRO	Curva Horizontal
PC	Curva Vertical
PT	PRINCIPIO DE CURVA HORIZONTAL
	PRINCIPIO DE TANGENTE HORIZONTAL
INDICA CUNETA EN PLANTA	tubería en planta, Caja cabezal en entrada y muro cabezal en salida
INDICA HOMBRO EN PLANTA	

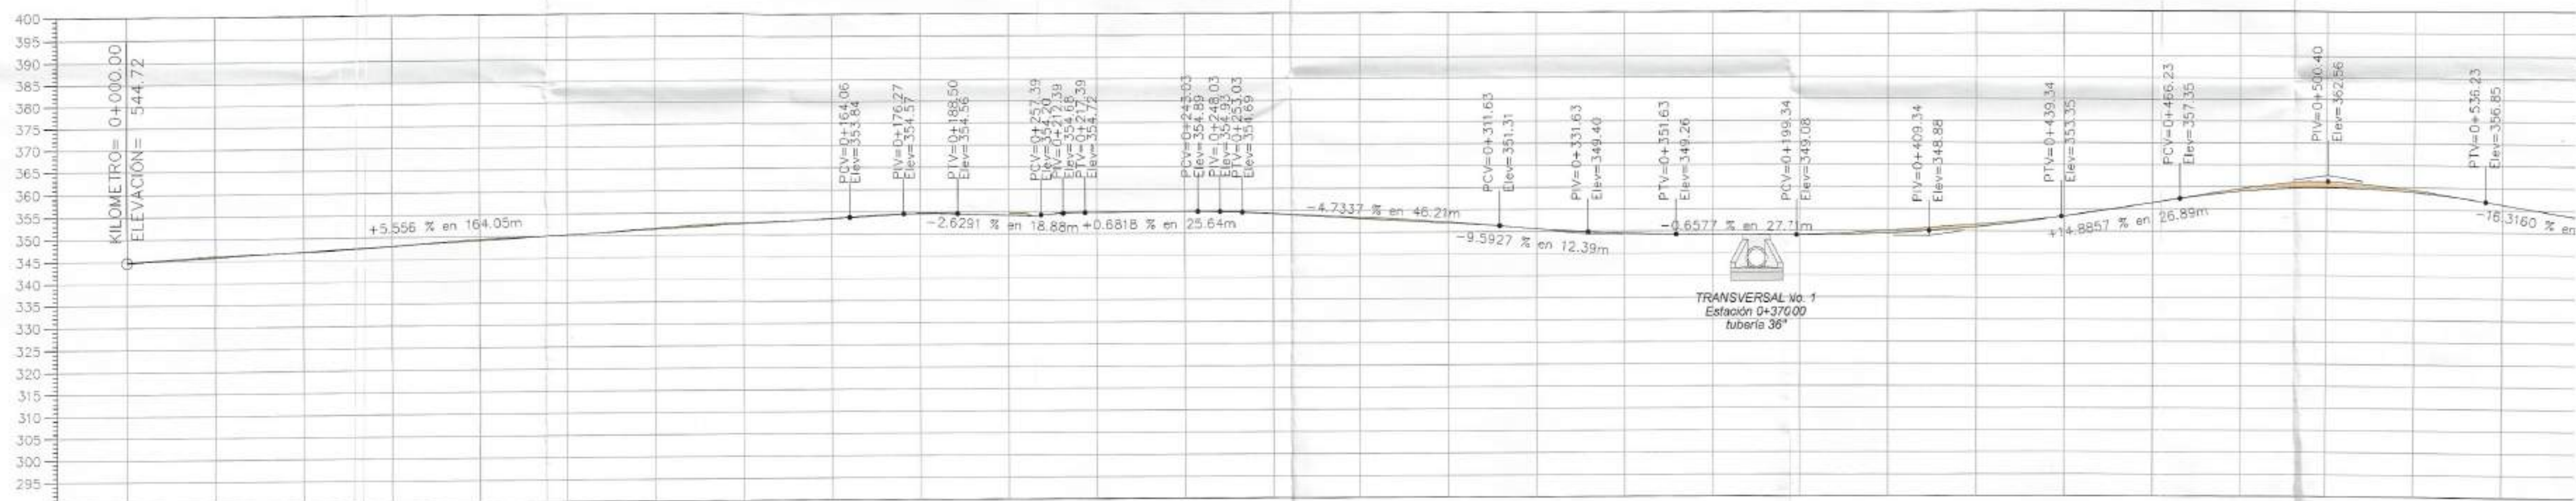

TIPO DE MATERIAL	FACTOR DE ABUNDAMIENTO	FACTOR DE COMPACTACION	ORDENADAS DE LA CURVA MASA	VOLUMEN	ESPESOR	ELEVACION
TERRAPLEN						
CORTE						
TERRAPLEN						
CORTE						
SUBRASANTE						
TERRENO						

PERFIL EST. 0+000 A 0+540
ESCALA 1:900



ADMINISTRACION
2024 - 2028

MUNICIPALIDAD DE
COBAN, A.V.
Dirección de Perfilación y
Elaboración de proyectos

PROYECTO:
MEJORAMIENTO CAMINO RURAL
(PAVIMENTO RIGIDO) DEL CASERIO LA
SULTANA HACIA EL CASERIO ROCJA TZIN,
COBAN, ALTA VERAPAZ

No. SNIP:
353493

UBICACIÓN:
CASERIO LA SULTANA,
COBAN ALTA VERAPAZ

CONTIENE:
PLANTA PERFIL
0+000.00 : 0+540.00

DISEÑO:
DIRECCIÓN DE PERFILACION Y
ELABORACIÓN DE PROYECTOS

DIBUJO:
DIRECCIÓN DE PERFILACION Y
ELABORACIÓN DE PROYECTOS

CALCULO:
DIRECCIÓN DE PERFILACION Y
ELABORACIÓN DE PROYECTOS

Vo. Bo. :

[Signature]
Alexis Abraham Peralta Morales
INGENIERO CIVIL
CO. VERAPAZ, A.V.


AR O E T I N S

MAGNITUD
1 085 MP.


FECHA:
SEPTIEMBRE - 2025

ESCALA:
INDICADA

HOJA A-1
05
11

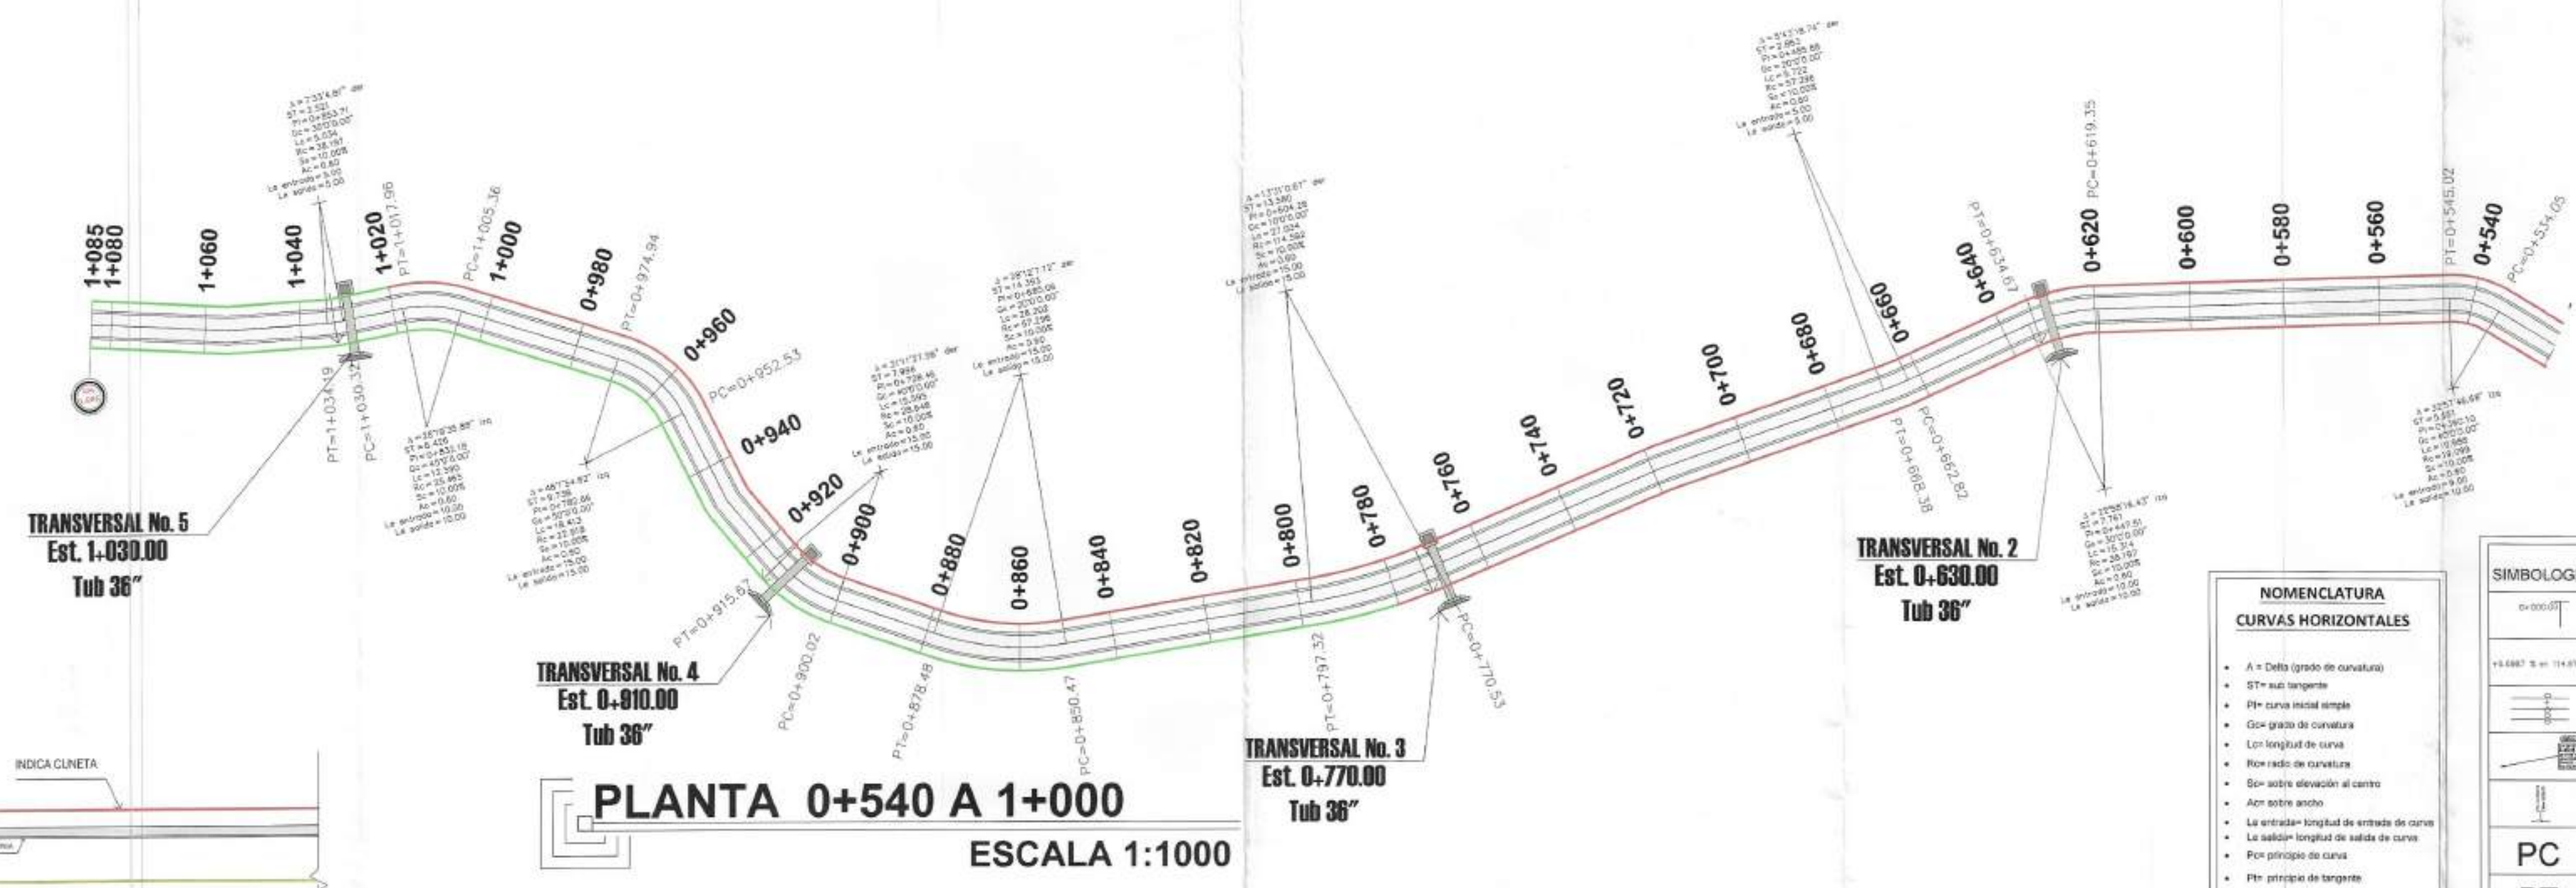


PLANTA 0+540 A 1+000
ESCALA 1:1000

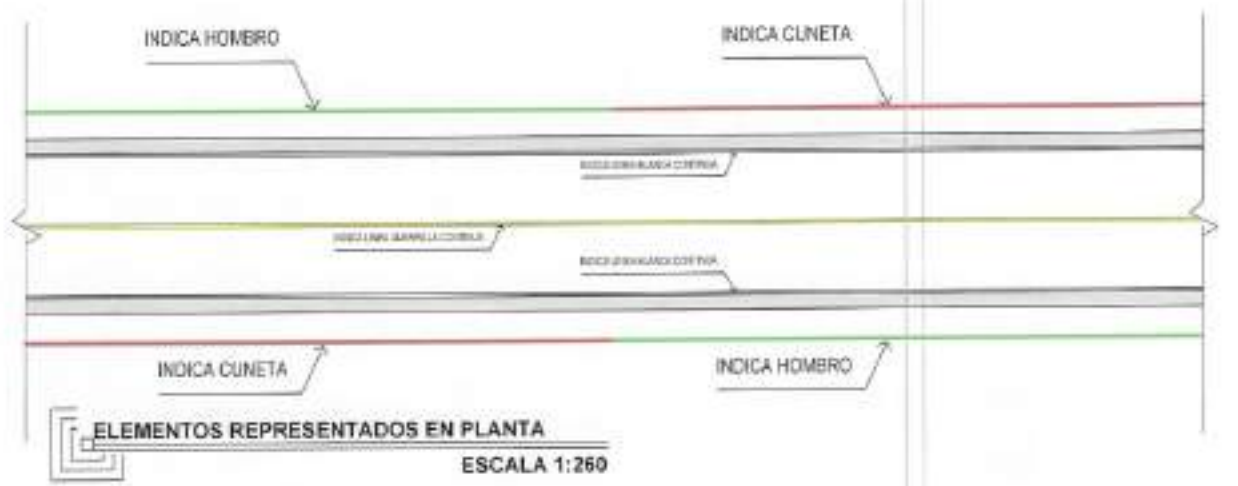

- NOMENCLATURA CURVAS HORIZONTALES**
- A = Delta (grado de curvatura)
 - ST = tangente simple
 - PT = punto de tangencia
 - GC = grado de curvatura
 - LC = longitud de curva
 - RC = radio de curvatura
 - SC = sobre elevación al centro
 - AC = sobre ancho
 - La = longitud de curva
 - La = longitud de curva
 - La = longitud de curva
- NOMENCLATURA CURVAS VERTICALES**
- PCV = principio de curva vertical
 - ELV = elevación
 - PIV = punto de intersección vertical
 - PTV = principio de tangente vertical
 - LVC = longitud de curva vertical

SIMBOLOGIA	DESCRIPCIÓN
0+540.00	Estacionamiento
+0.00%	Pendiente en perfil
1+000.00	Caminamiento en planta
PC	Curva Horizontal
PT	Curva Vertical
PC	PRINCIPIO DE CURVA HORIZONTAL
PT	PRINCIPIO DE TANGENTE HORIZONTAL
PC	tubería en planta, Caja cabezal en entrada y muro cabezal en salida
PT	Indica cuneta en planta
PC	Indica hombro en planta

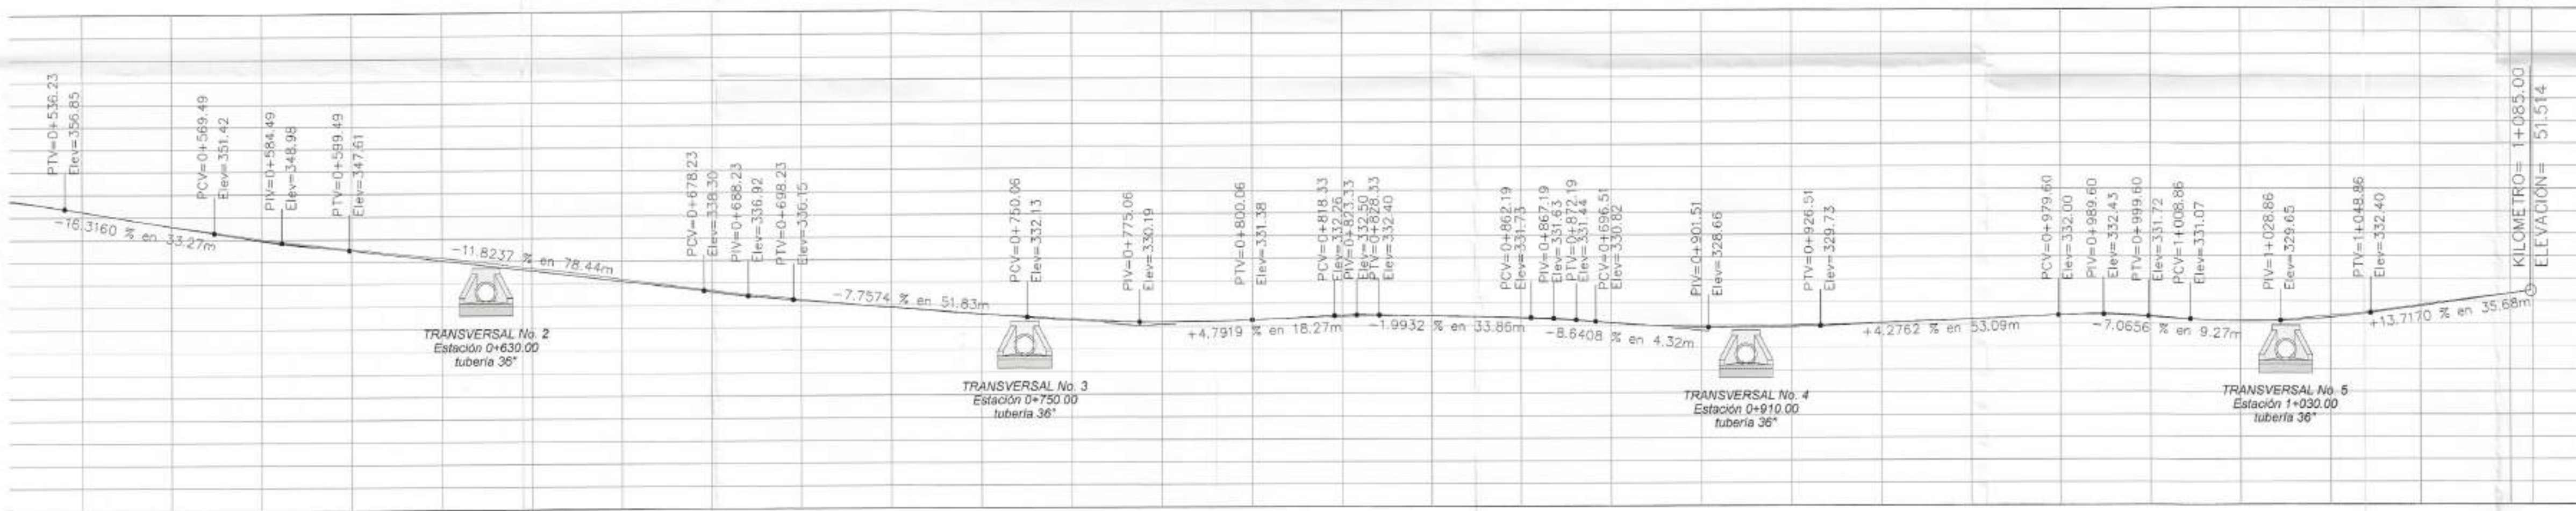

0+540.00	356.25	356.24	0.01	29.91	0.00	10.441
0+560.00	353.06	352.97	0.08	6.96	0.38	10.448
0+580.00	350.12	349.84	0.28	19.19	0.38	10.466
0+600.00	347.80	347.57	0.24	29.11	0.00	10.496
0+620.00	345.75	345.74	0.00	13.86	3.13	10.506
0+640.00	343.41	343.56	0.15	0.01	8.27	10.498
0+660.00	340.93	340.81	0.13	11.25	5.14	10.504
0+680.00	338.35	338.06	0.29	31.84	0.00	10.536
0+700.00	335.24	335.01	0.23	33.69	0.00	10.570
0+720.00	334.36	334.46	0.09	13.10	5.33	10.577
0+740.00	332.83	332.91	0.08	0.95	10.45	10.568
0+760.00	331.76	331.48	0.28	17.38	5.11	10.580
0+780.00	330.95	330.93	0.02	22.12	5.05	10.597
0+800.00	331.36	331.38	0.02	6.33	10.03	10.594
0+820.00	332.03	332.33	0.30	0.65	20.79	10.573
0+840.00	332.12	332.17	0.05	2.32	18.81	10.557
0+860.00	331.65	331.77	0.12	5.24	11.90	10.550
0+880.00	330.46	330.53	0.08	4.00	13.62	10.541
0+900.00	329.68	329.50	0.18	11.75	4.85	10.548
0+920.00	329.84	329.51	0.34	29.48	1.30	10.576
0+940.00	330.40	330.31	0.09	22.29	1.16	10.597
0+960.00	331.19	331.16	0.03	7.75	2.93	10.602
0+980.00	331.99	332.02	0.03	4.30	6.90	10.599
1+000.00	331.55	331.69	0.14	0.02	11.63	10.587
1+020.00	330.71	330.60	0.11	5.64	8.07	10.585
1+040.00	331.81	331.38	0.42	24.54	0.40	10.609
1+060.00	334.16	333.92	0.24	33.48	0.00	10.643
1+080.00	336.73	336.67	0.06	18.33	0.00	10.661
1+085.00						

PERFIL EST. 0+540 A 1+000
ESCALA 1:900



ADMINISTRACION
2024 - 2028

MUNICIPALIDAD DE
COBAN, A.V.
Dirección de Perfilación y
Elaboración de proyectos

PROYECTO:
MEJORAMIENTO CAMINO RURAL
(PAVIMENTO RIGIDO) DEL CASERIO LA
SULTANA HACIA EL CASERIO ROCJA TZIN,
COBAN, ALTA VERAPAZ

No. SNIP:

353493

UBICACIÓN:

CASERIO LA SULTANA,
COBAN ALTA VERAPAZ

CONTIENE:

PLANTA PERFIL
0+540.00 : 1+000.00

DISÑO:

DIRECCIÓN DE PERFILACION Y
ELABORACIÓN DE PROYECTOS

DIBUJO:

DIRECCIÓN DE PERFILACION Y
ELABORACIÓN DE PROYECTOS

CALCULO:

DIRECCIÓN DE PERFILACION Y
ELABORACIÓN DE PROYECTOS

Vo. Bo.:

Alcaldía Municipal
Cobán, Alta Verapaz
C. A. L. 177

MAGNITUD:
1:085 MF.
FECHA:
SEPTIEMBRE - 2025
ESCALA:
INDICADA

HOJA A-1
06
11



ADMINISTRACION
2024 - 2028

MUNICIPALIDAD DE
COBAN, A.V.
Dirección de Perfilación y
Elaboración de proyectos

PROYECTO:
MEJORAMIENTO CAMINO RURAL
(PAVIMENTO RIGIDO) DEL CASERIO LA
SULTANA HACIA EL CASERIO ROCJA TZIN,
COBAN, ALTA VERAPAZ

No. SNIP:

353493

UBICACIÓN:

CASERIO LA SULTANA,
COBAN ALTA VERAPAZ

CONTIENE:

SECCIONES
TRANSVERSALES
0+000.00 : 0+460.00

DISEÑO:

DIRECCIÓN DE PERFILACION Y
ELABORACIÓN DE PROYECTOS

DIBUJO:

DIRECCIÓN DE PERFILACION Y
ELABORACIÓN DE PROYECTOS

CALCULO:

DIRECCIÓN DE PERFILACION Y
ELABORACIÓN DE PROYECTOS

Vo. Bo.:



SECCIONES TRANSVERSALES

ESCALA 1:90

ARQ. EST. INS.

MAGNITUD:
1 085 M².










HOJA A-1

FECHA:
SEPTIEMBRE - 2025

07

ESCALA:
INDICADA

11

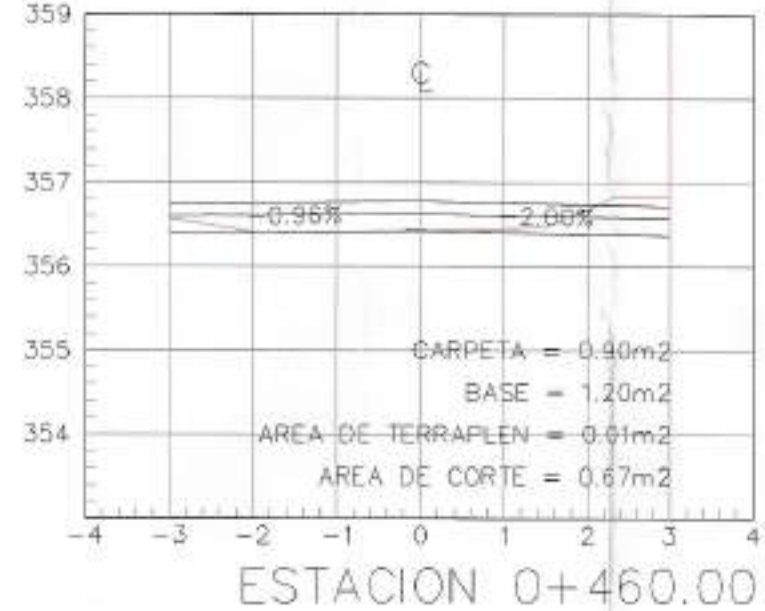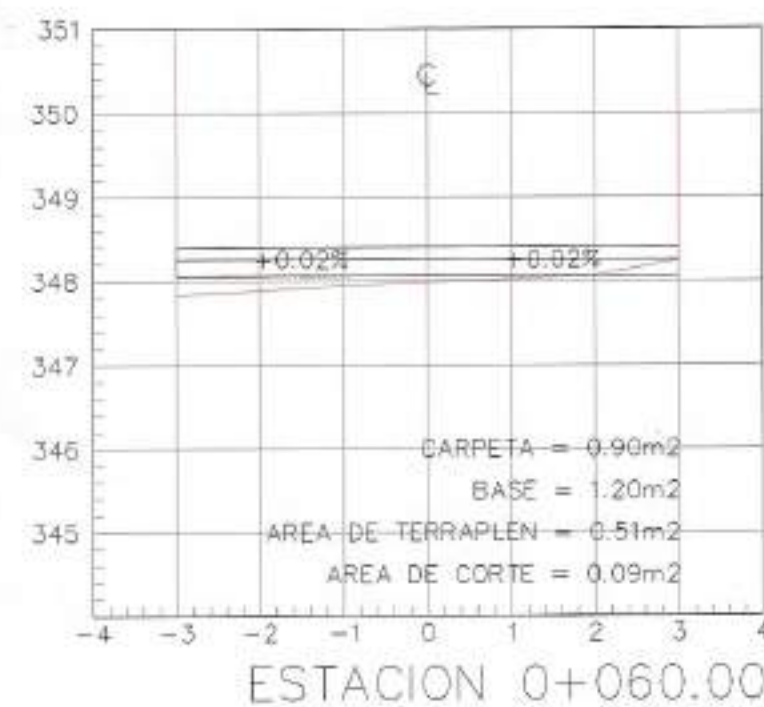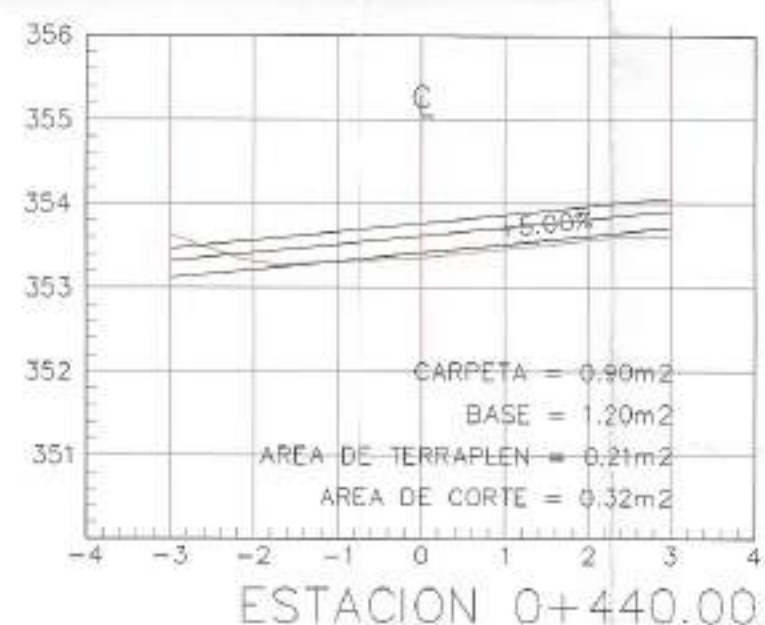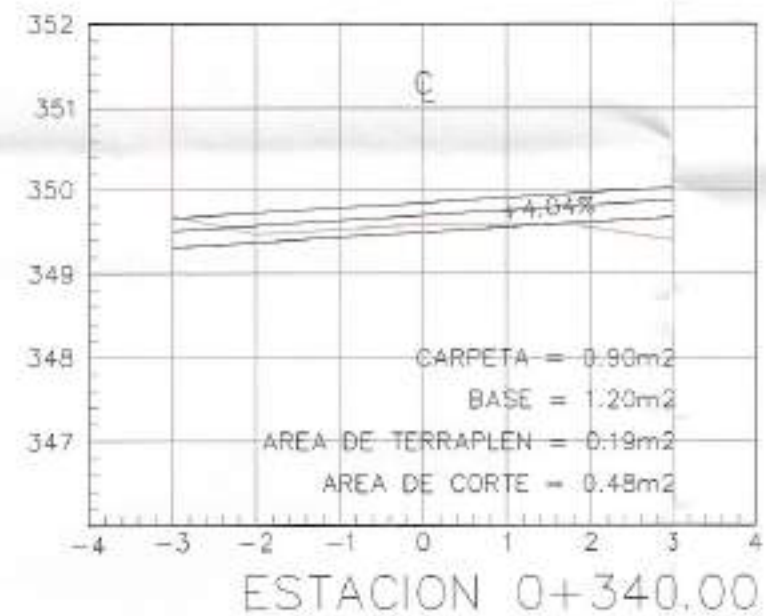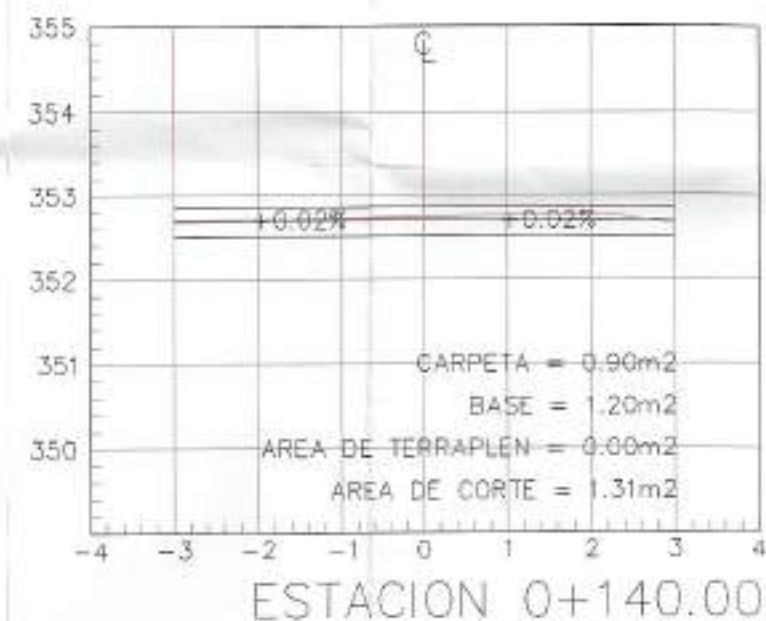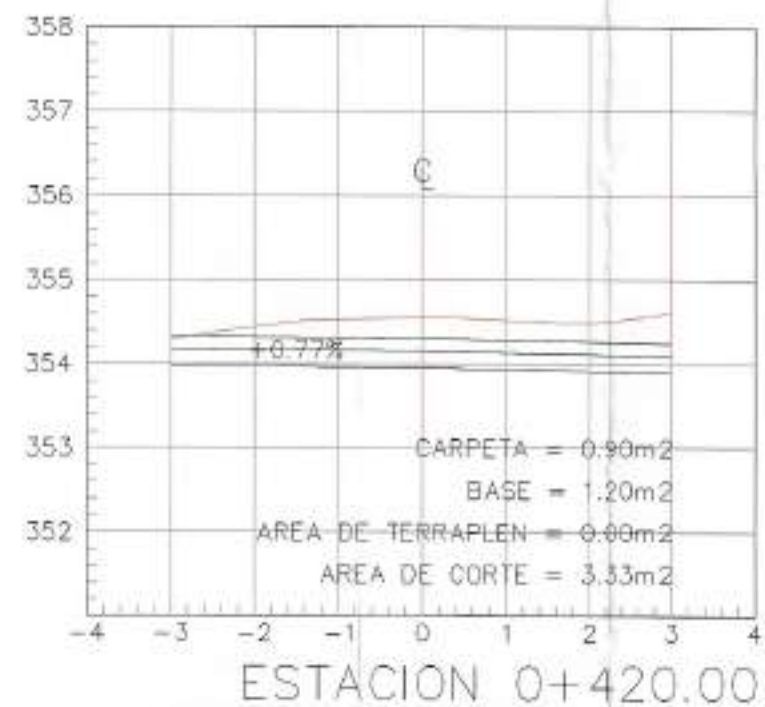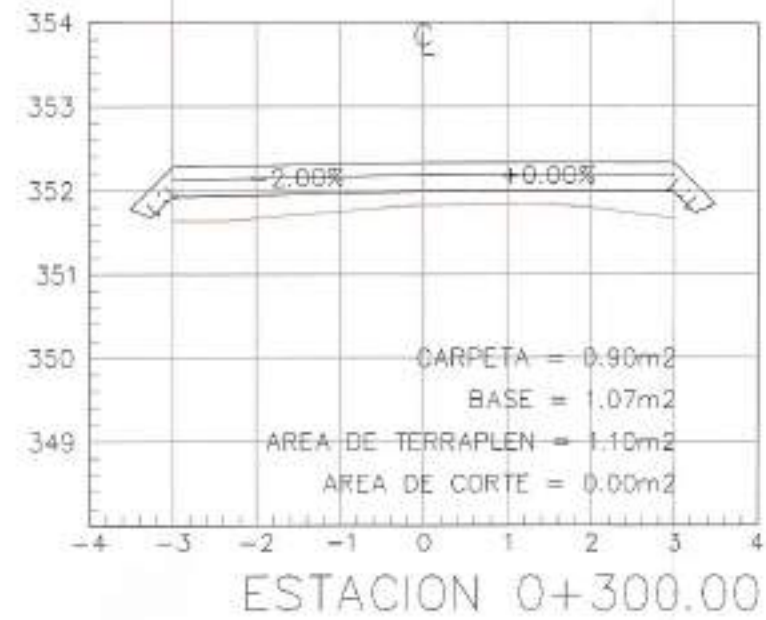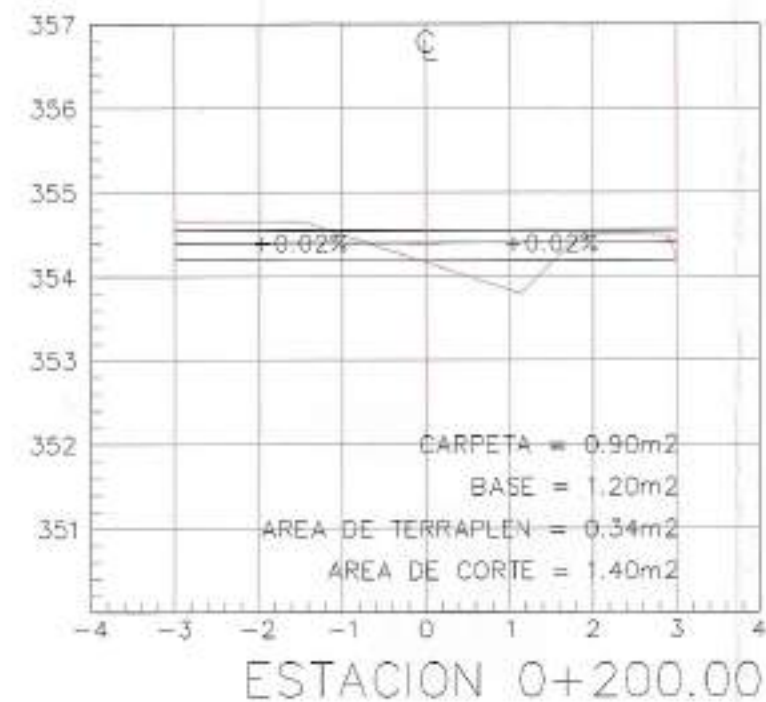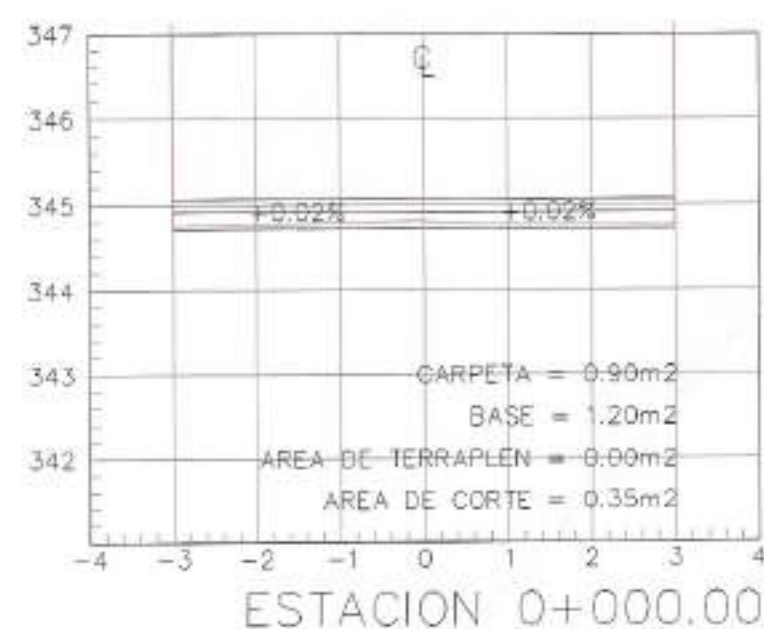



ADMINISTRACION
2024 - 2028

MUNICIPALIDAD DE
COBAN, A.V.
Dirección de Perfilación y
Elaboración de proyectos

PROYECTO:
MEJORAMIENTO CAMINO RURAL
(PAVIMENTO RIGIDO) DEL CASERIO LA
SULTANA HACIA EL CASERIO ROCHA TZIN,
COBAN, ALTA VERAPAZ

No. SNIP:

353493

UBICACIÓN:

CASERIO LA SULTANA,
COBAN ALTA VERAPAZ

CONTIENE:

SECCIONES
TRANSVERSALES
0+480.00 : 0+940.00

DISEÑO:

DIRECCIÓN DE PERFILACION Y
ELABORACIÓN DE PROYECTOS

DIBUJO:

DIRECCIÓN DE PERFILACION Y
ELABORACIÓN DE PROYECTOS

CALCULO:






DIRECCIÓN DE PERFILACION Y
ELABORACIÓN DE PROYECTOS

Vo. Bo. :



SECCIONES TRANSVERSALES

ESCALA 1:90

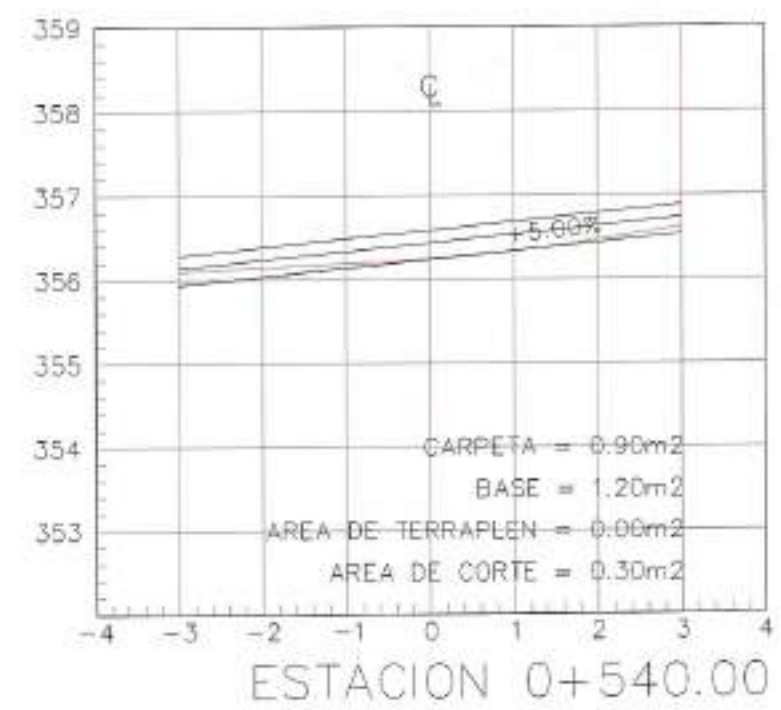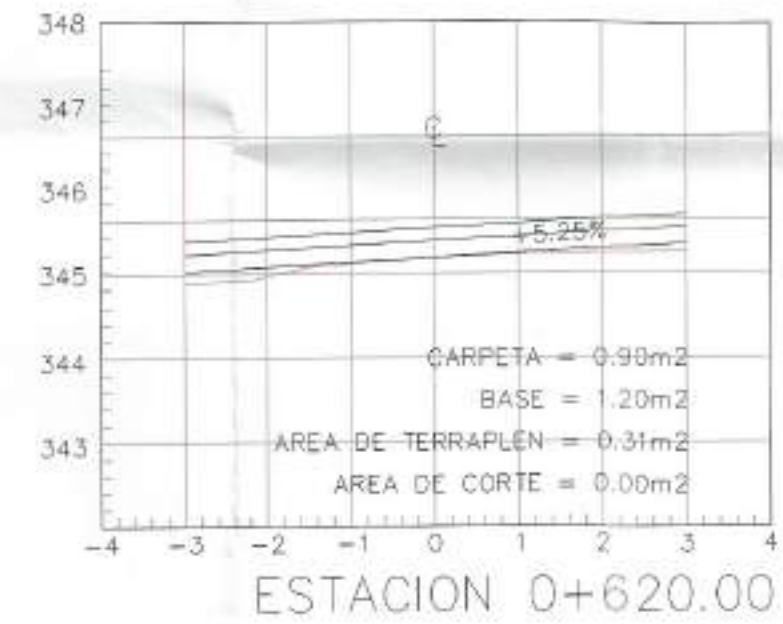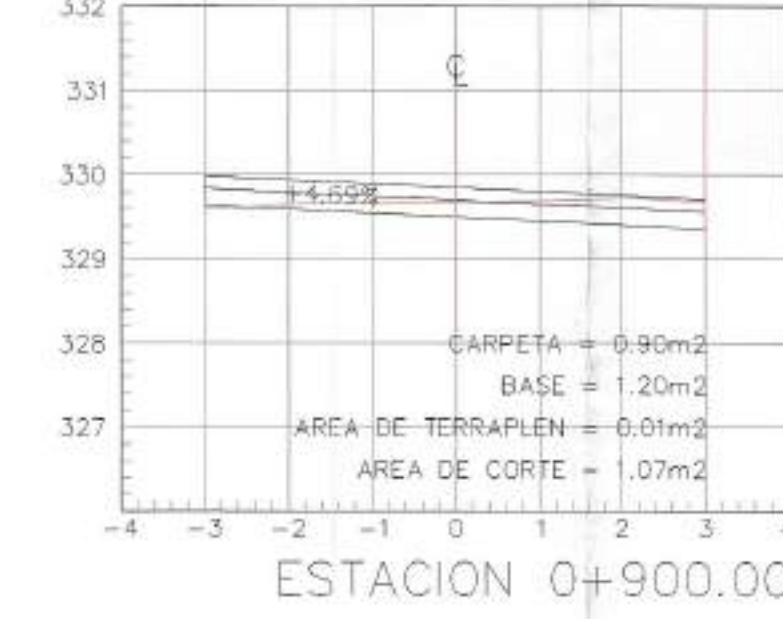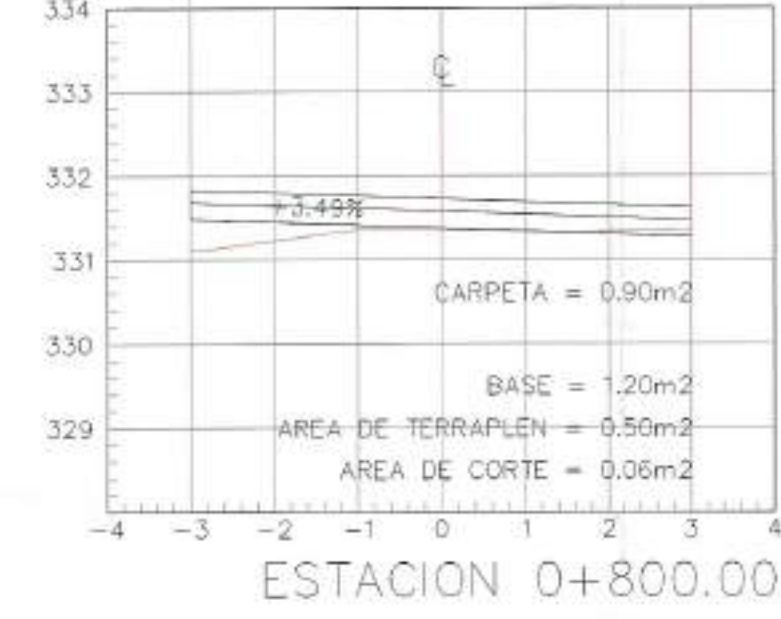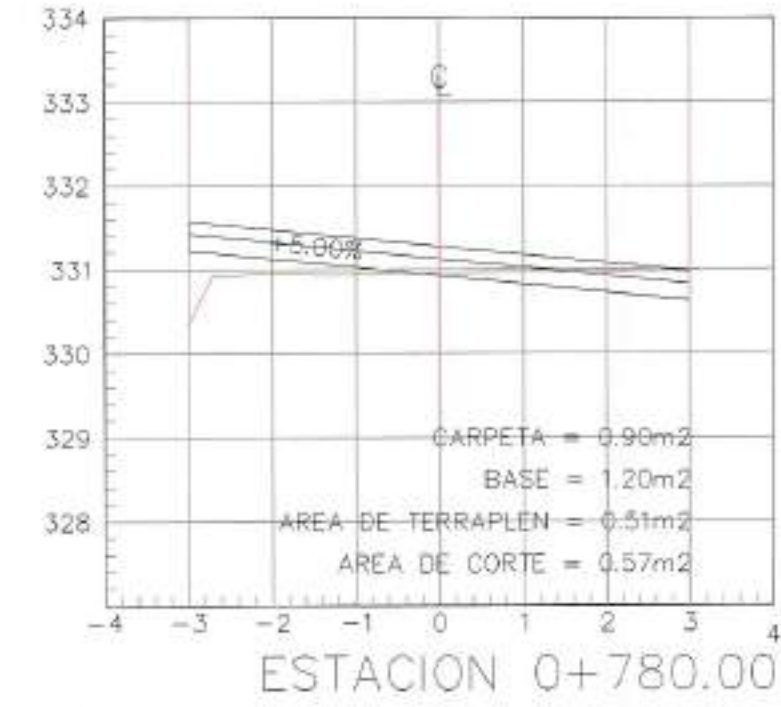

MAGNITUD:
1 085 M²

FECHA:
SEPTIEMBRE - 2025

ESCALA:
INDICADA

HOJA A-1
08
11