



ADMINISTRACION  
2024 - 2028

MUNICIPALIDAD DE  
COBAN, A.V.  
Dirección de Perfilación y  
Elaboración de proyectos

PROYECTO:  
MEJORAMIENTO CAMINO RURAL  
(PAVIMENTO RIGIDO) DEL CASERIO LA  
SULTANA HACIA EL CASERIO ROCJA TZIN,  
COBAN, ALTA VERAPAZ

No. SNIP:

353493

UBICACIÓN:

CASERIO LA SULTANA,  
COBAN ALTA VERAPAZ

CONTIENE:

SECCIONES  
TRANSVERSALES  
0+480.00 : 0+940.00

DISEÑO:

DIRECCIÓN DE PERFILACION Y  
ELABORACIÓN DE PROYECTOS










DIBUJO:

DIRECCIÓN DE PERFILACION Y  
ELABORACIÓN DE PROYECTOS

CALCULO:

DIRECCIÓN DE PERFILACION Y  
ELABORACIÓN DE PROYECTOS

Vo. Bo. :

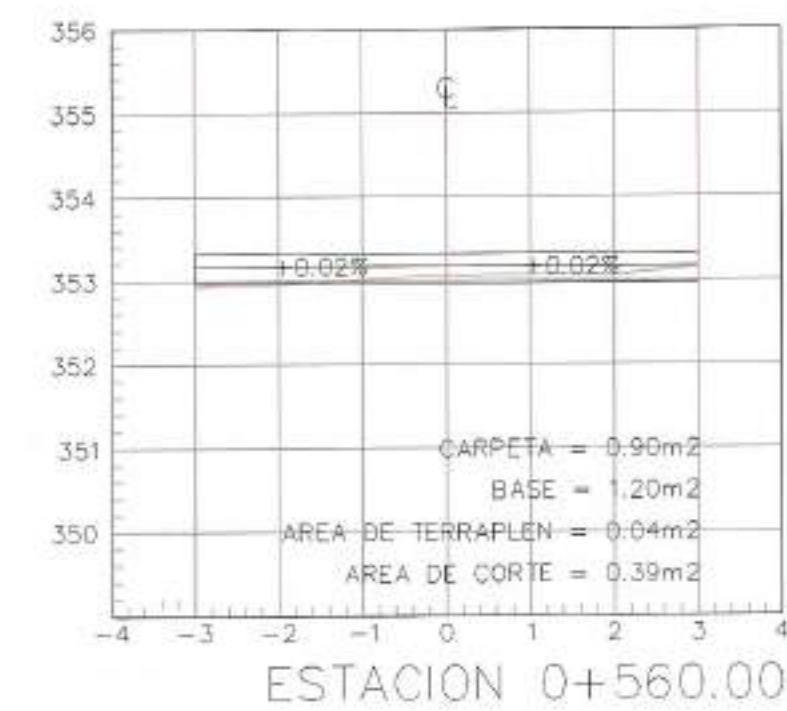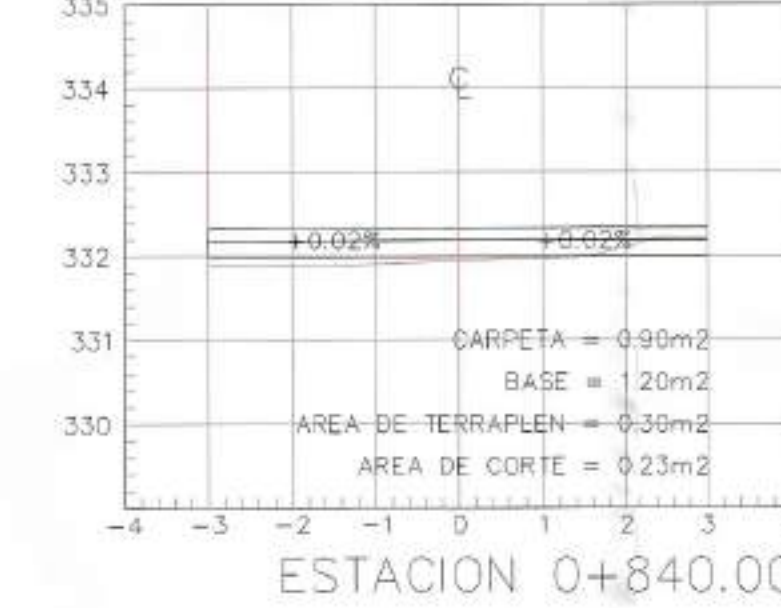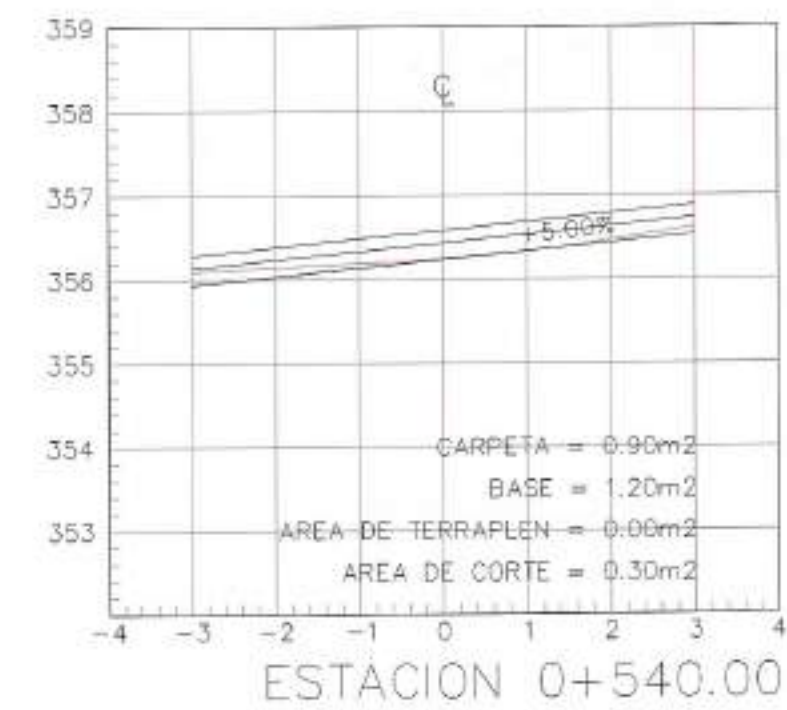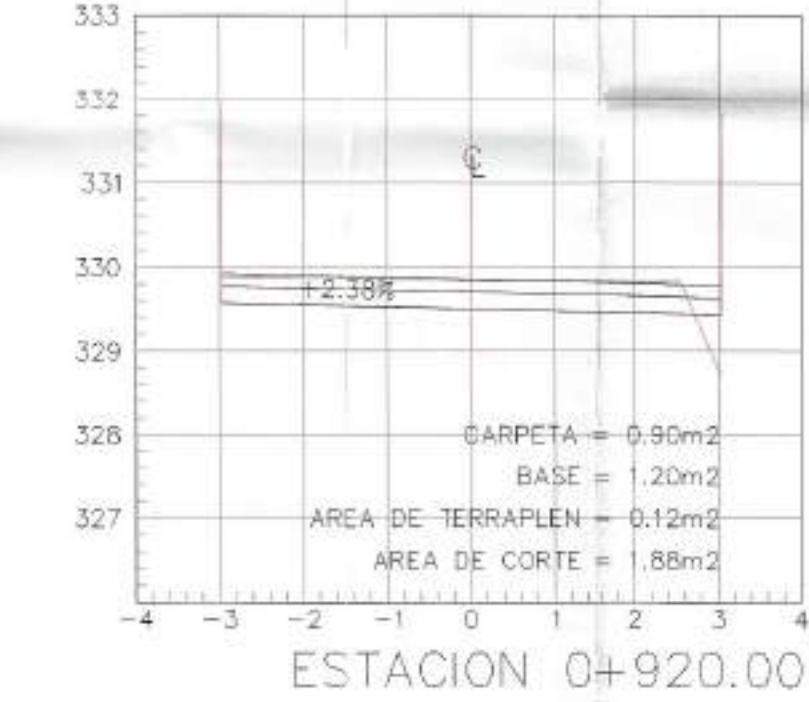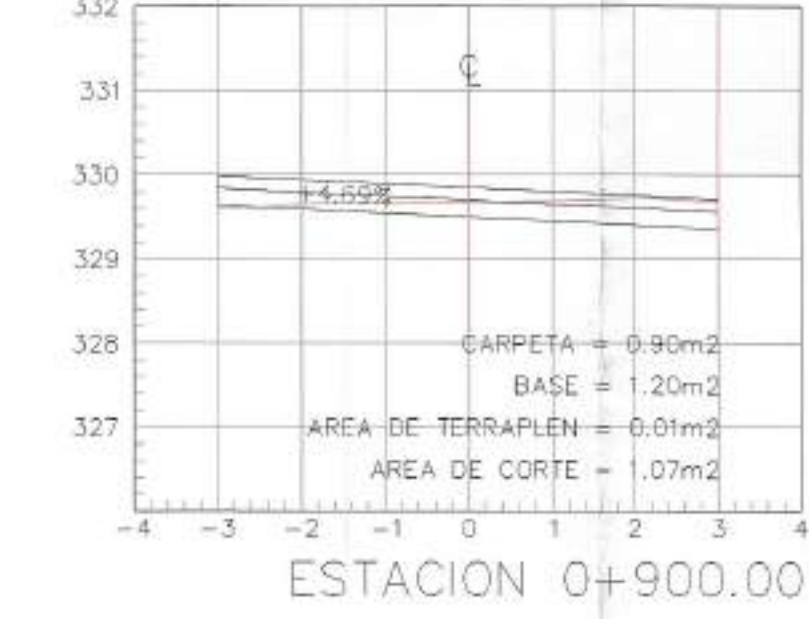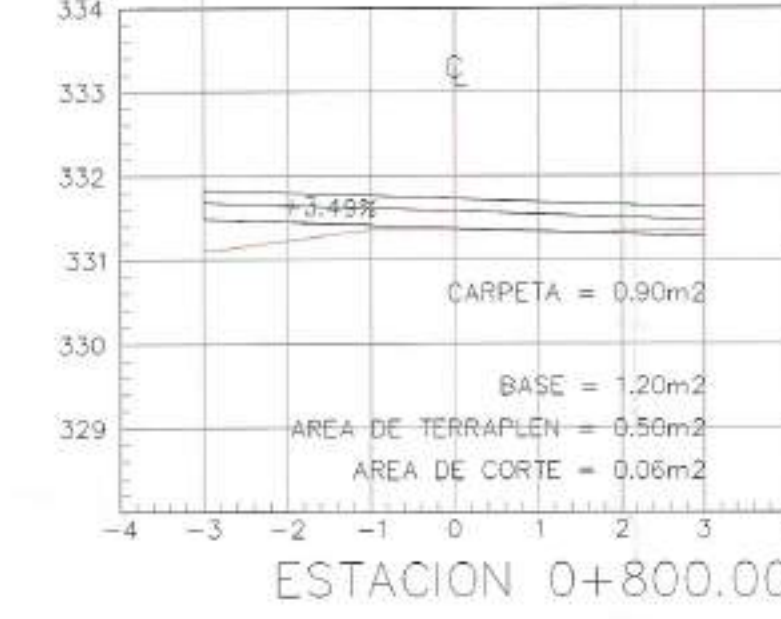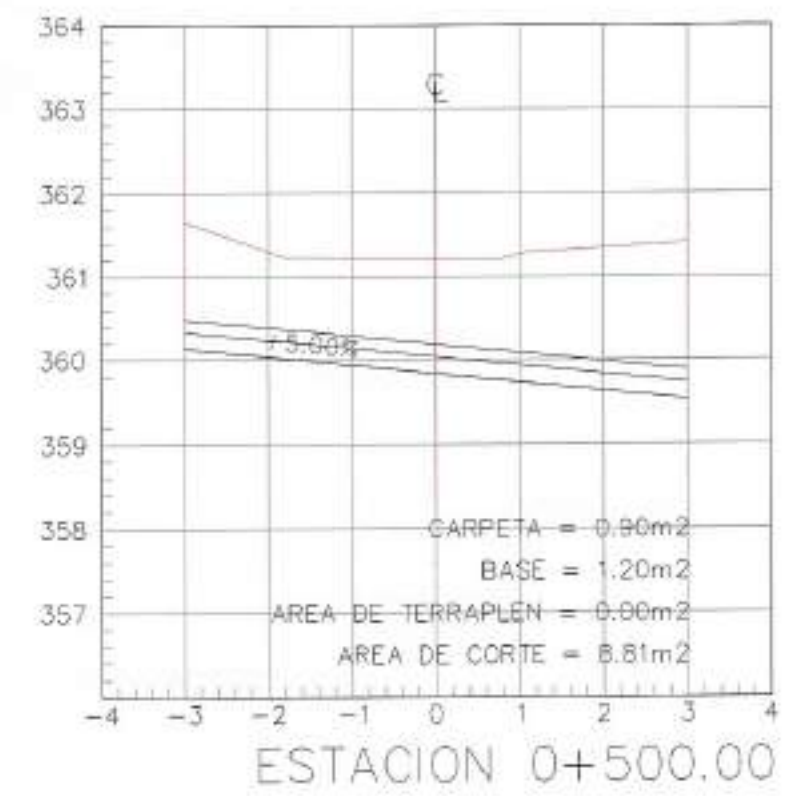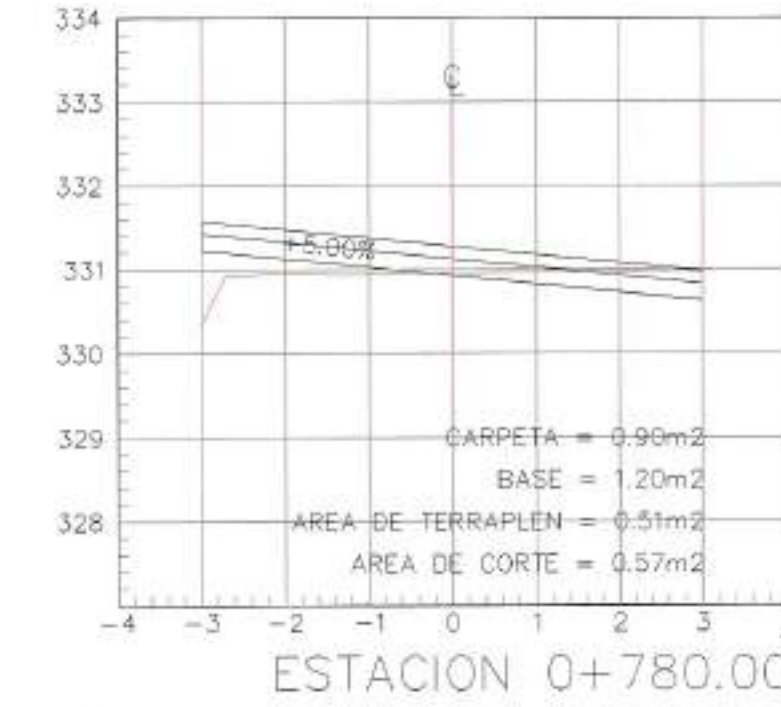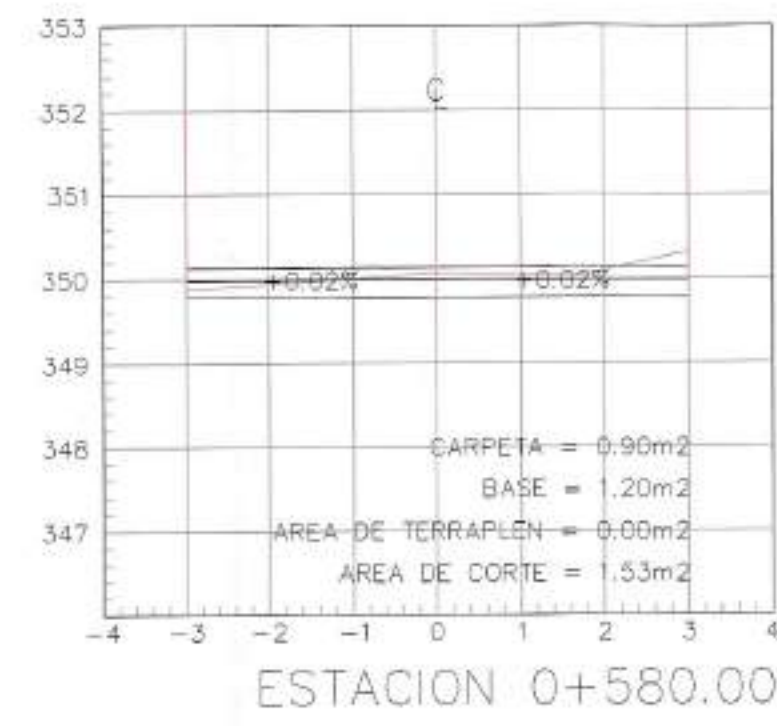

SECCIONES TRANSVERSALES  
ESCALA 1:90

MAGNITUD:  
1 085 M.  
FECHA:  
SEPTIEMBRE - 2025  
ESCALA:  
INDICADA  
HOJA A-1  
08  
11



ADMINISTRACION  
2024 - 2028

MUNICIPALIDAD DE  
COBAN, A.V.

Dirección de Perfilación y  
Elaboración de proyectos

PROYECTO:

MEJORAMIENTO CAMINO RURAL  
(PAVIMENTO RIGIDO) DEL CASERIO LA  
SULTANA HACIA EL CASERIO ROCJA TZIN,  
COBAN, ALTA VERAPAZ

No. SNIP:

353493

UBICACIÓN:

CASERIO LA SULTANA,  
COBAN ALTA VERAPAZ

CONTIENE:

SECCIONES  
TRANSVERSALES  
0+960.00 : 1+085.00

CUADRO DE  
VOLUMENES

DISEÑO:

DIRECCIÓN DE PERFILACION Y  
ELABORACIÓN DE PROYECTOS

DIBUJO:

DIRECCIÓN DE PERFILACION Y  
ELABORACIÓN DE PROYECTOS

CALCULO:

DIRECCIÓN DE PERFILACION Y  
ELABORACIÓN DE PROYECTOS

Va. Bo.:

1085 MP.






SEPTIEMBRE - 2025

ESCALA:  
INDICADA

HOJA A-1

09


11

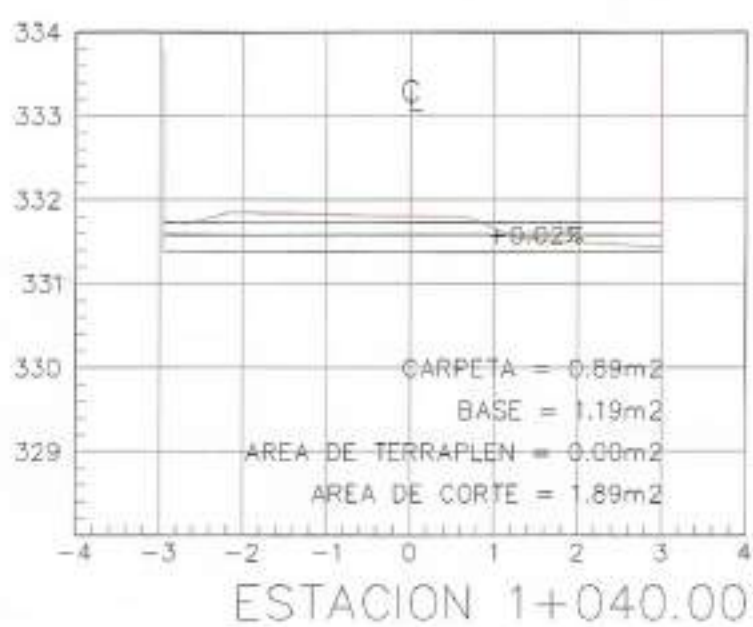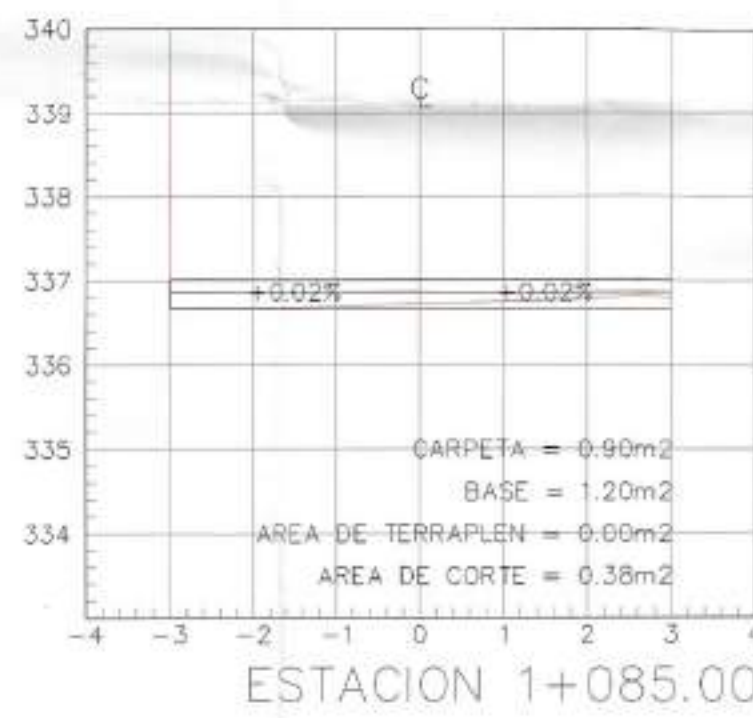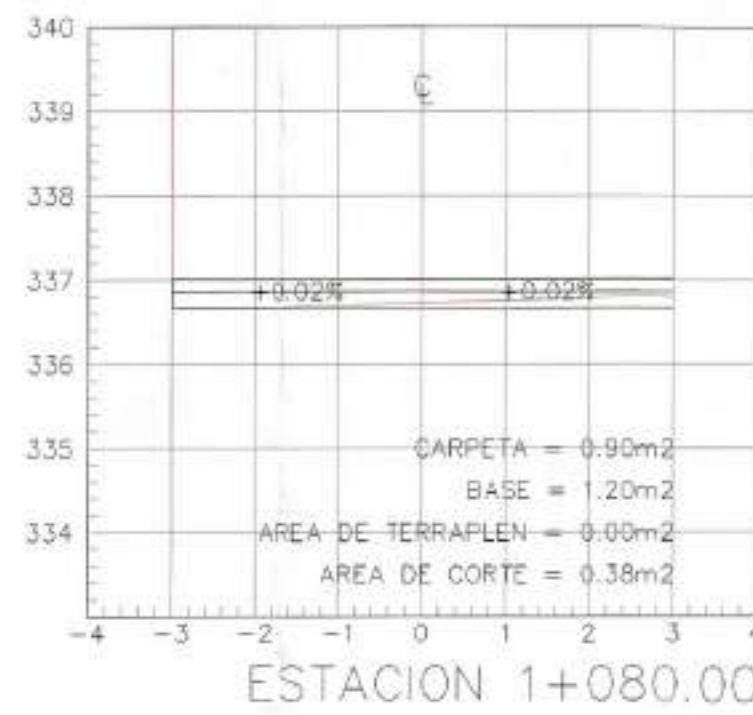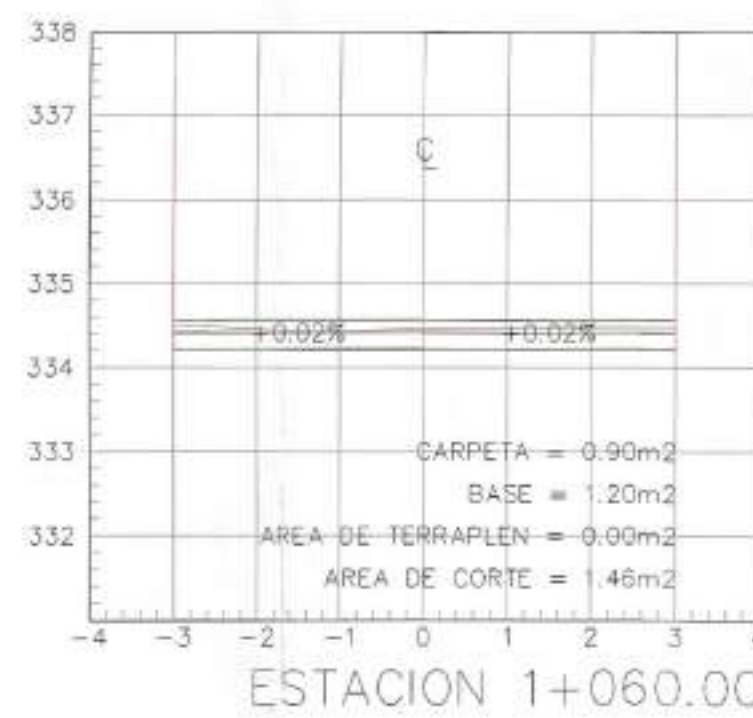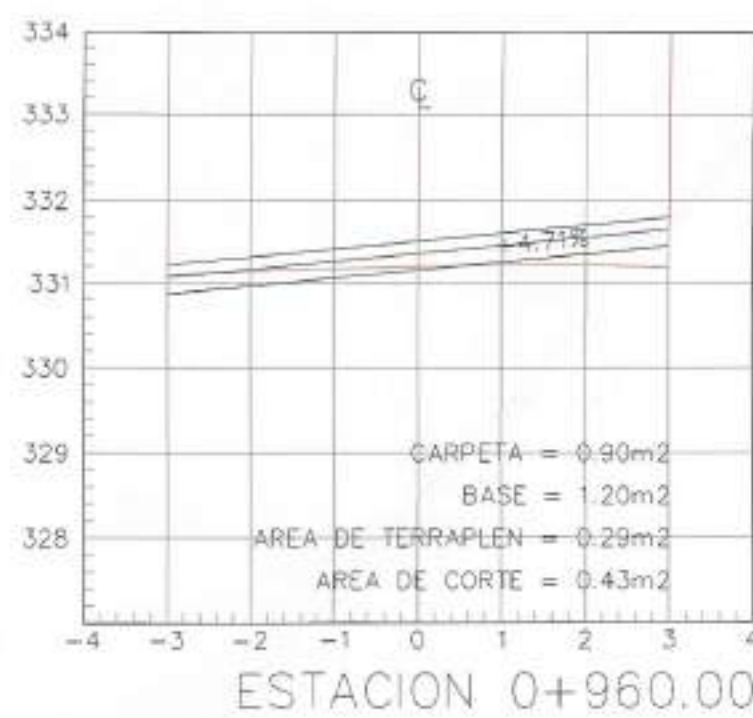

| SIMBOLOGIA |                       |
|------------|-----------------------|
| DC         | DESPALME EN CORTE     |
| DT         | DESPALME EN TERRAPLEN |
| C          | CORTE                 |
| T          | TERRAPLEN             |
| BH         | BASE                  |
| CA         | CARPETA               |


NOTA: Los conceptos que se incluirán  
en el cálculo de volúmenes aparecen  
subrayados. Se ha considerado el  
terreno ya despalado al calcular  
áreas y volúmenes de corte y terraplen.

| COORDENADA INICIAL DE CURVA MASA    |             |            | 10,000.00 |      | AREAS    |      |      |      |      |      |                                 |                |          | VOLUMENES |       |       |       |       |                                      |           |  |
|-------------------------------------|-------------|------------|-----------|------|----------|------|------|------|------|------|---------------------------------|----------------|----------|-----------|-------|-------|-------|-------|--------------------------------------|-----------|--|
| SECCIONES DE TN LEVANTADAS EN CAMPO | ELEVACIONES |            | ESPESORES |      | DESPALME |      | C    | I    | BH   | CA   | Factor de abundamiento en corte | SEMI-DISTANCIA | DESPALME |           | C     | I     | BH    | CA    | RESUMEN (ORDENADAS DE LA CURVA MASA) |           |  |
|                                     | TN          | SUBRASANTE | C         | T    | DC       | DT   |      |      |      |      |                                 |                | DC       | DT        |       |       |       |       |                                      |           |  |
|                                     |             
| 0+000.000                           | 344.811     | 344.721    | 0.00      | 0.00 | 0.00     | 0.00 | 0.35 | 0.00 | 1.20 | 0.90 |                                 |                |          |           |       |       |       |       | 0+000.000                            | 10,000.00 |  |
| 0+020.000                           | 346.055     | 345.832    | 0.09      | 0.00 | 0.00     | 0.00 | 1.31 | 0.00 | 1.20 | 0.90 | 1.00                            | 10.00          | 0.00     | 0.00      | 8.45  | 0.00  | 24.00 | 18.00 | 0+020.000                            | 10,009.59 |  |
| 0+040.000                           | 346.849     | 346.944    | 0.03      | 0.00 | 0.00     | 0.00 | 0.00 | 0.53 | 1.07 | 0.90 | 1.00                            | 10.00          | 0.00     | 0.00      | 7.75  | 2.93  | 24.00 | 18.00 | 0+040.000                            | 10,016.07 |  |
| 0+060.000                           | 347.988     | 348.056    | 0.00      | 0.03 | 0.00     | 0.00 | 0.09 | 0.51 | 1.20 | 0.90 | 1.00                            | 10.00          | 0.00     | 0.00      | 4.30  | 8.90  | 24.00 | 18.00 | 0+060.000                            | 10,009.36 |  |
| 0+080.000                           | 348.448     | 349.168    | 0.00      | 0.14 | 0.00     | 0.00 | 1.64 | 0.00 | 1.20 | 0.90 | 1.00                            | 10.00          | 0.00     | 0.00      | 0.02  | 8.24  | 22.75 | 18.00 | 0+080.000                            | 10,005.12 |  |
| 0+100.000                           | 350.229     | 350.280    | 0.11      | 0.00 | 0.00     | 0.00 | 0.23 | 0.30 | 1.20 | 0.90 | 1.00                            | 10.00          | 0.00     | 0.00      | 5.64  | 6.40  | 22.75 | 18.00 | 0+100.000                            | 10,003.80 |  |
| 0+120.000                           | 350.628     | 350.362    | 0.00      | 0.00 | 0.00     | 0.00 | 1.38 | 0.00 | 1.20 | 0.90 | 1.00                            | 2.27           | 0.00     | 0.00      | 0.00  | 0.00  | 5.45  | 4.09  | 0+120.000                            | 9,993.17  |  |
| 0+140.000                           | 352.736     | 352.500    | 0.09      | 0.00 | 0.00     | 0.00 | 1.31 | 0.00 | 1.20 | 0.90 | 1.00                            | 10.00          | 0.00     | 0.00      | 8.45  | 1.16  | 24.00 | 18.00 | 0+140.000                            | 9,981.16  |  |
| 0+160.000                           | 353.521     | 353.615    | 0.03      | 0.00 | 0.00     | 0.00 | 0.00 | 0.53 | 1.07 | 0.90 | 1.00                            | 10.00          | 0.00     | 0.00      | 7.18  | 2.38  | 24.00 | 18.00 | 0+160.000                            | 9,983.11  |  |
| 0+180.000                           | 354.727     | 354.727    | 0.00      | 0.00 | 0.00     | 0.00 | 0.01 | 0.12 | 1.18 | 0.88 | 1.00                            | 2.27           | 0.00     | 0.00      | 0.00  | 0.00  | 5.45  | 4.09  | 0+180.000                            | 9,988.00  |  |
| 0+200.000                           | 354.169     | 354.202    | 0.00      | 0.03 | 0.00     | 0.00 | 1.40 | 0.34 | 1.20 | 0.90 | 1.00                            | 10.00          | 0.00     | 0.00      | 14.14 | 4.55  | 23.75 | 17.83 | 0+200.000                            | 9,991.82  |  |
| 0+220.000                           | 354.700     | 354.736    | 0.00      | 0.04 | 0.00     | 0.00 | 0.23 | 0.64 | 1.19 | 0.90 | 1.00                            | 10.00          | 0.00     | 0.00      | 16.27 | 9.79  | 23.94 | 17.96 | 0+220.000                            | 10,025.42 |  |
| 0+240.000                           | 354.896     | 354.872    | 0.02      | 0.00 | 0.00     | 0.00 | 0.26 | 0.52 | 1.20 | 0.90 | 1.00                            | 10.00          | 0.00     | 0.00      | 4.89  | 11.60 | 23.94 | 17.96 | 0+240.000                            | 10,090.40 |  |
| 0+260.000                           | 354.354     | 354.360    | 0.00      | 0.01 | 0.00     | 0.00 | 0.01 | 0.18 | 1.07 | 0.90 | 1.00                            | 10.00          | 0.00     | 0.00      | 2.76  | 7.00  | 22.75 | 18.00 | 0+260.000                            | 10,124.75 |  |
| 0+280.000                           | 353.458     | 353.414    | 0.04      | 0.00 | 0.00     | 0.00 | 0.19 | 0.15 | 1.20 | 0.90 | 1.00                            | 10.00          | 0.00     | 0.00      | 2.04  | 3.36  | 22.75 | 18.00 | 0+280.000                            | 10,132.42 |  |
| 0+300.000                           | 352.266     | 352.430    | 0.00      | 0.16 | 0.00     | 0.00 | 0.00 | 1.10 | 1.07 | 0.90 | 1.00                            | 10.00          | 0.00     | 0.00      | 1.91  | 12.54 | 22.75 | 18.00 | 0+300.000                            | 10,173.51 |  |
| 0+320.000                           | 350.604     | 350.590    | 0.01      | 0.00 | 0.00     | 0.00 | 0.48 | 0.58 | 1.17 | 0.87 | 1.00                            | 10.00          | 0.00     | 0.00      | 4.85  | 16.86 | 22.40 | 17.74 | 0+320.000                            | 10,296.14 |  |
| 0+340.000                           | 349.581     | 349.491    | 0.09      | 0.00 | 0.00     | 0.00 | 0.48 | 0.19 | 1.20 | 0.90 | 1.00                            | 10.00          | 0.00     | 0.00      | 9.65  | 7.70  | 23.68 | 17.74 | 0+340.000                            | 10,411.13 |  |
| 0+360.000                           | 349.231     | 349.209    | 0.02      | 0.00 | 0.00     | 0.00 | 0.20 | 0.00 | 1.08 | 0.90 | 1.00                            | 10.00          | 0.00     | 0.00      | 6.79  | 1.90  | 22.75 | 18.00 | 0+360.000                            | 10,441.03 |  |
| 0+380.000                           | 349.140     | 349.078    | 0.06      | 0.00 | 0.00     | 0.00 | 0.54 | 0.36 | 1.20 | 0.90 | 1.00                            | 10.00          | 0.00     | 0.00      | 7.41  | 3.60  | 22.75 | 18.00 | 0+380.000                            | 10,447.61 |  |
| 0+400.000                           | 350.067     | 349.498    | 0.57      | 0.00 | 0.00     | 0.00 | 3.17 | 0.00 | 1.20 | 0.90 | 1.00                            | 10.00          | 0.00     | 0.00      | 24.60 | 3.55  | 24.00 | 18.00 | 0+400.000                            | 10,466.42 |  |
| 0+420.000                           | 351.553     | 350.955    | 0.60      | 0.00 | 0.00     | 0.00 | 3.33 | 0.00 | 1.20 | 0.90 | 1.00                            | 10.00          | 0.00     | 0.00      | 14.80 | 0.00  | 24.00 | 18.00 | 0+420.000                            | 10,495.52 |  |
| 0+440.000                           | 353.385     | 353.447    | 0.00      | 0.05 | 0.00     | 0.00 | 0.32 | 0.21 | 1.20 | 0.90 | 1.00                            | 10.00          | 0.00     | 0.00      | 16.78 | 2.13  | 24.00 | 18.00 | 0+440.000                            | 10,506.25 |  |
| 0+460.000                           | 356.423     | 356.424    | 0.00      | 0.00 | 0.00     | 0.00 | 0.67 | 0.01 | 1.20 | 0.90 | 1.00                            | 10.00          | 0.00     | 0.00      | 9.88  | 2.21  | 24.00 | 18.00 | 0+460.000                            | 10,497.99 |  |
| 0+480.000                           | 359.596     | 358.979    | 0.62      | 0.00 | 0.00     | 0.00 | 3.45 | 0.00 | 1.20 | 0.90 | 1.00                            | 10.00          | 0.00     | 0.00      | 14.47 | 0.09  | 24.00 | 18.00 | 0+480.000                            | 10,504.09 |  |
| 0+500.000                           | 361.213     | 359.638    | 1.57      | 0.00 | 0.00     | 0.00 | 8.81 | 0.00 | 1.20 | 0.90 | 1.00                            | 10.00          | 0.00     | 0.00      | 26.74 | 0.00  | 24.00 | 18.00 | 0+500.000                            | 10,536.93 |  |
| 0+520.000                           | 359.387     | 358.913    | 0.47      | 0.00 | 0.00     | 0.00 | 2.69 | 0.00 | 1.20 | 0.90 | 1.00                            | 10.00          | 0.00     | 0.00      | 32.44 | 0.00  | 24.00 | 18.00 | 0+520.000                            | 10,569.63 |  |
| 0+540.000                           | 356.245     | 356.237    | 0.01      | 0.00 | 0.00     | 0.00 | 0.30 | 0.00 | 1.20 | 0.90 | 1.00                            | 10.00          | 0.00     | 0.00      | 26.91 | 0.00  | 24.00 | 18.00 | 0+540.000                            | 10,577.39 |  |
| 0+560.000                           | 353.055     | 352.974    | 0.08      | 0.00 | 0.00     | 0.00 | 0.39 | 0.04 | 1.20 | 0.90 | 1.00                            | 10.00          | 0.00     | 0.00      | 6.96  | 0.38  | 24.00 | 18.00 | 0+560.000                            | 10,567.89 |  |
| 0+580.000                           | 350.124     | 349.844    | 0.28      | 0.00 | 0.00     | 0.00 | 1.53 | 0.00 | 1.20 | 0.90 | 1.00                            | 10.00          | 0.00     | 0.00      | 19.19 | 0.38  | 24.00 | 18.00 | 0+580.000                            | 10,580.17 |  |
| 0+600.000                           | 347.802     | 347.566    | 0.24      | 0.00 | 0.00     | 0.00 | 1.38 | 0.00 | 1.20 | 0.90 | 1.00                            | 10.00          | 0.00     | 0.00      | 29.11 | 0.00  | 24.00 | 18.00 | 0+600.000                            | 10,597.23 |  |
| 0+620.000                           | 345.748     | 345.744    | 0.00      | 0.00 | 0.00     | 0.00 | 0.00 | 0.31 | 1.20 | 0.90 | 1.00                            | 10.00          | 0.00     | 0.00      | 13.86 | 3.13  | 24.00 | 18.00 | 0+620.000                            | 10,593.54 |  |
| 0+640.000                           | 343.407     | 343.560    | 0.00      | 0.15 | 0.00     | 0.00 | 0.00 | 0.51 | 1.07 | 0.90 | 1.00                            | 10.00          | 0.00     | 0.00      | 0.01  | 8.27  | 22.75 | 18.00 | 0+640.000                            | 10,573.39 |  |
| 0+660.000                           | 340.933     | 340.808    | 0.13      | 0.00 | 0.00     | 0.00 | 1.12 | 0.00 | 1.20 | 0.90 | 1.00                            | 10.00          | 0.00     | 0.00      | 11.25 | 5.14  | 22.75 | 18.00 | 0+660.000                            | 10,556.91 |  |
| 0+680.000                           | 338.352     | 338.061    | 0.29      | 0.00 | 0.00     | 0.00 | 2.06 | 0.00 | 1.20 | 0.90 | 1.00                            | 10.00          | 0.00     | 0.00      | 31.64 | 0.00  | 24.00 | 18.00 | 0+680.000                            | 10,560.25 |  |
| 0+700.000                           | 336.243     | 336.010    | 0.23      | 0.00 | 0.00     | 0.00 | 1.31 | 0.00 | 1.20 | 0.90 | 1.00                            | 10.00          | 0.00     | 0.00      | 33.69 | 0.00  | 24.00 | 18.00 | 0+700.000                            | 10,540.82 |  |
| 0+720.000                           | 334.354     | 334.459    | 0.00      | 0.00 | 0.00     | 0.00 | 0.00 | 0.53 | 1.07 | 0.90 | 1.00                            | 10.00          | 0.00     | 0.00      | 13.10 | 5.33  | 22.75 | 18.00 | 0+720.000                            | 10,547.61 |  |
| 0+740.000                           | 332.832     | 332.907    | 0.00      | 0.00 | 0.00     | 0.00 | 0.09 | 0.51 | 1.20 | 0.90 | 1.00                            | 10.00          | 0.00     | 0.00      | 0.95  | 10.45 | 22.75 | 18.00 | 0+740.000                            | 10,575.69 |  |
| 0+760.000                           | 331.780     | 331.480    | 0.28      | 0.00 | 0.00     | 0.00 | 1.64 | 0.00 | 1.20 | 0.90 | 1.00                            | 10.00          | 0.00     | 0.00      | 17.38 | 5.11  | 24.00 | 18.00 | 0+760.000                            | 10,596.82 |  |
| 0+780.000                           | 330.954     | 330.929    | 0.02      | 0.00 | 0.00     | 0.00 | 0.57 | 0.51 | 1.20 | 0.90 | 1.00                            | 10.00          | 0.00     | 0.00      | 22.12 | 5.05  | 24.00 | 18.00 | 0+780.000                            | 10,601.65 |  |
| 0+800.000                           | 331.360     | 331.362    | 0.00      | 0.00 | 0.00     | 0.00 | 0.06 | 0.50 | 1.20 | 0.90 | 1.00                            | 10.00          | 0.00     | 0.00      | 6.33  | 10.03 | 24.00 | 18.00 | 0+800.000                            | 10,599.05 |  |
| 0+820.000                           | 332.028     | 332.331    | 0.00      | 0.39 | 0.00     | 0.00 | 0.00 | 1.58 | 1.07 | 0.90 | 1.00                            | 10.00          | 0.00     | 0.00      | 0.65  | 12.47 | 22.75 | 18.00 | 0+820.000                            | 10,587.44 |  |
| 0+840.000                           | 332.117     | 332.168    | 0.00      | 0.08 | 0.00     | 0.00 | 0.23 | 0.30 | 1.20 | 0.90 | 1.00                            | 10.00          | 0.00     | 0.00      | 2.32  | 18.81 | 22.75 | 18.00 | 0+840.000                            | 10,585.02 |  |
| 0+860.000                           | 331.652     | 331.769    | 0.00      | 0.11 | 0.00     | 0.00 | 0.29 | 0.89 | 1.20 | 0.90 | 1.00                            | 10.00          | 0.00     | 0.00      | 5.24  | 11.90 | 24.00 | 18.00 | 0+860.000                            | 10,608.16 |  |
| 0+880.000                           | 330.459     | 330.535    | 0.00      | 0.08 | 0.00     | 0.00 | 0.11 | 0.47 | 1.20 | 0.90 | 1.00                            | 10.00          | 0.00     | 0.00      | 4.00  | 13.62 | 24.00 | 18.00 | 0+880.000                            | 10,642.64 |  |
| 0+900.000                           | 329.680     | 329.504    | 0.16      | 0.00 | 0.00     | 0.00 | 1.07 | 0.01 | 1.20 | 0.90 | 1.00                            | 10.00          | 0.00     | 0.00      | 11.75 | 4.85  | 24.00 | 18.00 | 0+900.000                            | 10,660.97 |  |
| 0+920.000                           | 329.844     | 329.505    | 0.34      | 0.00 | 0.00     | 0.00 | 1.88 | 0.12 | 1.20 | 0.90 | 1.00                            | 10.00          | 0.00     | 0.00      | 12.80 | 1.30  | 24.00 | 18.00 | 0+905.000                            | 0.00      |  |
| 0+940.000                           | 330.397     | 330.306    | 0.09      | 0.00 | 0.00     | 0.00 | 0.35 | 0.00 | 1.20 | 0.90 | 1.00                            | 10.00          | 0.00     | 0.00      | 8.45  | 1.16  | 24.00 | 18.00 | 0+760.000                            | 10,596.82 |  |
| 0+960.000                           | 331.192     | 331.162    | 0.03      | 0.00 | 0.00     | 0.00 | 0.43 | 0.29 | 1.20 | 0.90 | 1.00                            | 10.00          | 0.00     | 0.00      | 7.75  | 2.93  | 24.00 | 18.00 | 0+780.000                            | 10,601.65 |  |
| 0+980.000                           | 331.988     | 332.016    | 0.00      | 0.00 | 0.00     | 0.00 | 0.00 | 0.40 | 1.20 | 0.90 | 1.00                            | 10.00          | 0.00     | 0.00      | 4.30  | 6.50  | 24.00 | 18.00 | 0+800.000                            | 10,599.05 |  |
| 1+000.000                           | 331.551     | 331.693    | 0.00      | 0.14 | 0.00     | 0.00 | 0.00 | 0.77 | 1.07 | 0.90 | 1.00                            | 10.00          | 0.00     | 0.00      | 0.02  | 11.46 | 22.75 | 18.00 | 0+820.000                            | 10,587.44 |  |
| 1+020.000                           | 330.710     | 330.602    | 0.11      | 0.00 | 0.00     | 0.00 | 0.56 | 0.04 | 1.20 | 0.90 | 1.00                            | 10.00          | 0.00     | 0.00      | 5.64  | 8.07  | 22.75 | 18.00 | 0+840.000                            | 10,585.02 |  |
| 1+040.000                           | 331.807     | 331.384    | 0.42      | 0.00 | 0.00     | 0.00 | 1.89 | 0.00 | 1.19 | 0.89 | 1.00                            | 10.00          | 0.00     | 0.00      | 4.65  | 0.40  | 23.89 | 17.92 | 0+905.000                            | 0.00      |  |
| 1+060.000                           | 334.164     | 333.923    | 0.24      | 0.00 | 0.00     | 0.00 | 1.46 | 0.00 | 1.20 | 0.90 | 1.00                            | 10.00          | 0.00     | 0.00      | 3.24  | 0.00  | 23.89 | 17.92 | 0+780.000                            | 10,596.82 |  |
| 1+080.000                           | 336.727     | 336.667    | 0.06      | 0.00 | 0.00     | 0.00 | 0.38 | 0.00 | 1.20 | 0.90 | 1.00                            | 10.00          | 0.00     | 0.00      | 10.48 | 0.00  | 24.00 | 18.00 | 0+780.000                            | 10,601.65 |  |
| 1+085.000                           | 336.727     | 336.667    | 0.06      | 0.00 | 0.00     | 0.00 | 0.38 | 0.00 | 1.20 | 0.90 | 1.00                            | 10.00          |          |           |       |       |       |       |                                      |           |  |

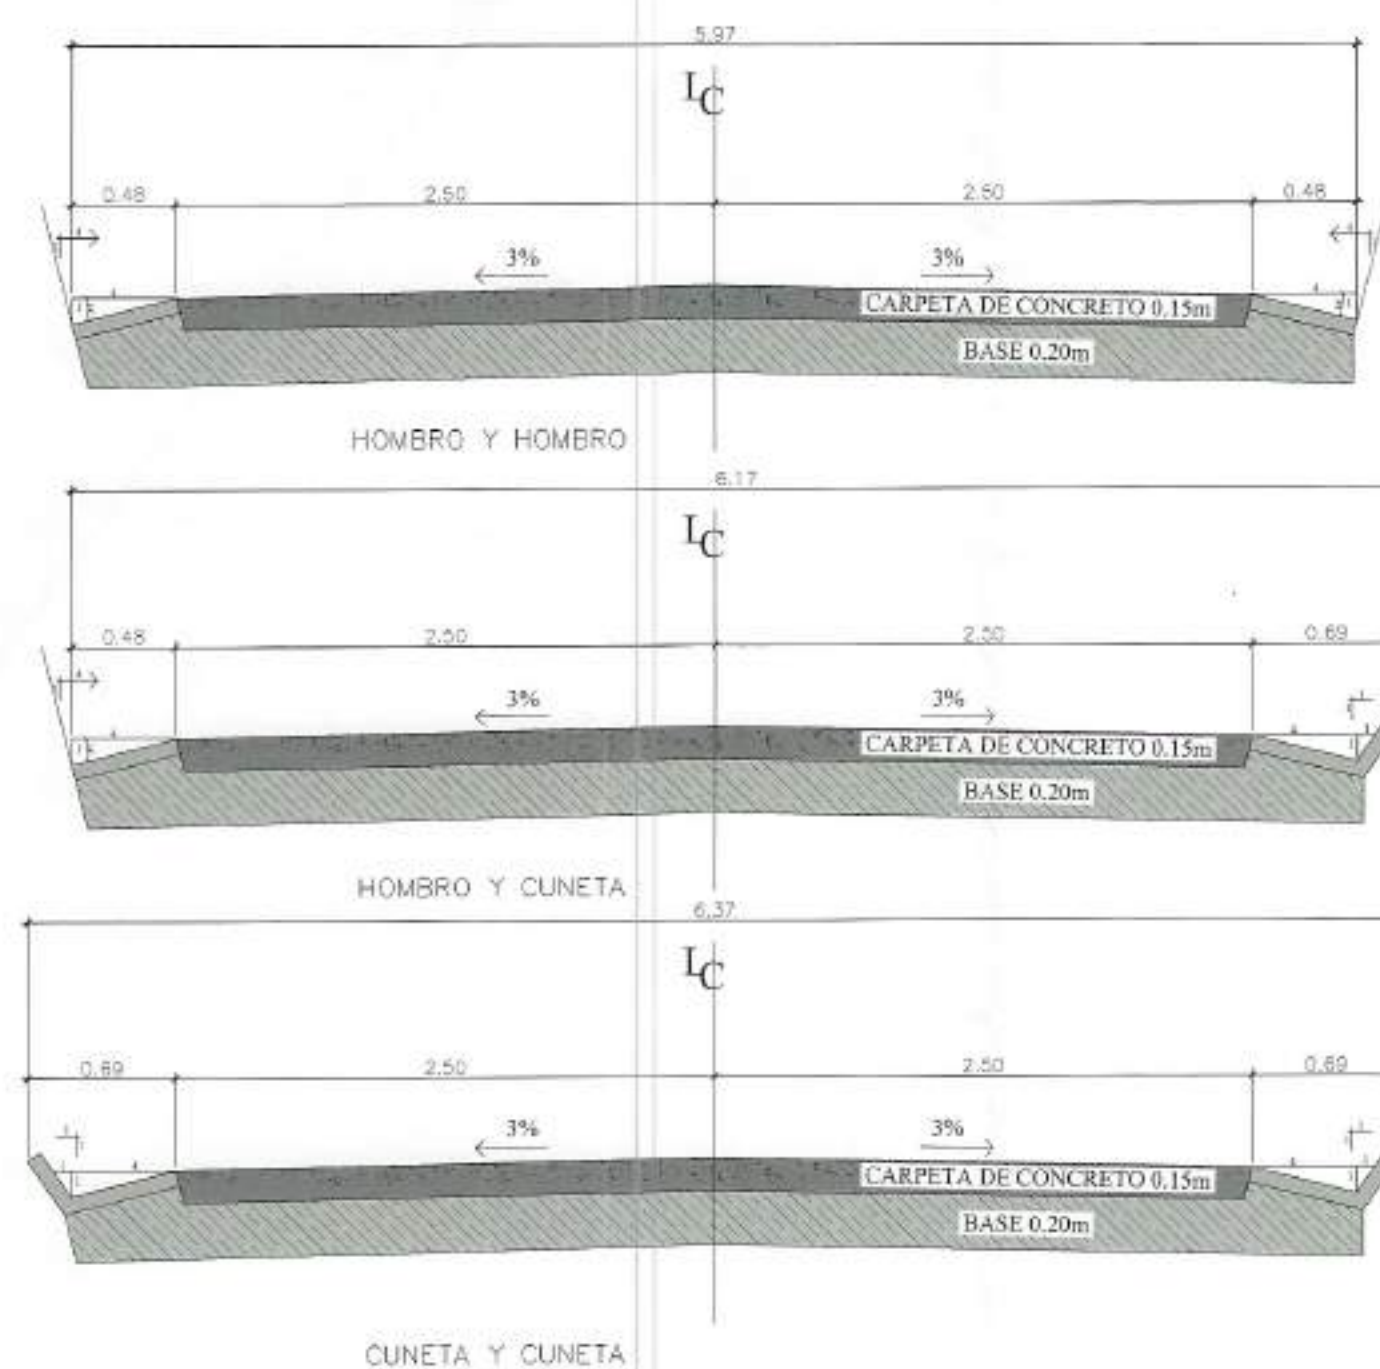


SECCIONES TÍPICAS DE CARRILES

ESCALA 1/35

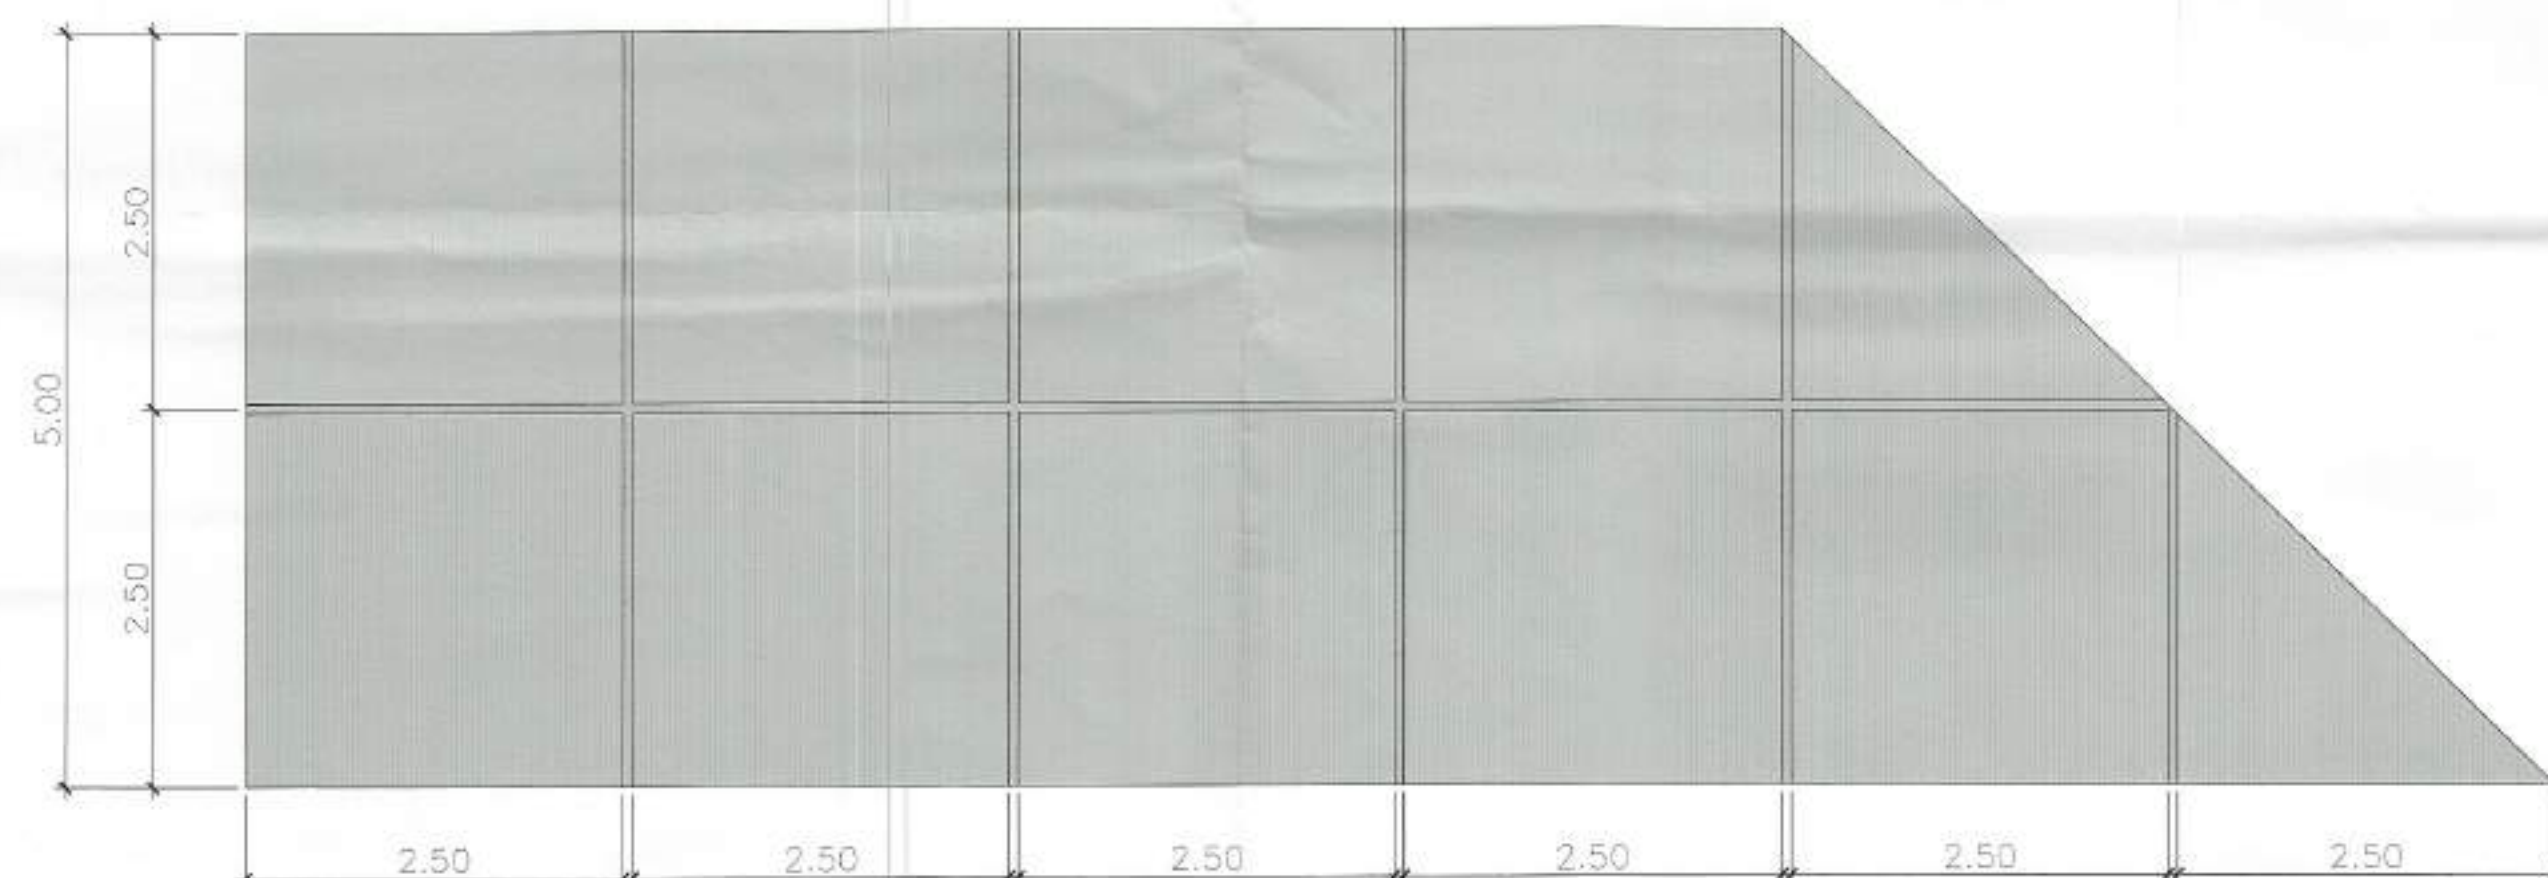


DETALLE SEPARACIÓN DE JUNTAS

ESCALA 1/50

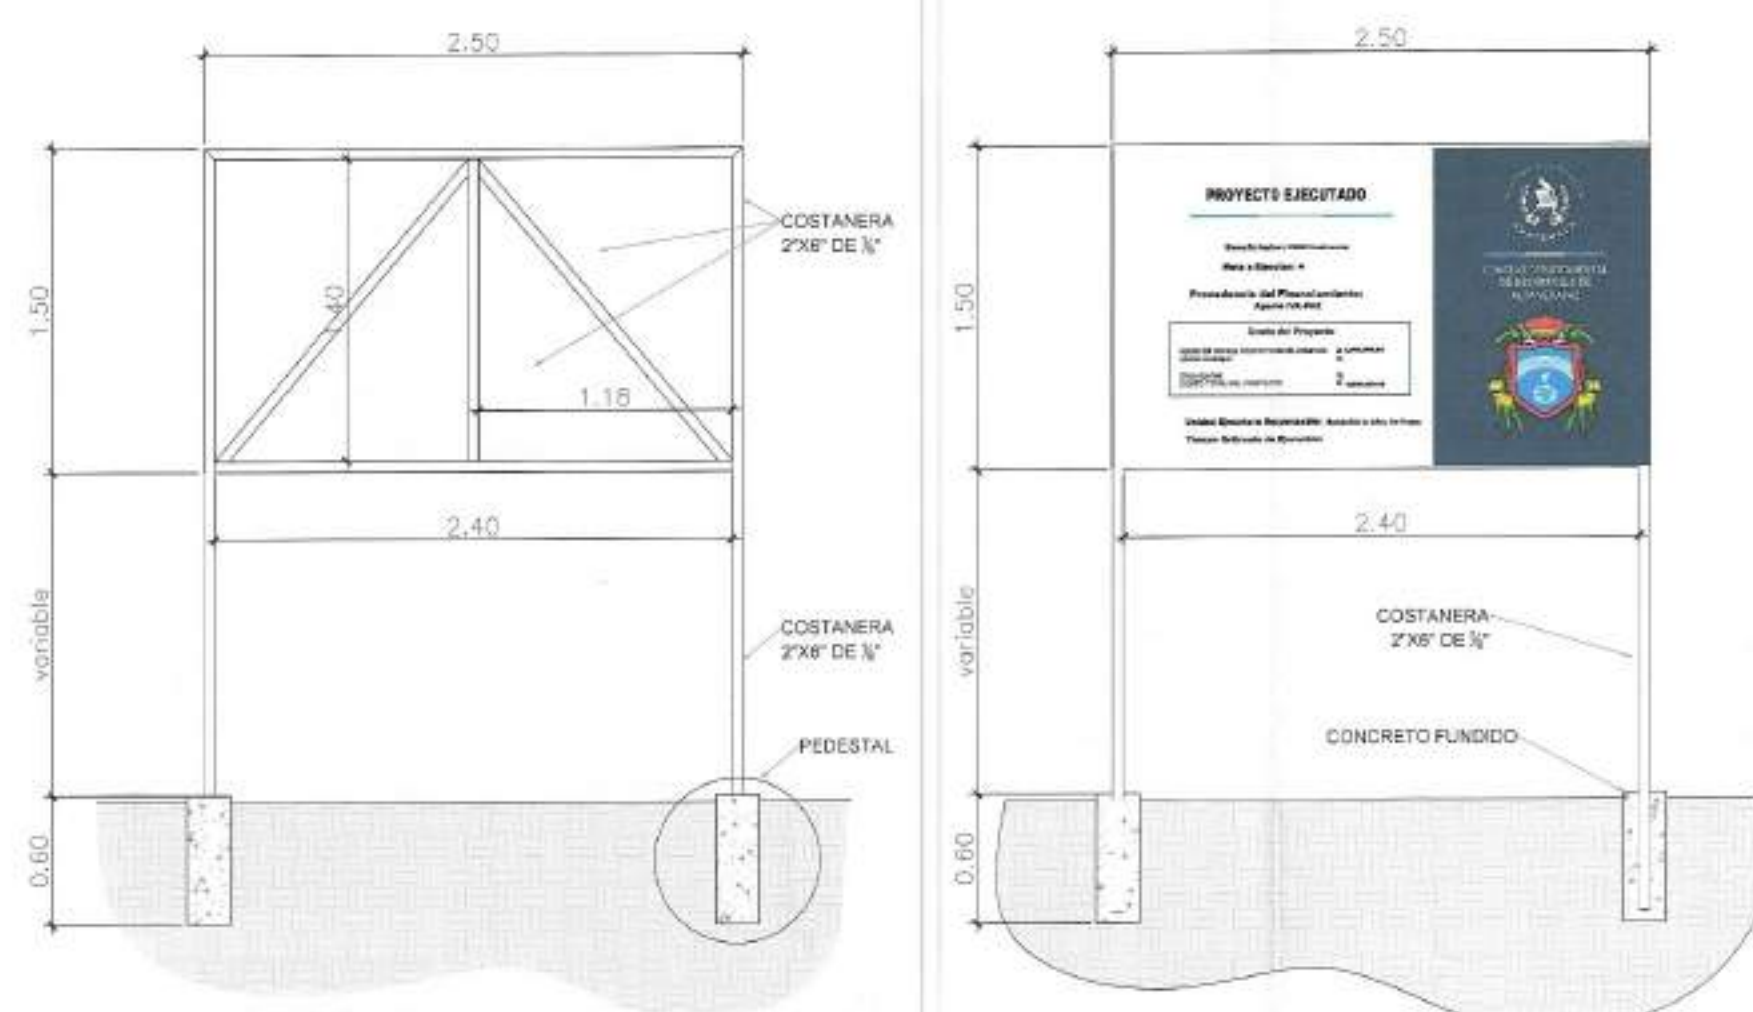

DETALLE ROTULO DE PROYECTO

ESCALA 1/35

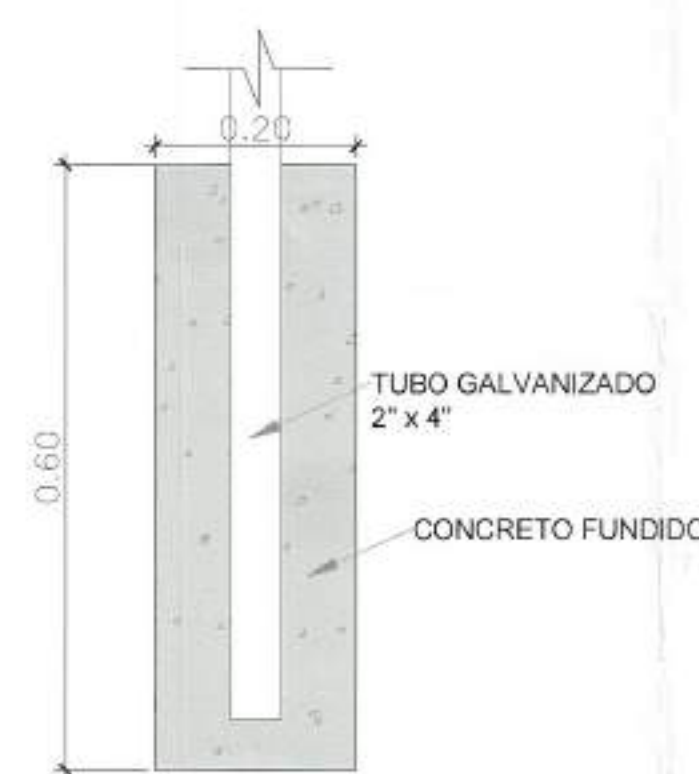


SECCION

PLANTA

DETALLE PEDESTAL DEL ROTULO DE PROYECTO

ESCALA 1/7.5

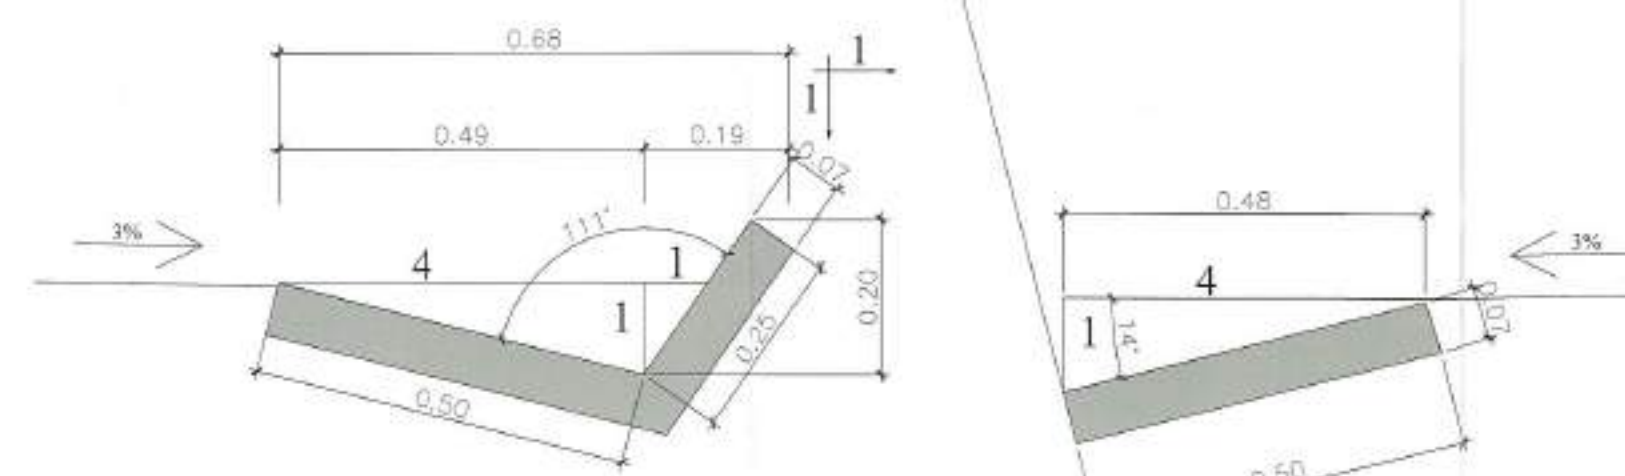


DETALLE DE CUNETA Y HOMBRO

ESCALA 1/10



DETALLES DE SEÑALIZACIÓN HORIZONTAL


ESCALA 1/65

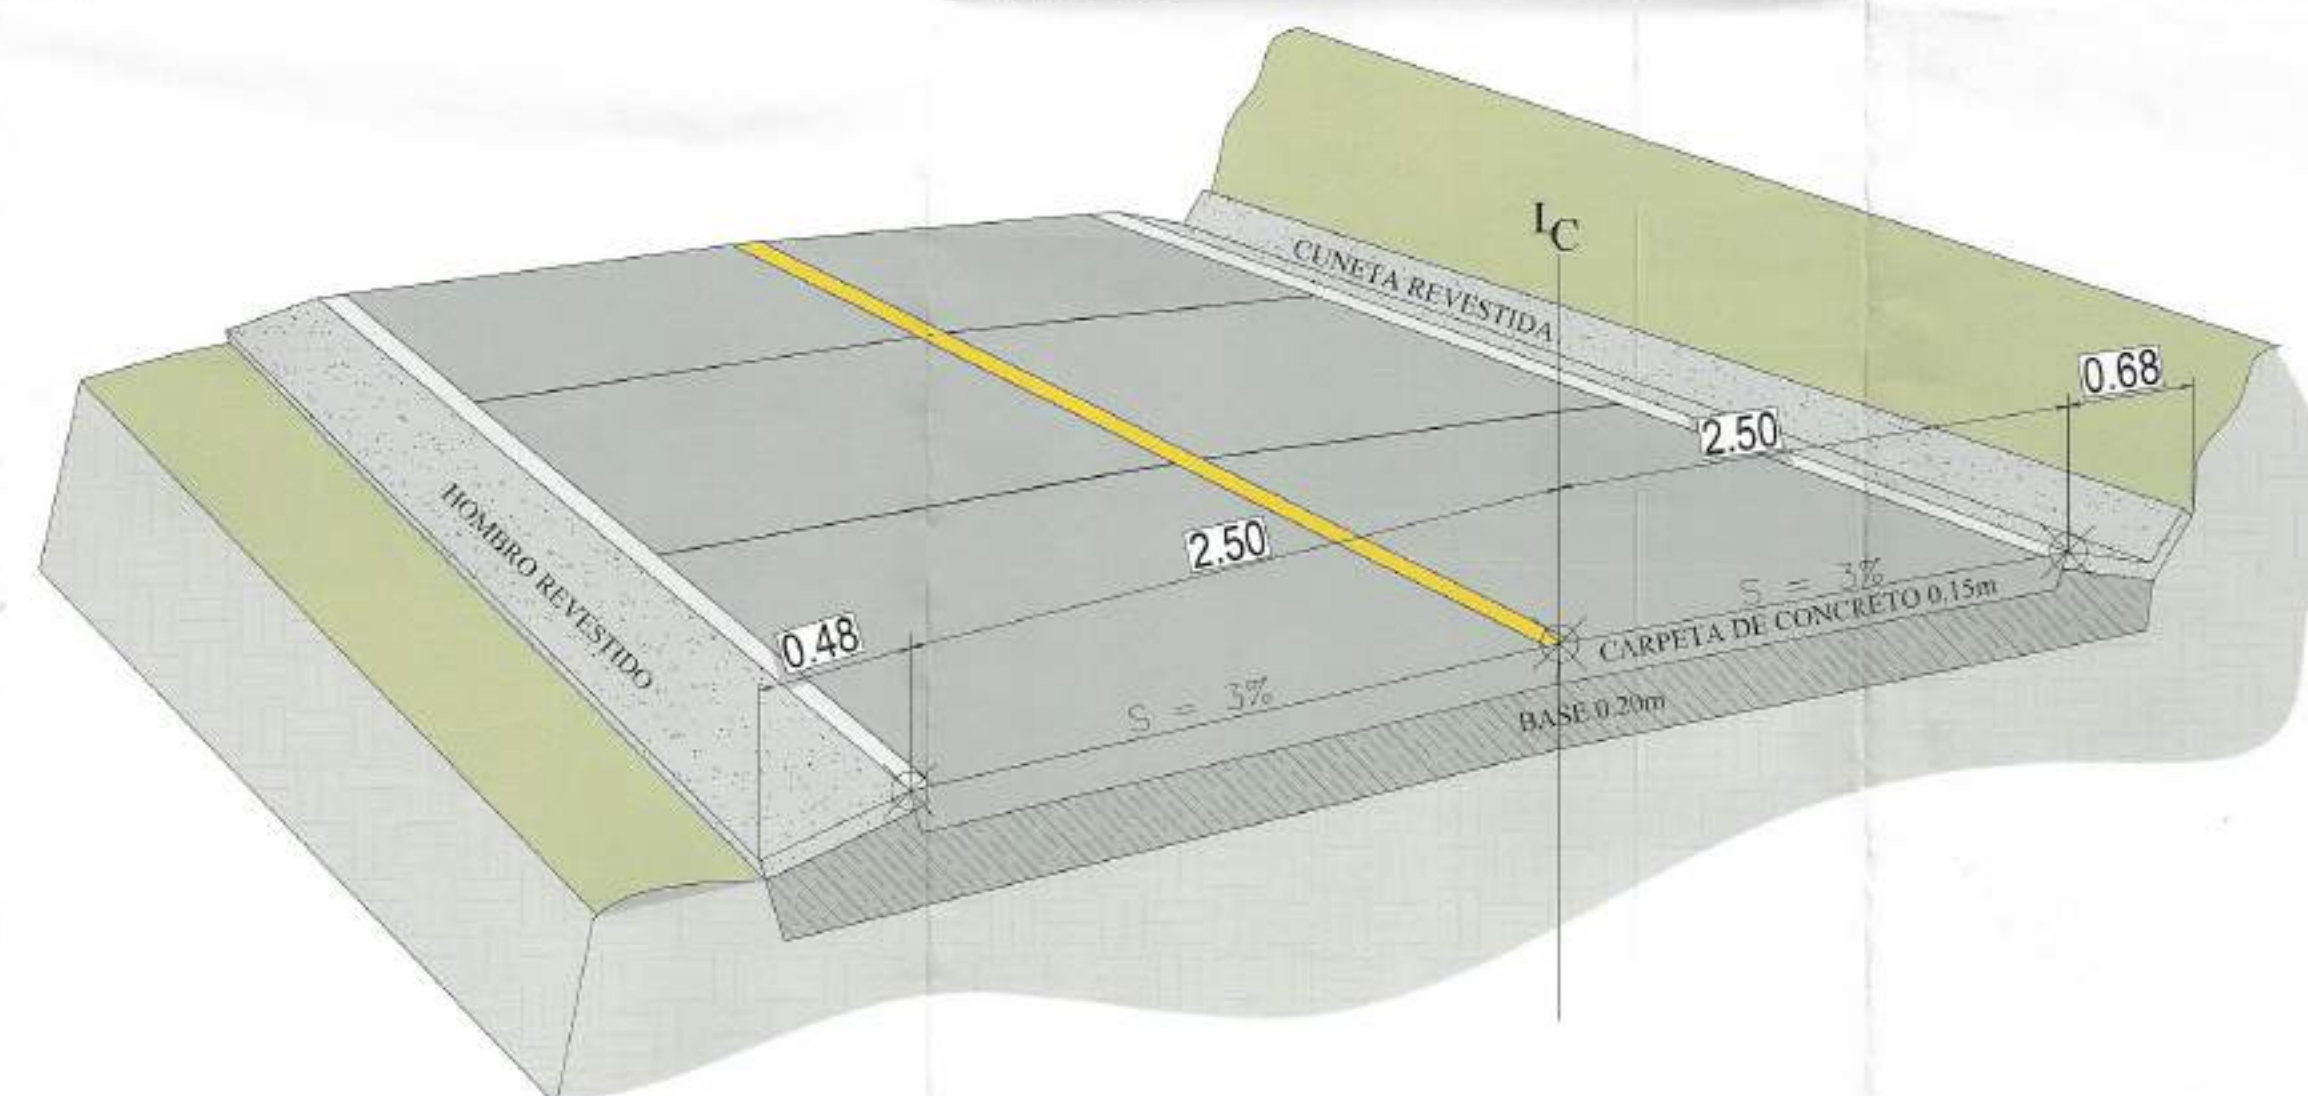

ISOMETRICO DE SECCION TIPICA

ESCALA 1/30

JUNTA LONGITUDINAL  
PROFUNDIDAD DE CORTE: 0.05 M  
RELLENO Y SELLO: MATERIAL ELASTOMERICO NORMA ACI 504-R

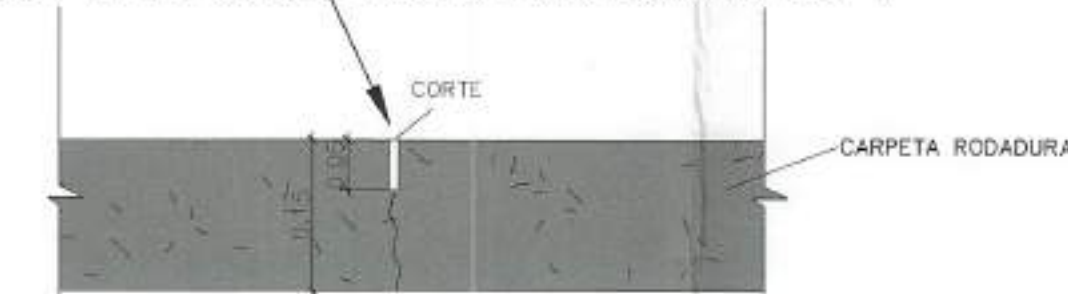

SECCION TIPICA JUNTA LONGITUDINAL

ESCALA 1/7.5



ADMINISTRACION  
2024 - 2028

MUNICIPALIDAD DE  
COBAN, A.V.  
Dirección de Perfilación y  
Elaboración de proyectos

PROYECTO:  
MEJORAMIENTO CAMINO RURAL  
(PAVIMENTO RIGIDO) DEL CASERIO LA  
SULTANA HACIA EL CASERIO ROCJA TZIN,  
COBAN, ALTA VERAPAZ

No. SNIP:

353493

UBICACIÓN:  
CASERIO LA SULTANA,  
COBAN ALTA VERAPAZ


CONTIENE:  
-DETALLES DE SECCION  
TIPICA  
-DETALLES DE SEÑALIZACION  
HORIZONTAL  
-DETALLES DE ROTULO DE  
PROYECTO

DISEÑO:  
DIRECCIÓN DE PERFILACION Y  
ELABORACIÓN DE PROYECTOS

DIBUJO:  
DIRECCIÓN DE PERFILACION Y  
ELABORACIÓN DE PROYECTOS

CALCULO:  
DIRECCIÓN DE PERFILACION Y  
ELABORACIÓN DE PROYECTOS

Vo. Bo.:

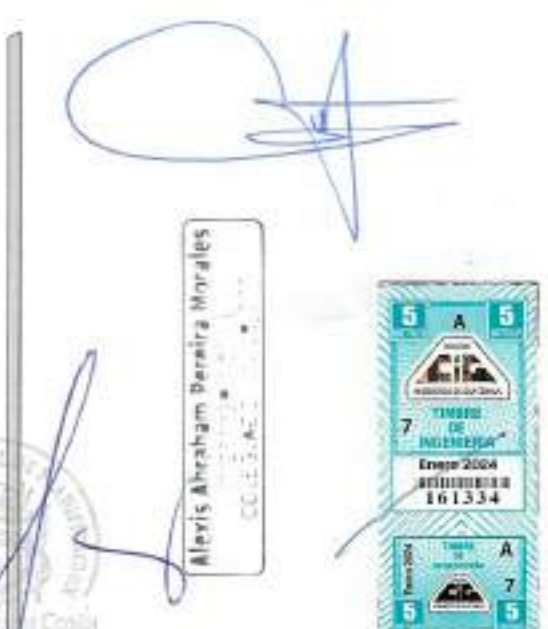

ARQ. E. T. INS.






MAGNITUD:  
1 085 M².

HOJA A-1

FECHA:  
SEPTIEMBRE - 2025

ESCALA:  
INDICADA

10  
11

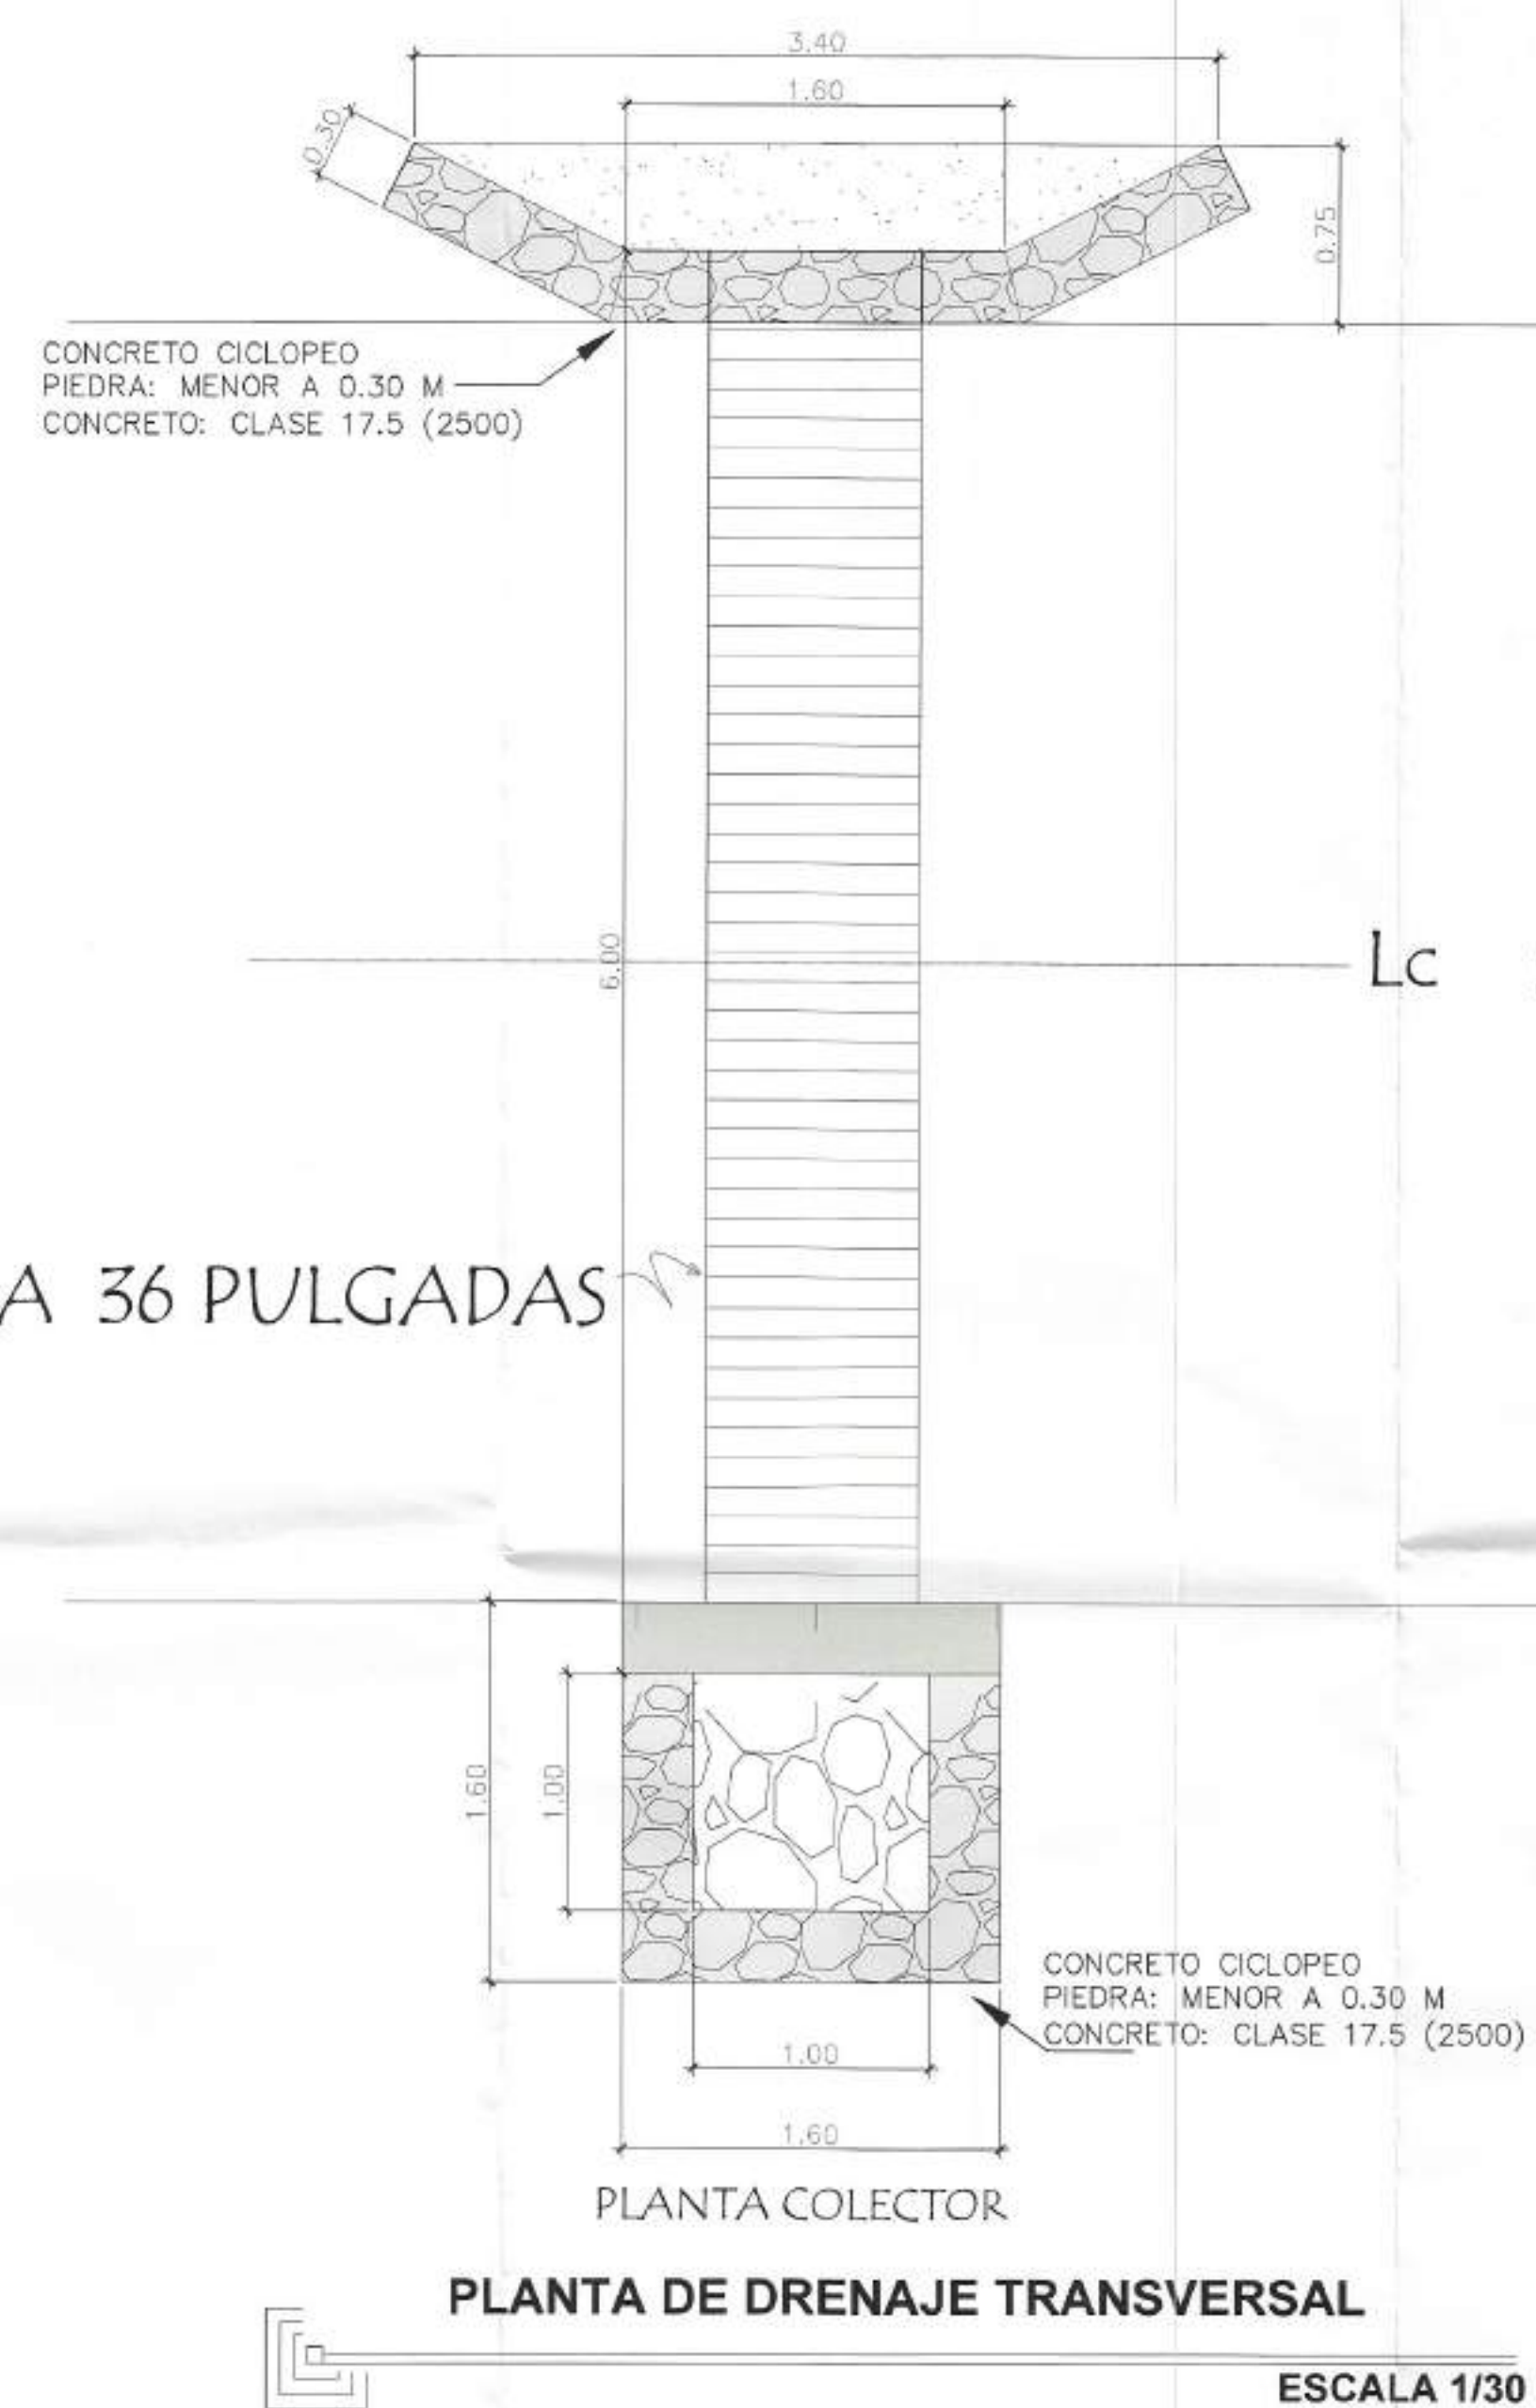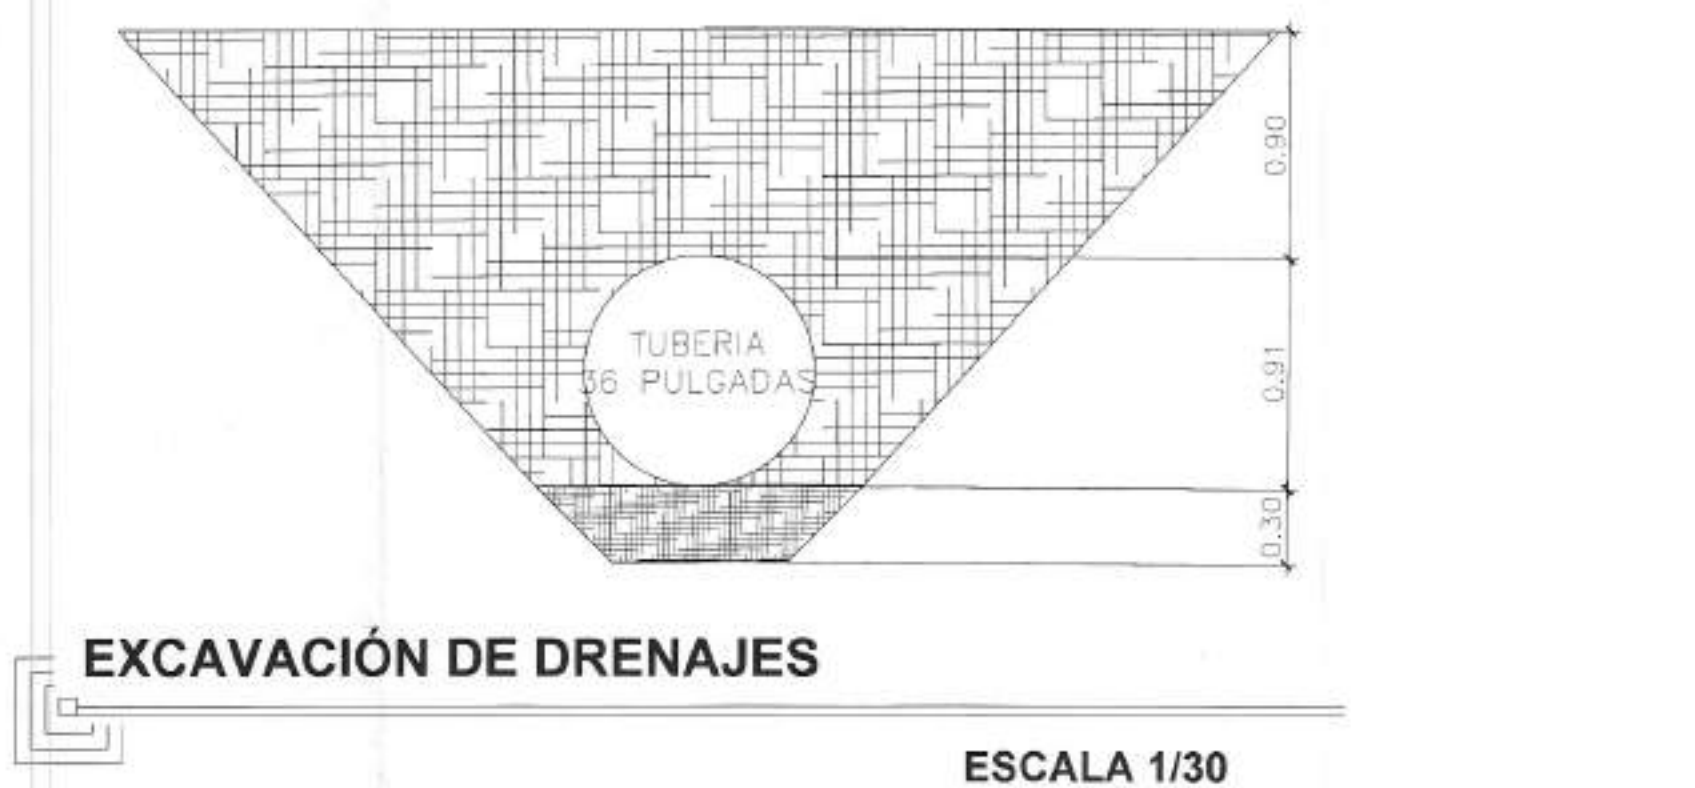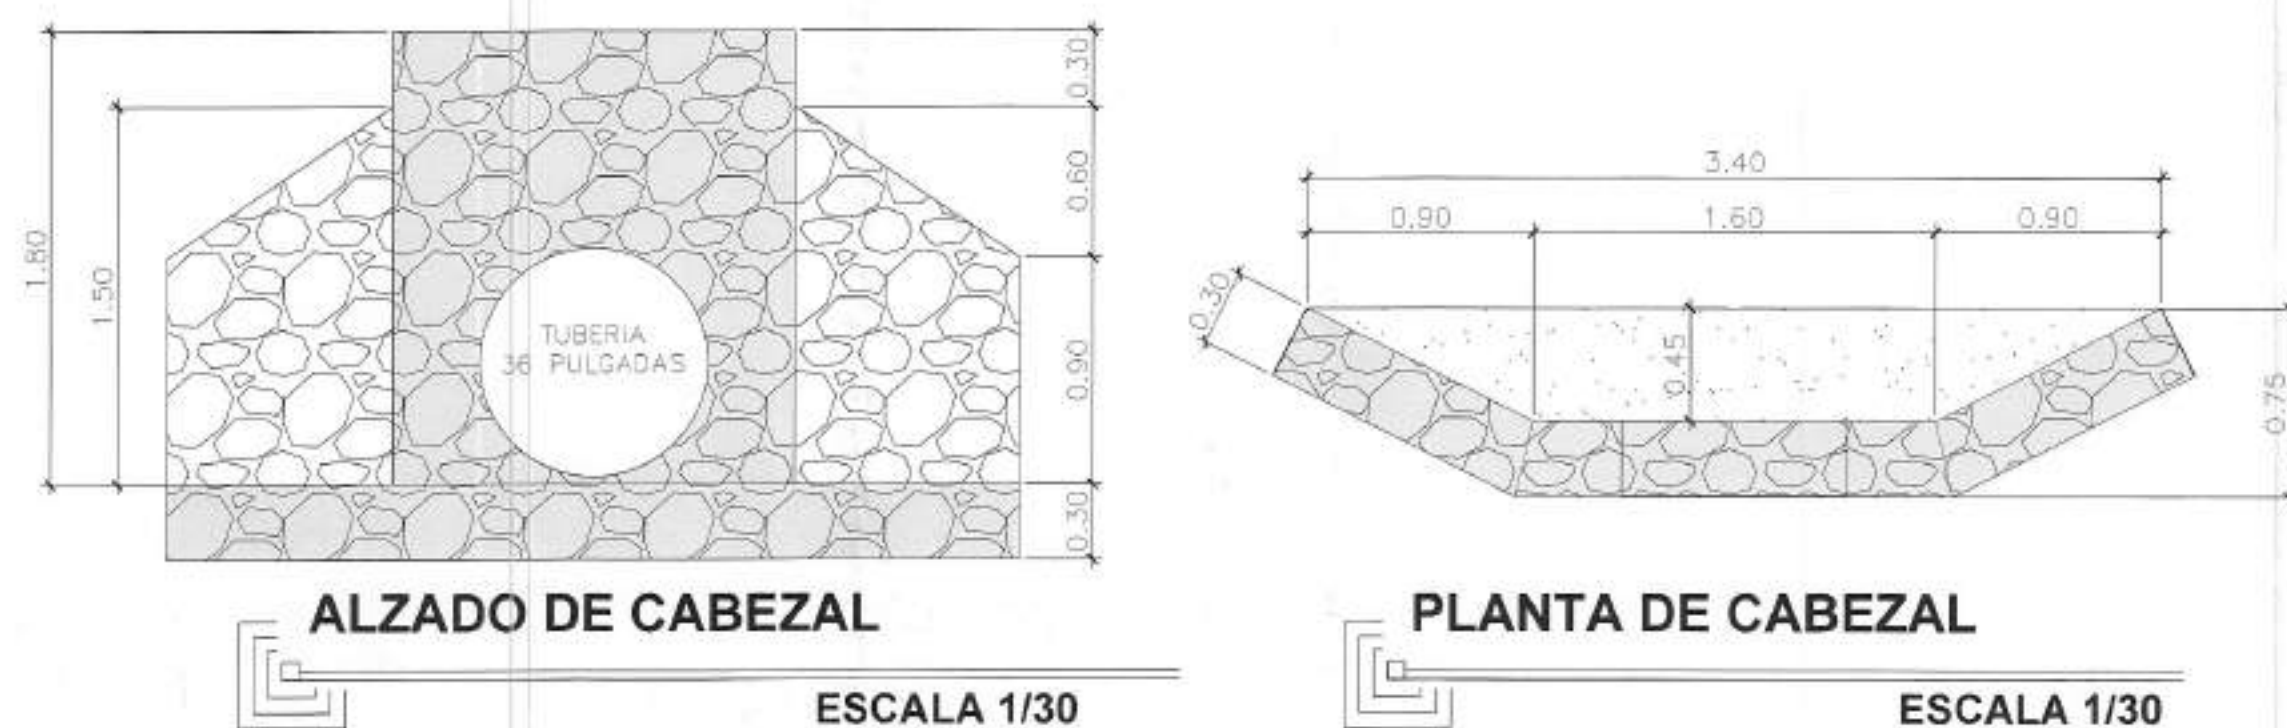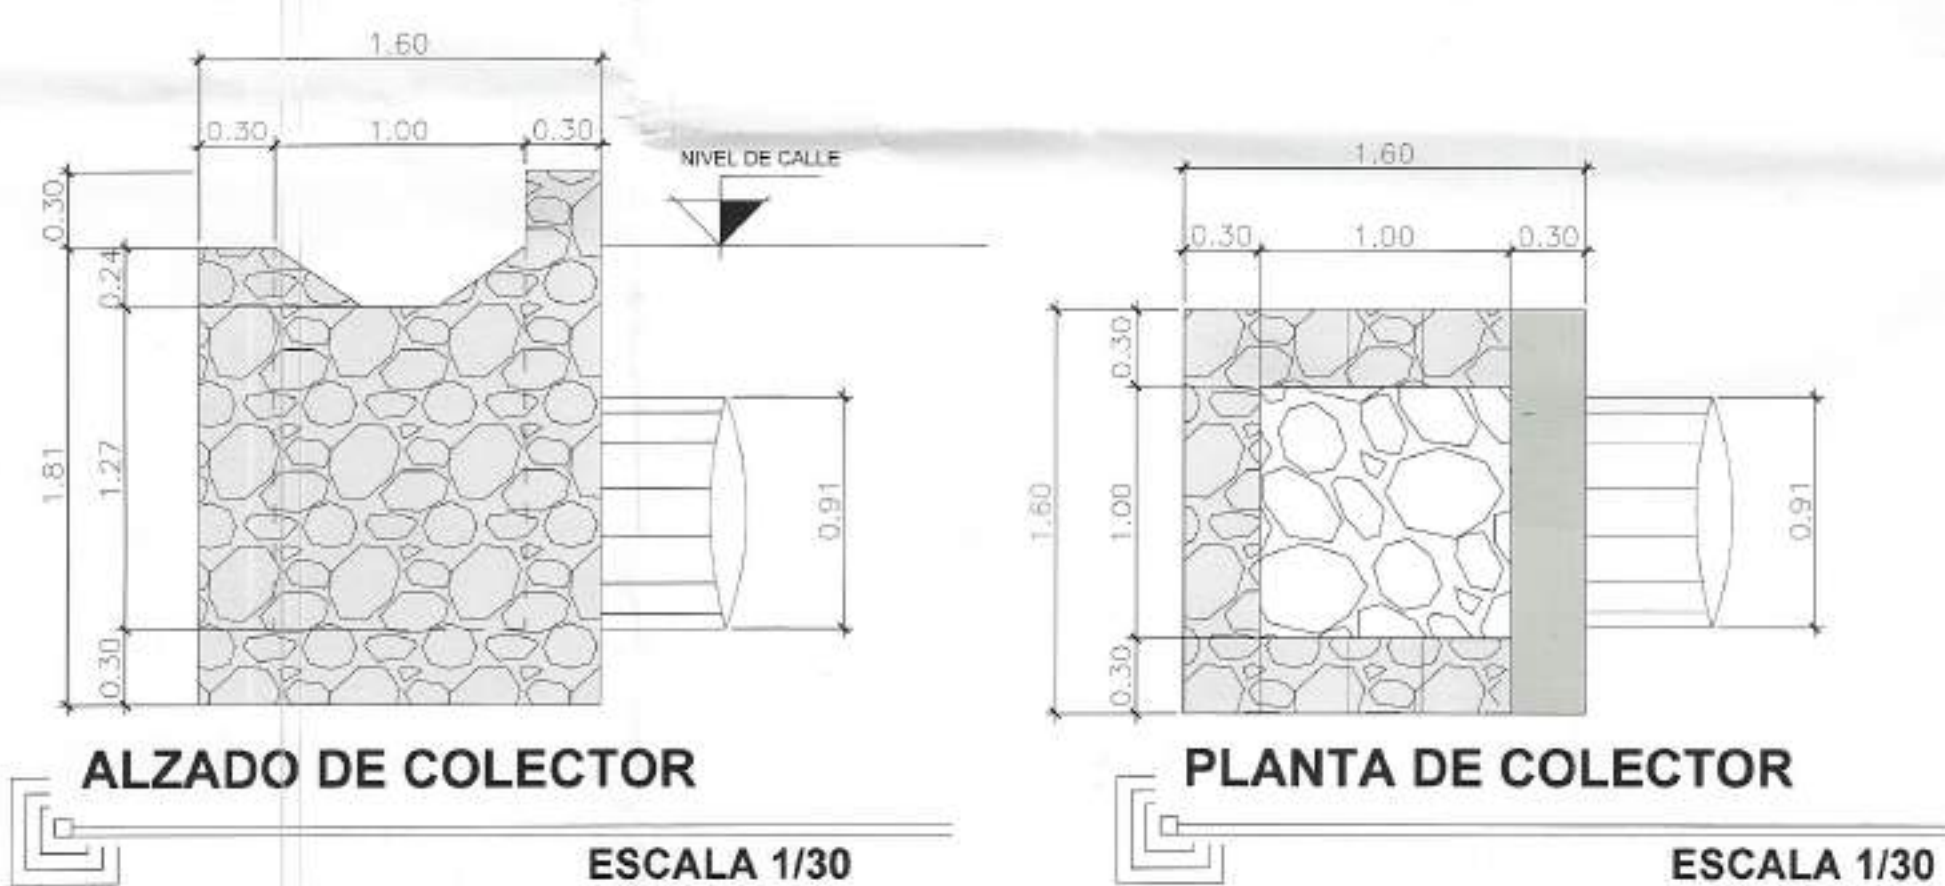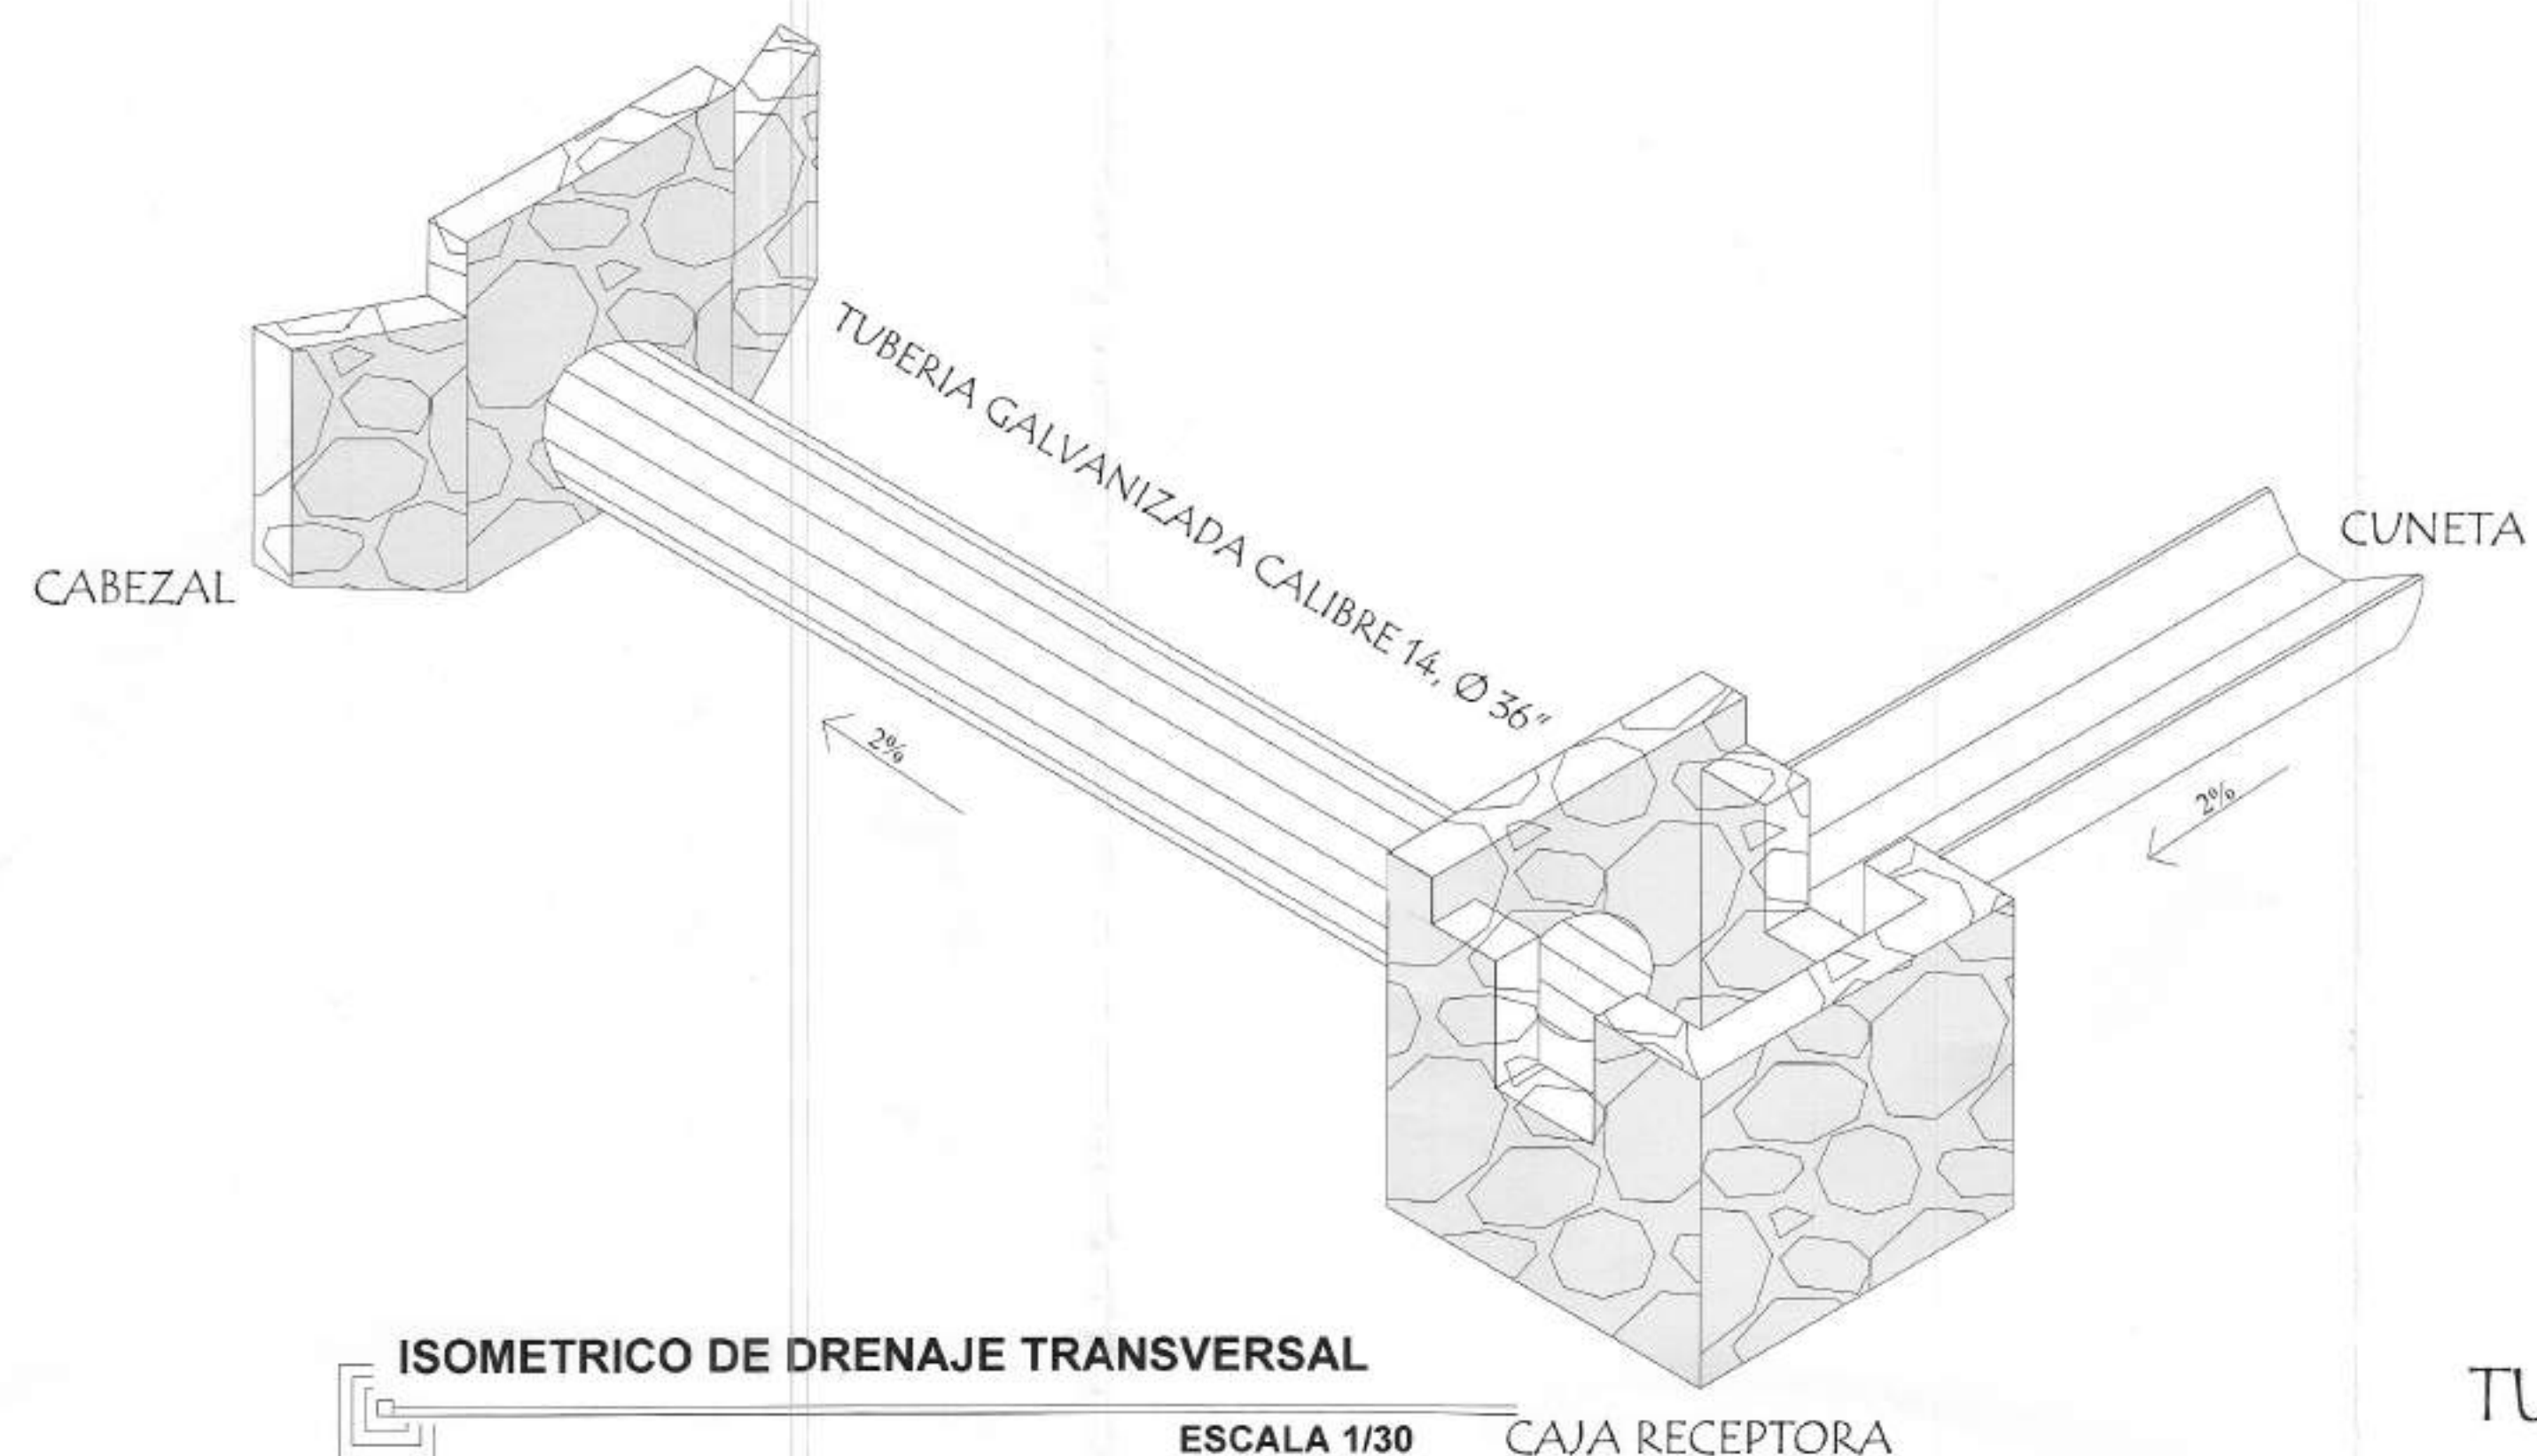

ADMINISTRACION  
2024 - 2028

MUNICIPALIDAD DE  
COBAN, A.V.  
Dirección de Perfilación y  
Elaboración de proyectos

PROYECTO:  
MEJORAMIENTO CAMINO RURAL  
(PAVIMENTO RIGIDO) DEL CASERIO LA  
SULTANA HACIA EL CASERIO ROCJA TZIN,  
COBAN, ALTA VERAPAZ

No. SNIP:

353493

UBICACIÓN:

CASERIO LA SULTANA,  
COBAN ALTA VERAPAZ

CONTIENE:

DETALLES DE  
DRENAJES  
TRANSVERSALES

DISEÑO:

DIRECCIÓN DE PERFILACION Y  
ELABORACIÓN DE PROYECTOS

DIBUJO:

DIRECCIÓN DE PERFILACION Y  
ELABORACIÓN DE PROYECTOS

CALCULO:

DIRECCIÓN DE PERFILACION Y  
ELABORACIÓN DE PROYECTOS

Vo. Bo.:



MAGNITUD:  
1 085 MP.

FECHA:  
SEPTIEMBRE - 2025

ESCALA:  
INDICADA

HOJA A-1

11  
11