


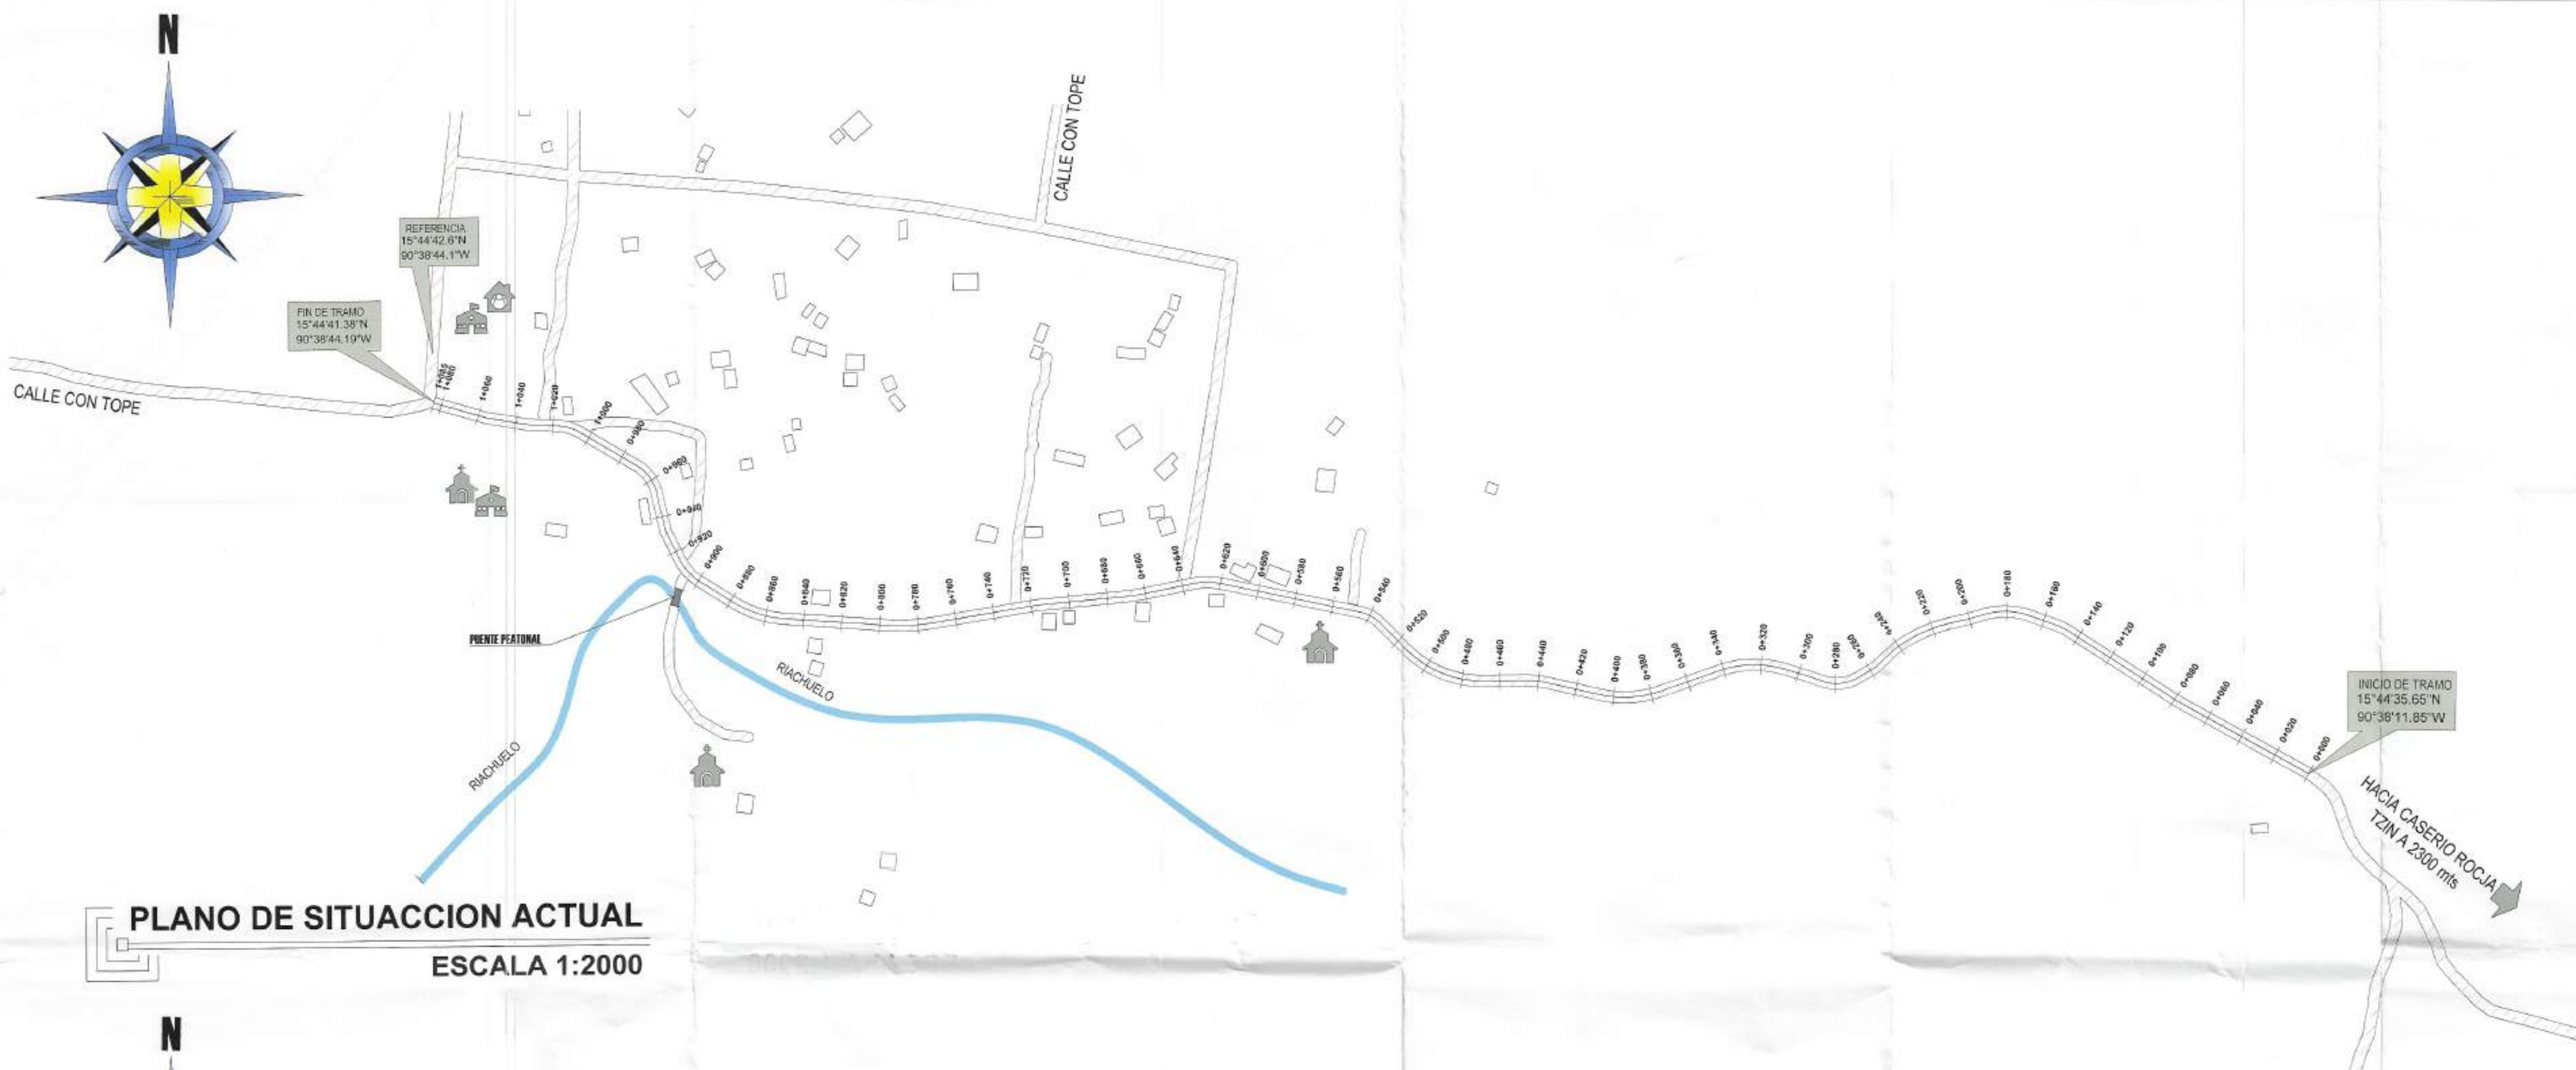

PLANO DE SITUACION ACTUAL
ESCALA 1:2000



PLANO DE SITUACION FUTURA
ESCALA 1:2000

NOMENCLATURA	
PAVIMENTO RIGIDO	
TERRACERIA	
CONSTRUCCIONES Y VIVIENDAS	
TRANSVERSAL TUBERIA DE 36"	
CUNETAS EN PLANTA	
HOMBRO EN PLANTA	
IGLESIA	
ESCUELA	
SALON COMUNAL	



ADMINISTRACION
2024 - 2028

MUNICIPALIDAD DE
COBAN, A.V.
Dirección de Perfilación y
Elaboración de proyectos

PROYECTO:
MEJORAMIENTO CAMINO RURAL
(PAVIMENTO RIGIDO) DEL CASERIO LA
SULTANA HACIA EL CASERIO ROCJA TZIN,
COBAN, ALTA VERAPAZ

No. SNIP:
353493

UBICACIÓN:
CASERIO LA SULTANA,
COBAN ALTA VERAPAZ

CONTIENE:
**PLANO DE SITUACION
ACTUAL Y FUTURA**

DISEÑO:
DIRECCIÓN DE PERFILACION Y
ELABORACIÓN DE PROYECTOS

DIBUJO:
DIRECCIÓN DE PERFILACION Y
ELABORACIÓN DE PROYECTOS

CALCULO:
DIRECCIÓN DE PERFILACION Y
ELABORACIÓN DE PROYECTOS

Vo. Bo.:

Alexis Abraham Perera
INGENIERO
COLEGIADO N.º 18



MAGNITUD:
1:085 M.P.
FECHA:
SEPTIEMBRE - 2025
ESCALA:
INDICADA

HOJA A-1
01
01