


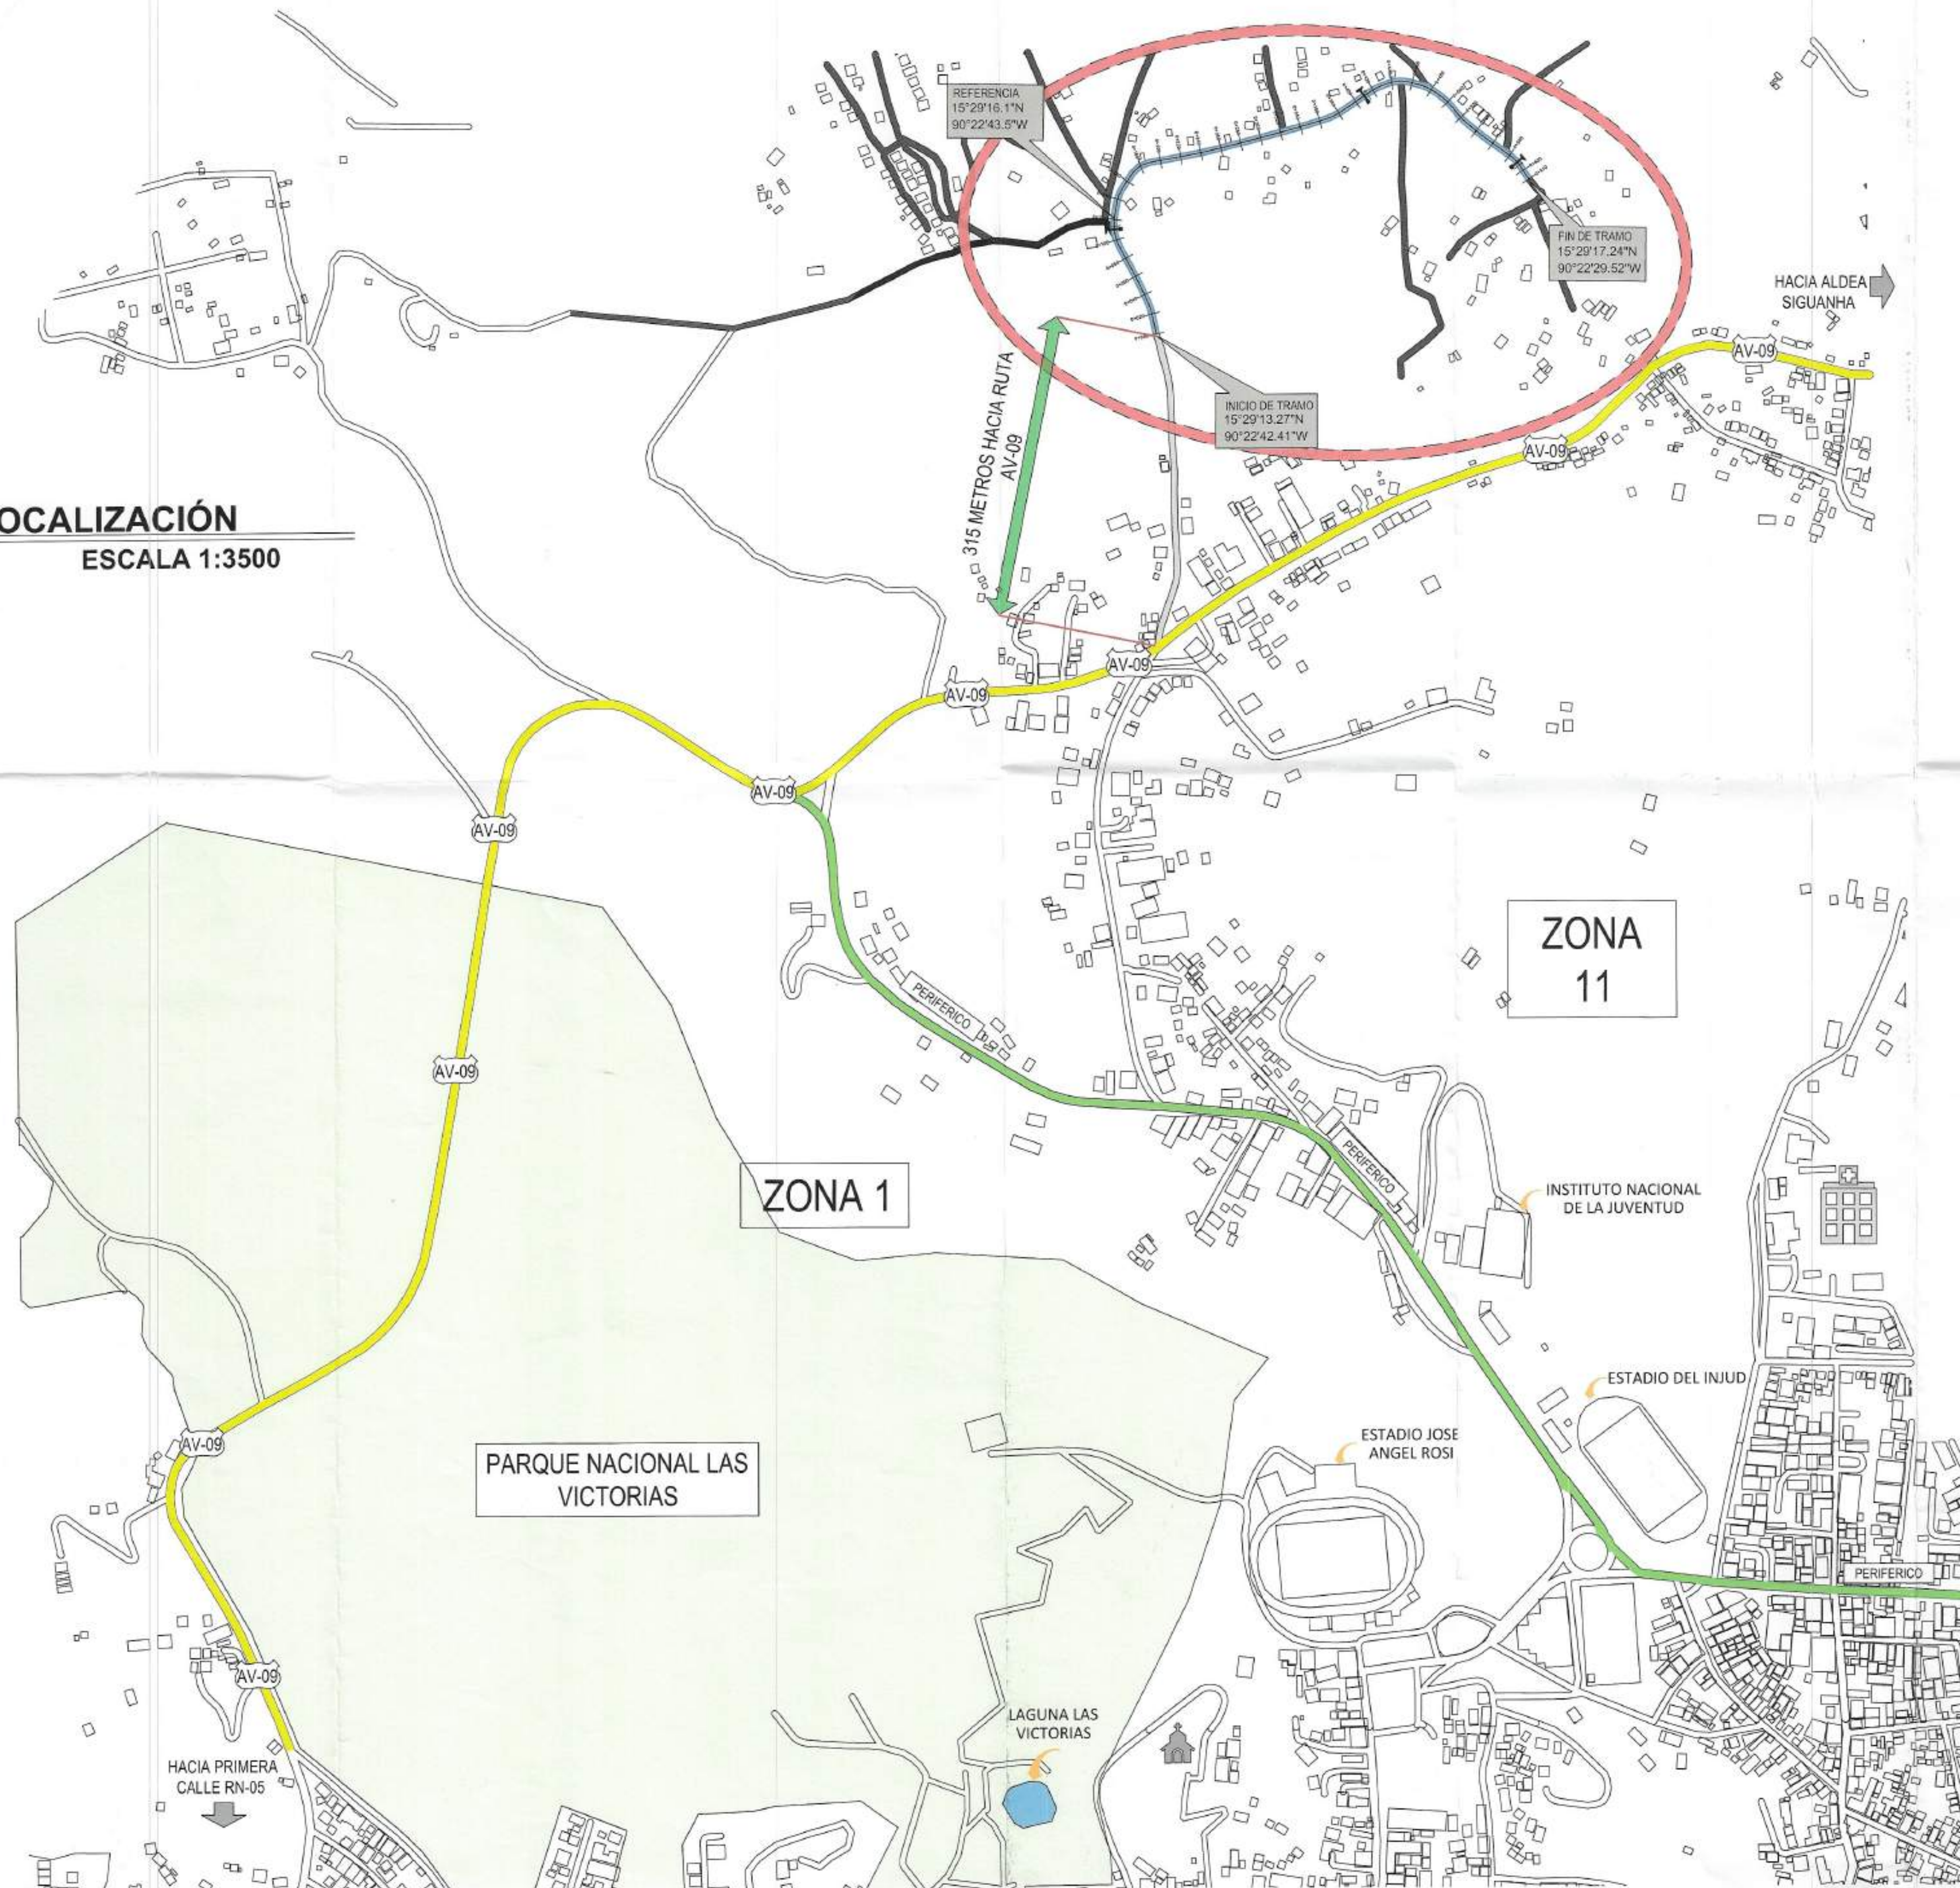

PLANO DE LOCALIZACIÓN

ESCALA 1:3500

NOMENCLATURA	
PAVIMENTO RÍGIDO	
TERRACERIA	
CONSTRUCCIONES Y VIVIENDAS	
TRANSVERSAL TUBERIA DE 36"	
BORDILLO	
IGLESIA	
ESCUELA	
HOSPITAL REGIONAL DE COBAN	



ADMINISTRACION
2024 - 2028

MUNICIPALIDAD DE
COBAN, A.V.
Dirección de Perfilación y
Elaboración de proyectos

PROYECTO:
MEJORAMIENTO CAMINO RURAL
(PAVIMENTO RIGIDO) CASERIO GUALOM
SAXYANTZUUL, COBAN, ALTA VERAPAZ

No. SNIP:

353086

UBICACIÓN:

CASERIO GUALOM SAXYANTZUUL
COBAN ALTA VERAPAZ

CONTIENE:

PLANO DE
LOCALIZACIÓN

DISEÑO:

DIRECCIÓN DE PERFILACION Y
ELABORACIÓN DE PROYECTOS

DIBUJO:

DIRECCIÓN DE PERFILACION Y
ELABORACIÓN DE PROYECTOS

CALCULO:

DIRECCIÓN DE PERFILACION Y
ELABORACIÓN DE PROYECTOS

Vo. Bo.:

ALCALDIA MUNICIPAL DE COBAN
MUNICIPALIDAD DE COBAN
COBAN, ALTA VERAPAZ

Alexis Abraham
INGENIERO
COLEGIADO

MAGNITUD:

610 M.

HOJA A-1

FECHA:
AGOSTO - 2025

01

ESCALA:
INDICADA

10



PLANO DE UBICACIÓN

ESCALA 1:1250

NOMENCLATURA	
PAVIMENTO RÍGIDO	
TERRACERIA	
CONSTRUCCIONES Y VIVIENDAS	
TRANSVERSAL TUBERIA DE 36"	
BORDILLO	
IGLESIA	
ESCUELA	
HOSPITAL REGIONAL DE COBAN	

TRAMO PAVIMENTADO



ADMINISTRACION
2024 - 2028

MUNICIPALIDAD DE
COBAN, A.V.
Dirección de Perfilación y
Elaboración de proyectos

PROYECTO:
MEJORAMIENTO CAMINO RURAL
(PAVIMENTO RIGIDO) CASERIO GUALOM
SAXYANTZUUL, COBAN, ALTA VERAPAZ

No. SNIP:

353086

UBICACIÓN:
CASERIO GUALOM SAXYANTZUUL,
COBAN ALTA VERAPAZ

CONTIENE:
PLANO DE UBICACIÓN

DISEÑO:
DIRECCIÓN DE PERFILACION Y
ELABORACIÓN DE PROYECTOS

DIBUJO:
DIRECCIÓN DE PERFILACION Y
ELABORACIÓN DE PROYECTOS

CALCULO:
DIRECCIÓN DE PERFILACION Y
ELABORACIÓN DE PROYECTOS

Vo. Bo.:




Alexis Abraham Perera Morán
INGENIERO CIVIL
COLEGIADO No. 18.97

ARQ EST INS

MAGNITUD: 610 M. HOJA A-1

FECHA: AGOSTO - 2025 02/10

ESCALA: INDICADA

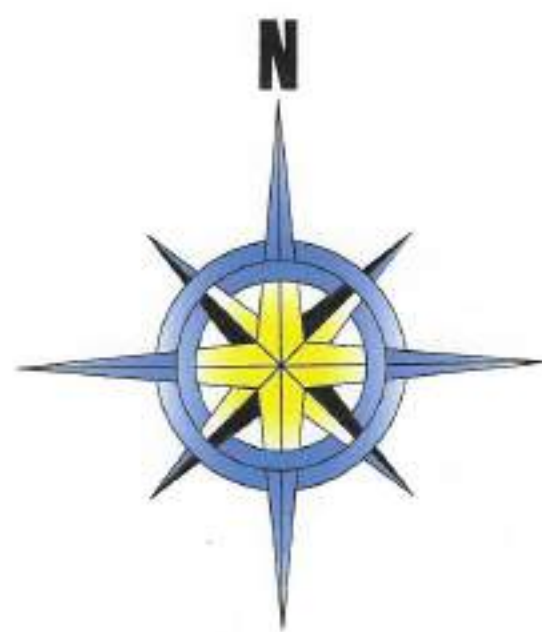

PLANTA DE CURVAS DE NIVEL

ESCALA 1:650

SIMBOLOGIA	DESCRIPCIÓN
	Estacionamiento
	Pendiente en perfil
	Caminamiento en planta
	Curva de nivel
	Cota del terreno
	Curva Horizontal
	Curva Vertical
	PRINCIPIO DE CURVA HORIZONTAL
	PRINCIPIO DE TANGENTE HORIZONTAL
	tubería en planta, Caja cabezal en entrada y muro cabezal en salida
	Indica Bordillo

No.	ESPECIFICACIONES
1	ANCHO DE RODADURA = 5.00 METROS
2	CAPA DE MATERIAL BASE GRANULAR DE 0.20 M. COMPACTADO COMO MÍNIMO AL 95 %. CBR NO MENOR AL 70 %.
3	ANTES DE COLOCAR LA CAPA DE BASE, DEBERÁ CONFORMARSE Y ESCARIFICARSE LA SUB-RASANTE CON PATÍOOL DE ACUERDO A PLANOS.
4	EL MATERIAL DE BASE DEBERÁ SER DE TAMAÑO UNIFORME Y LIBRE DE RESIDUOS DE MADERA, RAÍCES O CUALQUIER OTRO MATERIAL EXTRAÑO.
5	EL TAMAÑO MÁXIMO DEL AGREGADO GRUESO DEL MATERIAL DE BASE NO DEBERÁ SER MAYOR A 2 1/2". EL ESPESOR DE LA CAPA DE BASE ES DECOR NO MAYOR A 0.10 M.

ESPECIFICACIONES PAVIMENTO

REQUISITOS PARA LOS MATERIALES.
Los materiales para pavimentos de concreto de cemento hidráulico, deben llenar los requisitos siguientes.
(a) **Cemento Hidráulico.** Estos cementos deben cumplir con una clase de resistencia de 20MPa (4,000 PSI) o mayor.
(b) **Agregado fino.** debe consistir en arena natural o manufacturada, compuesta de partículas duras y durables, el agregado fino debe ser almacenado separadamente del agregado grueso, en pilas independientes para las diversas procedencias, debiéndose controlar sus características y los ajustes en la dosificación, en el momento de la elaboración del concreto.
(c) **Agregado Grueso.** Debe consistir en grava o piedra triturada, triturada parcialmente o sin triturar, procesadas adecuadamente para formar un agregado clasificado.
Las juntas de contracción, deberán ser construidas con espaciamientos de 2.50 x2.50 metros, formando una cuadrícula, a 1/3 del espesor del pavimento (0.05 mts.)

ESPECIFICACIONES TÉCNICAS DE DISEÑO

PERIODO DE DISEÑO DE 20 AÑOS.
SUPERFICIE DE RODADURA VARIABLE.
ESPESOR PAVIMENTO 0.15mts.
BOMBEO 3%.

ESPESOR CAPA BASE GRANULAR 0.20 mts.
COMPACTACION AL 95% (AASHTO T 180).

FUENTE: Especificaciones del libro Azul y Características Geométricas de carretera de la D.G.C. de Guatemala.

TOTAL VOLUMEN DE CORTE = 112.20m³
TOTAL VOLUMEN DE TERRAPLEN = 430.04m³



ADMINISTRACION
2024 - 2028

MUNICIPALIDAD DE
COBAN, A.V.
Dirección de Perfilación y
Elaboración de proyectos

PROYECTO:
MEJORAMIENTO CAMINO RURAL
(PAVIMENTO RIGIDO) CASERIO GUALOM
SAXYANQTZUUL, COBAN, ALTA VERAPAZ

No. SNIP:
353086

UBICACIÓN:
CASERIO GUALOM SAXYANQTUUL
COBAN ALTA VERAPAZ

CONTIENE:
PLANO DE CURVAS DE NIVEL

DISEÑO:
DIRECCIÓN DE PERFILACION Y
ELABORACIÓN DE PROYECTOS

DIBUJO:
DIRECCIÓN DE PERFILACION Y
ELABORACIÓN DE PROYECTOS

CALCULO:
DIRECCIÓN DE PERFILACION Y
ELABORACIÓN DE PROYECTOS

Vo. Bo.:



Alexis Abraham Pérez Morales
INGENIERO CIVIL
COLEGIADO No. 18,977

ARQ. E. INS.
MAGNITUD:
610 M.
FECHA:
AGOSTO - 2025
ESCALA:
INDICADA

HOJA A-1
03/10

INDICA BORDILLO

INDICA BORDILLO

INDICA LINEA BLANCA CONTINUA

INDICA LINEA AMARILLA CONTINUA



INDICA LINEA BLANCA CONTINUA

INDICA BORDILLO

INDICA BORDILLO

ELEMENTOS REPRESENTADOS EN PLANTA

ESCALA 1:150

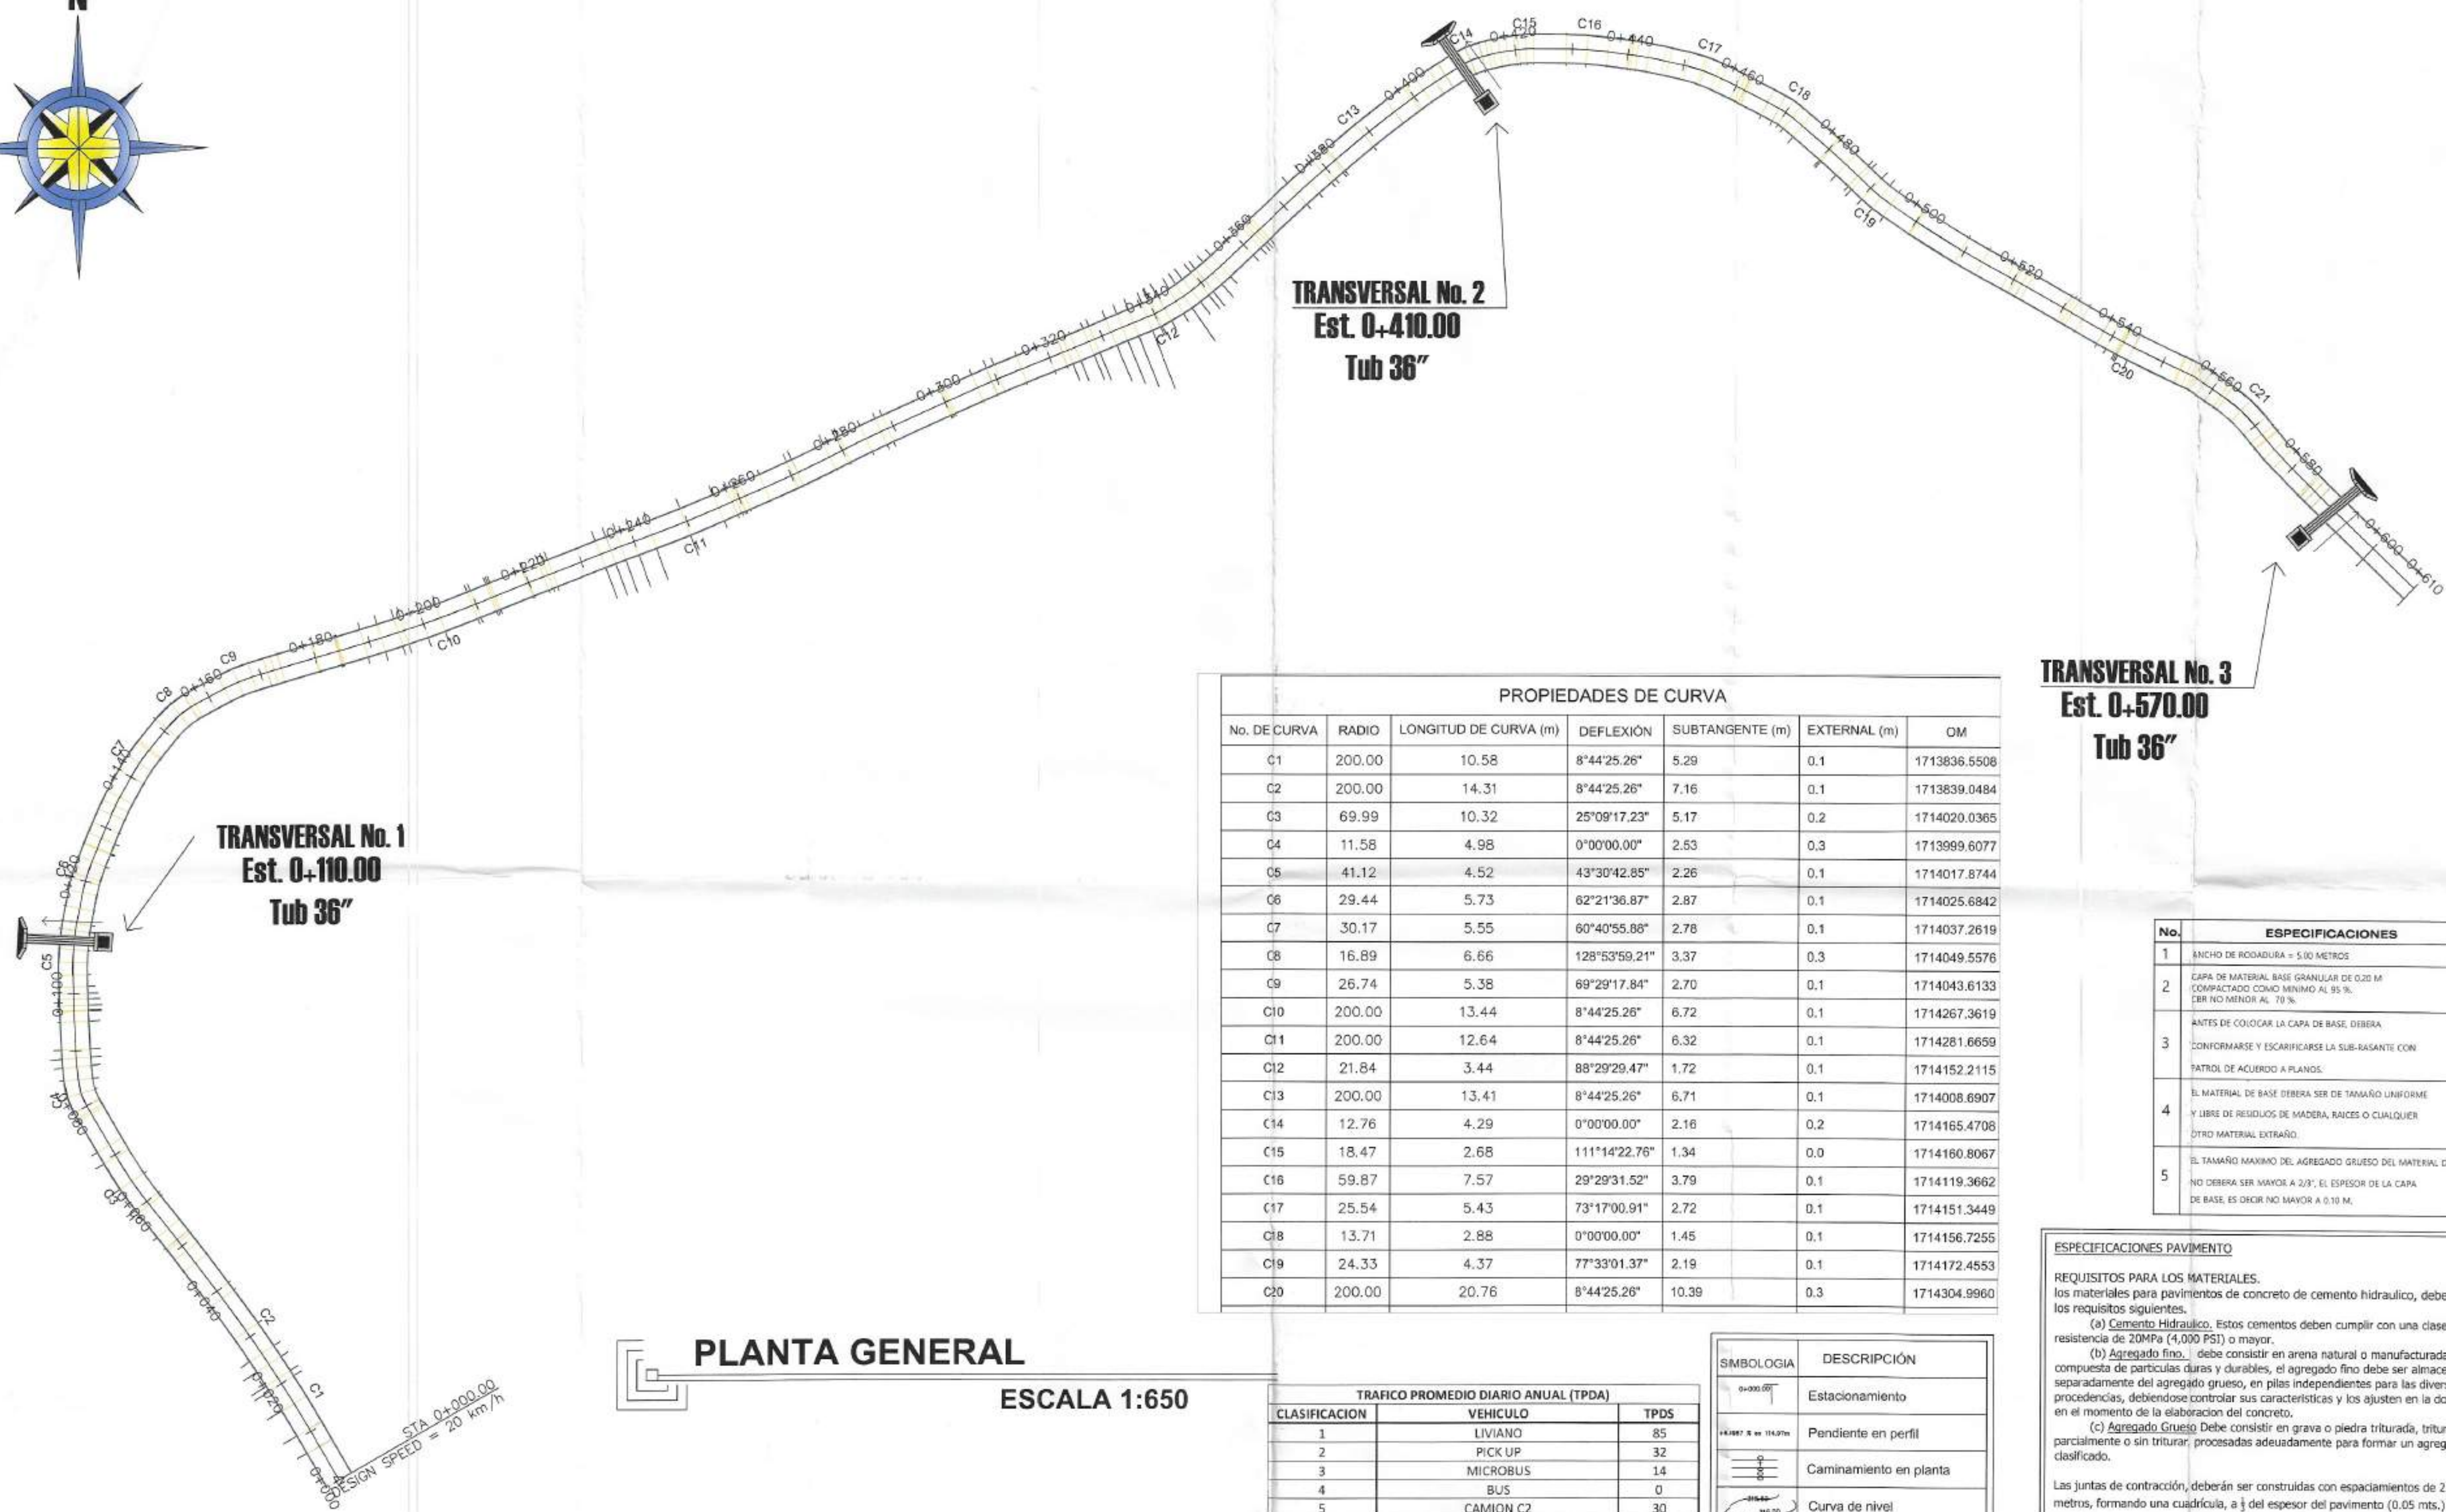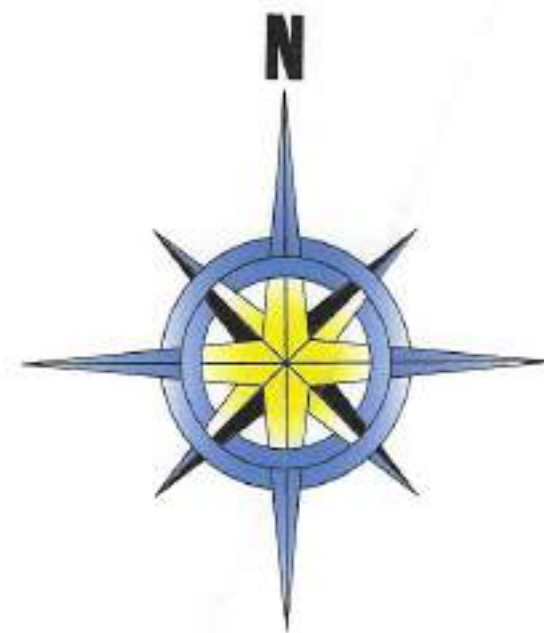


PLANTA GENERAL

ESCALA 1:650

TRAFICO PROMEDIO DIARIO ANUAL (TPDA)		
CLASIFICACION	VEHICULO	TPDS
1	LIVIANO	85
2	PICK UP	32
3	MICROBUS	14
4	BUS	0
5	CAMION C2	30
6	CAMION C3	0
7	CAMION C4	0
8	ARTICULADO T3-S1	0
9	ARTICULADO T3-S2	0
10	ARTICULADO T3-S3	0
TOTAL		

Simbología	Descripción
	Estacionamiento
	Pendiente en perfil
	Caminamiento en planta
	Curva de nivel
	Cota del terreno
	Curva Horizontal
	Curva Vertical
	PRINCIPIO DE CURVA HORIZONTAL
	PRINCIPIO DE TANGENTE HORIZONTAL
	tubería en planta, Caja cabezal en entrada y muro cabezal en salida
	Indica Bordo

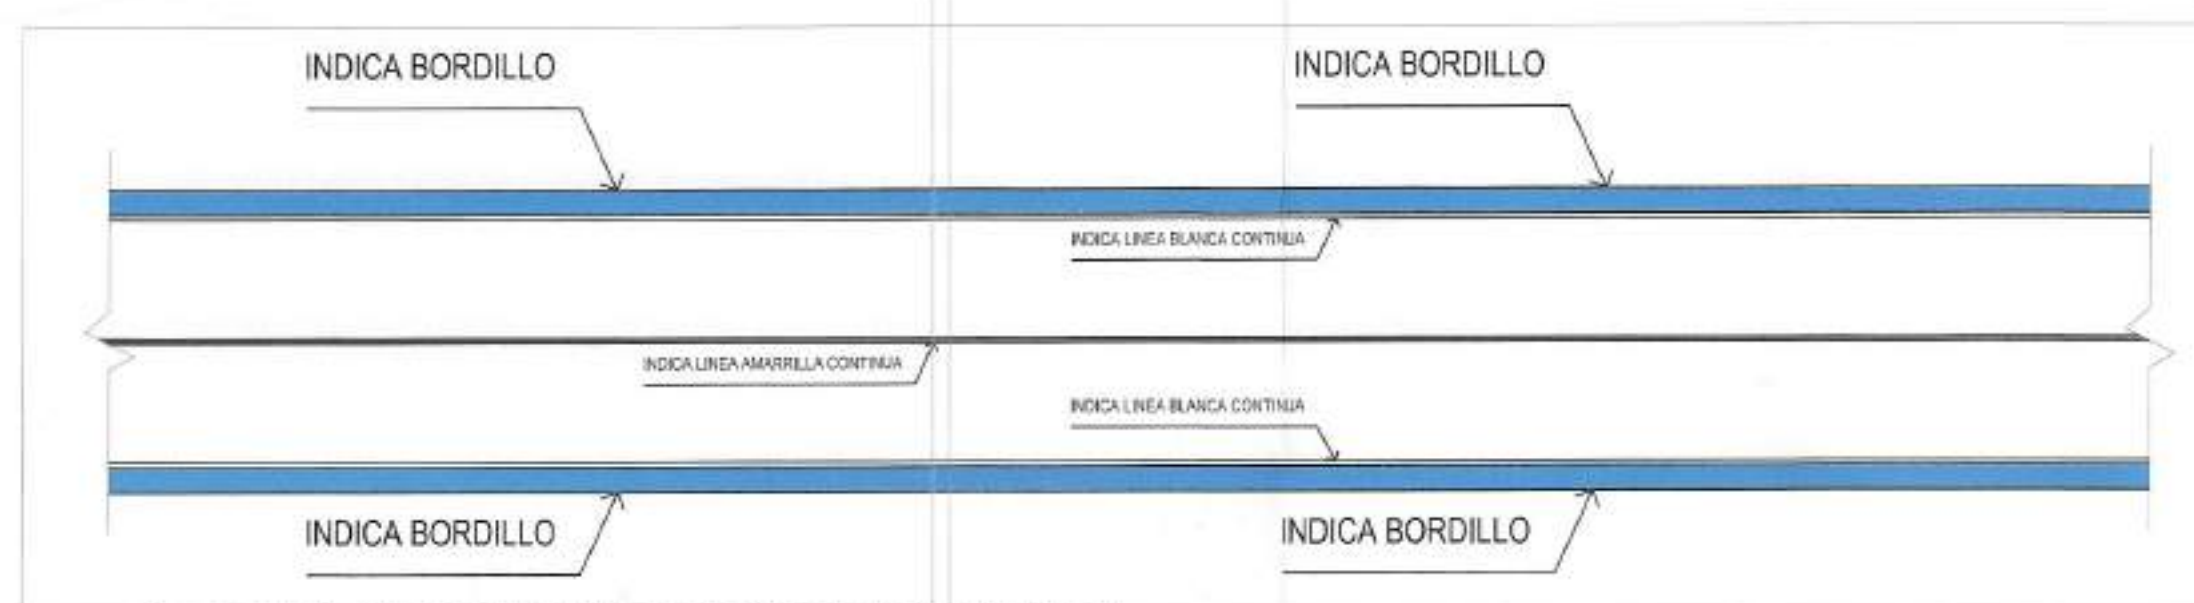

ELEMENTOS REPRESENTADOS EN PLANTA

ESCALA 1:150



ADMINISTRACION
2024 - 2028

MUNICIPALIDAD DE
COBAN, A.V.
Dirección de Perfilación y
Elaboración de proyectos

PROYECTO:
MEJORAMIENTO CAMINO RURAL
(PAVIMENTO RIGIDO) CASERIO GUALOM
SAXYANQTZUUL, COBAN, ALTA VERAPAZ

No. SNIP:

353086

UBICACIÓN:
CASERIO GUALOM SAXYANQTUUL
COBAN ALTA VERAPAZ

CONTIENE:
**PLANO DE PLANTA
GENERAL**

DISEÑO:
DIRECCIÓN DE PERFILACION Y
ELABORACIÓN DE PROYECTOS

DIBUJO:
DIRECCIÓN DE PERFILACION Y
ELABORACIÓN DE PROYECTOS

CALCULO:
DIRECCIÓN DE PERFILACION Y
ELABORACIÓN DE PROYECTOS

Vo. Bo.:



TRANSVERSAL No. 3
Est. 0+570.00
Tub 36"


No.	ESPECIFICACIONES
1	ANCHO DE RODADURA = 5.00 METROS
2	CAPA DE MATERIAL BASE GRANULAR DE 0.20 M. COMPACTADO COMO MÍNIMO AL 95 %. ERR NO MENOR AL 70 %
3	ANTES DE COLOCAR LA CAPA DE BASE, DEBERÁ CONFORMARSE Y ESCARIFICARSE LA SUB-RASANTE CON PATROL DE ACUERDO A PLANOS.
4	EL MATERIAL DE BASE DEBERÁ SER DE TAMAÑO UNIFORME Y LIBRE DE RESIDUOS DE MADERA, RAICES O CUALQUIER OTRO MATERIAL EXTRAÑO.
5	EL TAMAÑO MÁXIMO DEL AGREGADO GRUESO DEL MATERIAL DE BASE NO DEBERÁ SER MAYOR A 2/3"; EL ESPESOR DE LA CAPA DE BASE, ES DECIR NO MAYOR A 0.10 M.

ESPECIFICACIONES PAVIMENTO
REQUISITOS PARA LOS MATERIALES.
Los materiales para pavimentos de concreto de cemento hidraulico, deben llenar los requisitos siguientes.
(a) Cemento Hidraulico. Estos cementos deben cumplir con una clase de resistencia de 20MPa (4,000 PSI) o mayor.
(b) Agregado fino. Debe consistir en arena natural o manufacturada, compuesta de partículas duras y durables, el agregado fino debe ser almacenado separadamente del agregado grueso, en pilas independientes para las diversas procedencias, debiéndose controlar sus características y los ajustes en la dosificación, en el momento de la elaboración del concreto.
(c) Agregado Grueso. Debe consistir en grava o piedra triturada, triturada parcialmente o sin triturar, procesadas adecuadamente para formar un agregado clasificado.
Las juntas de contracción, deberán ser construidas con espaciamentos de 2.50 x2.50 metros, formando una cuadrícula, a $\frac{1}{2}$ del espesor del pavimento (0.05 mts.)

ESPECIFICACIONES TECNICAS DE DISEÑO
PERIODO DE DISEÑO DE 20 AÑOS.
SUPERFICIE DE RODADURA VARIABLE.
ESPESOR PAVIMENTO 0.15mts.
BOMBEO 3%.
ESPESOR CAPA BASE GRANULAR 0.20 mts.
COMPACTACION AL 95% (AASHTO T 180).
FUENTE: Especificaciones del libro Azul y Características Geometricas de carretera de la D.G.C. de Guatemala.

TOTAL VOLUMEN DE CORTE = 112.20m3
TOTAL VOLUMEN DE TERRAPLEN = 430.04m3

MAGNITUD: 610 M.
FECHA: AGOSTO - 2025
ESCALA: INDICADA
HOJA A-1
04/10

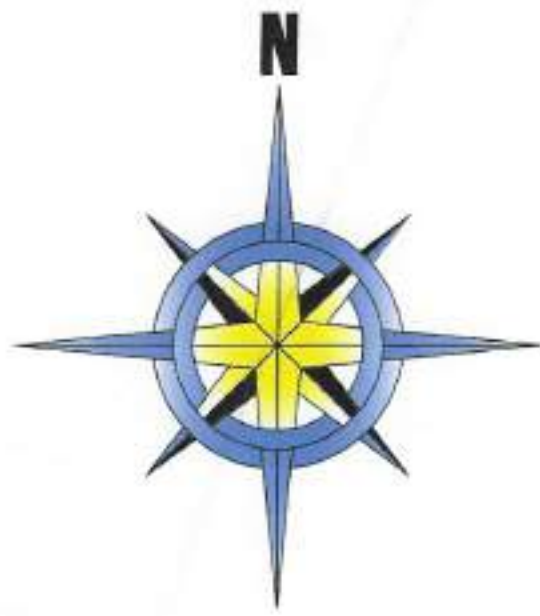

ADMINISTRACION
2024 - 2028

MUNICIPALIDAD DE
COBAN, A.V.
Dirección de Perfilación y
Elaboración de proyectos

PROYECTO:
MEJORAMIENTO CAMINO RURAL
(PAVIMENTO RIGIDO) CASERIO GUALOM
SAXYANQTUUL, COBAN, ALTA VERAPAZ

No. SNIP:
353086

UBICACIÓN:
CASERIO GUALOM SAXYANQTUUL
COBAN ALTA VERAPAZ

CONTIENE:
PLANTA PERFIL
0+000.00 : 0+610.00

DISEÑO:
DIRECCIÓN DE PERFILACION Y
ELABORACIÓN DE PROYECTOS

DIBUJO:
DIRECCIÓN DE PERFILACION Y
ELABORACIÓN DE PROYECTOS

CALCULO:
DIRECCIÓN DE PERFILACION Y
ELABORACIÓN DE PROYECTOS

Va. Bo.:
MUNICIPALIDAD DE COBAN
CIUDAD IMPERIAL


Alexis Abraham Pereira
INGENIERO CIVIL
COLEGIADO No. 18,077

HOJA A-1
FECHA:
AGOSTO - 2025
ESCALA:
INDICADA

PLANTA EST. 0+000 A 0+610
ESCALA 1:700

PERFIL LONGITUDINAL

Indica área de relleno
Indica área de corte

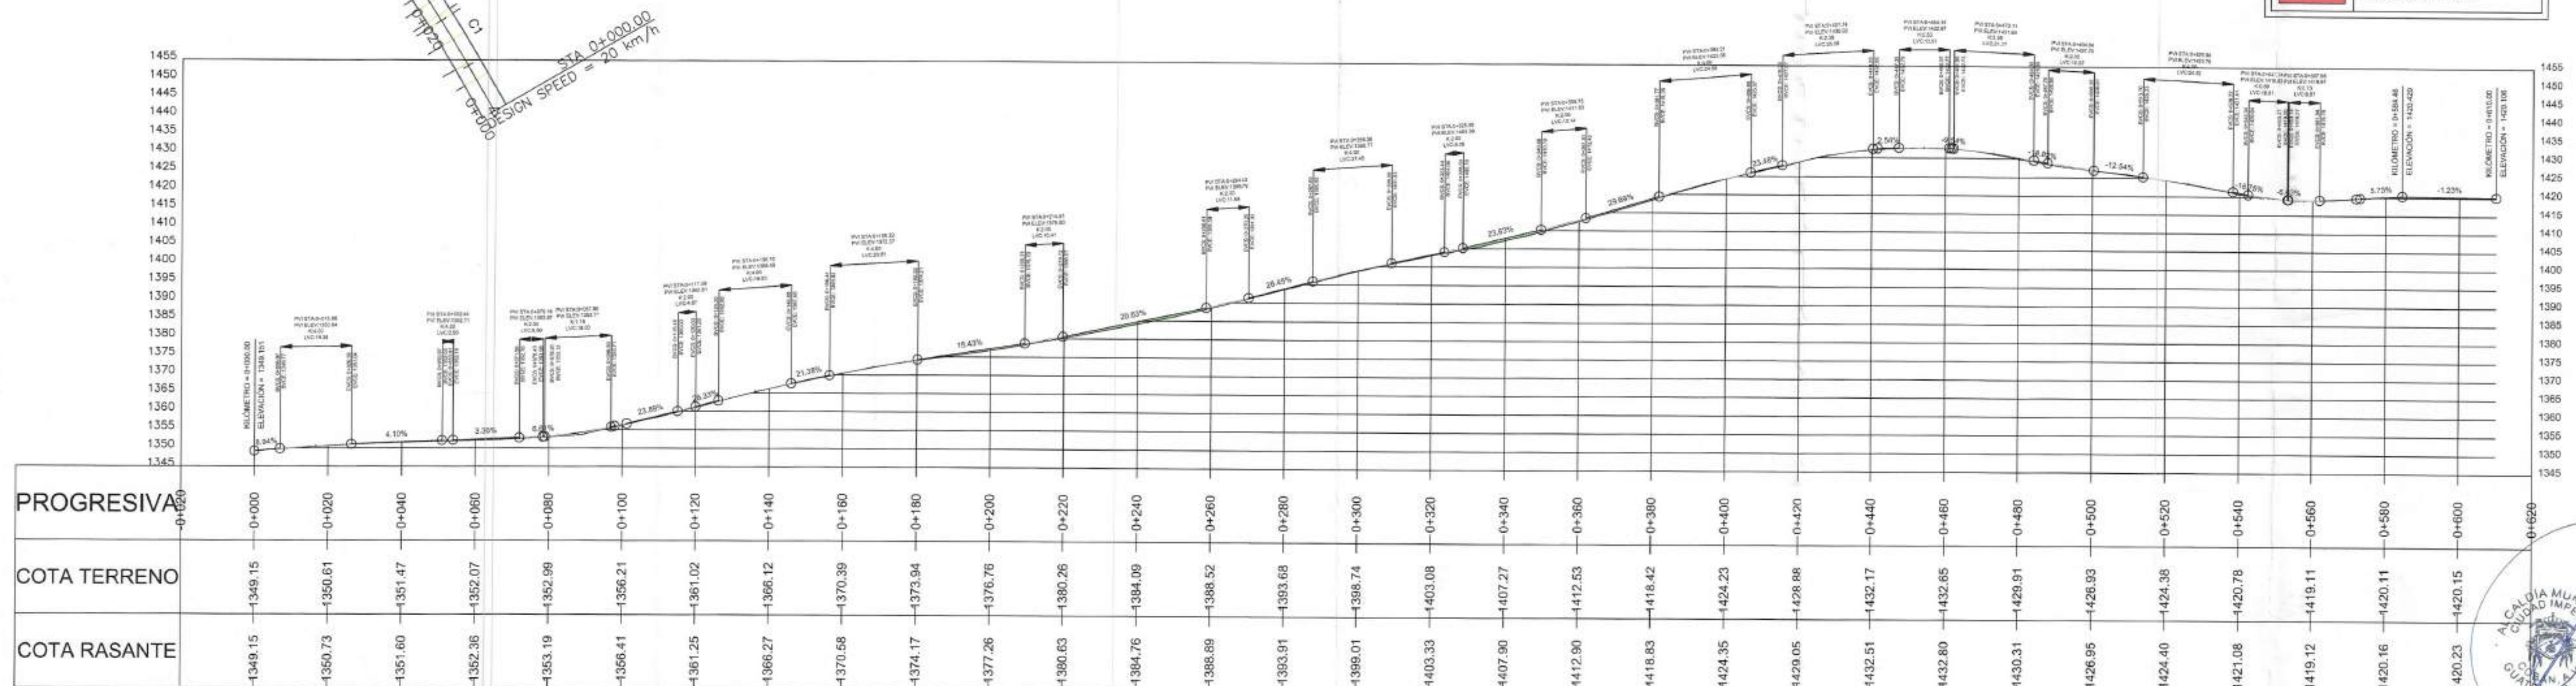

PERFIL EST. 0+000 A 0+610
ESCALA 1:1000