



PLANO DE SEÑALIZACIÓN VERTICAL



ESCALA 1:700

TRANSVERSAL No. 3
Est. 0+570.00
Tub 36"


TRANSVERSAL No. 1
Est. 0+110.00
Tub 36"

TRANSVERSAL No. 2
Est. 0+410.00
Tub 36"


SIMBOLOGIA	
	PENDIENTE PRONUNCIADA
	VELOCIDAD MAXIMA PERMITIDA

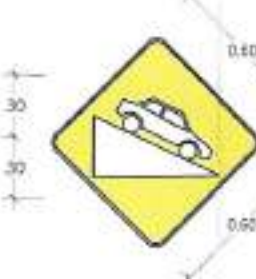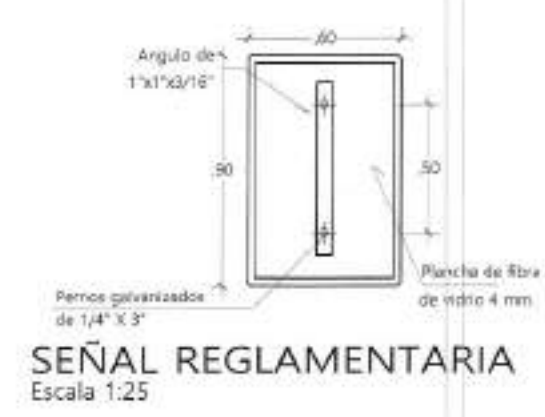

DETALLE DE SEÑALES

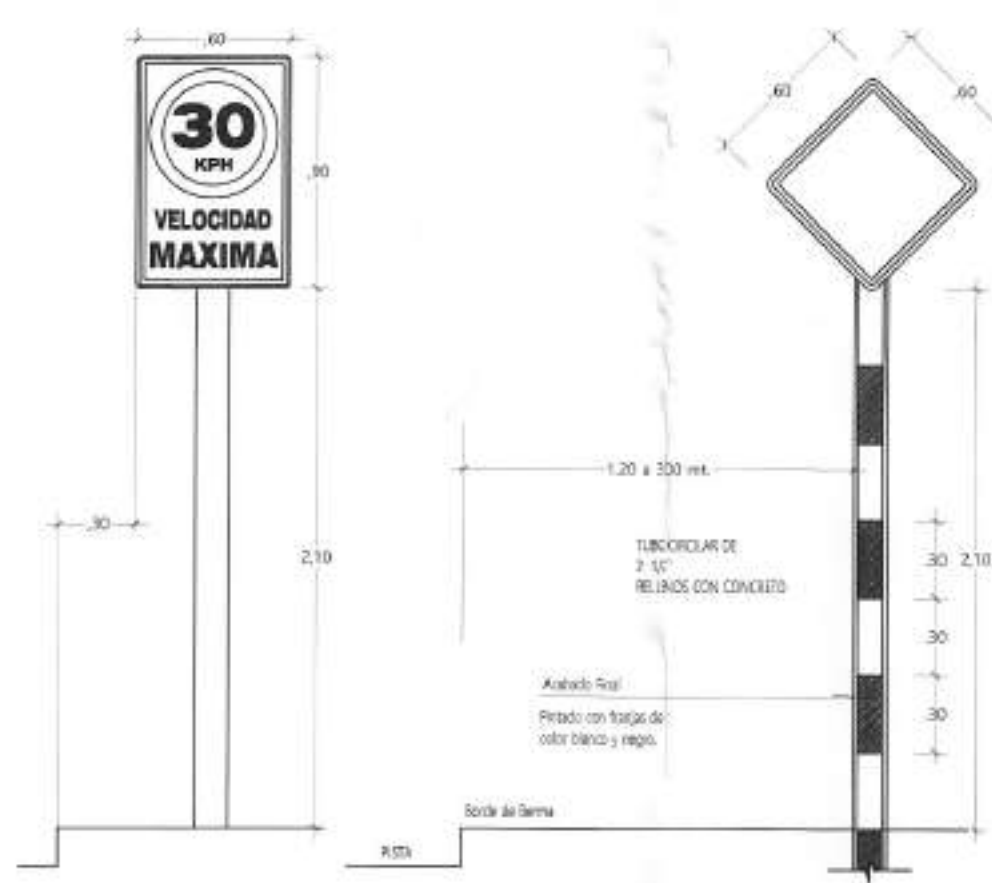

UBICACION DE SEÑALES VERTICALES CON RELACION AL BORDE Y NIVEL DE LA VIA
Escala 1:25

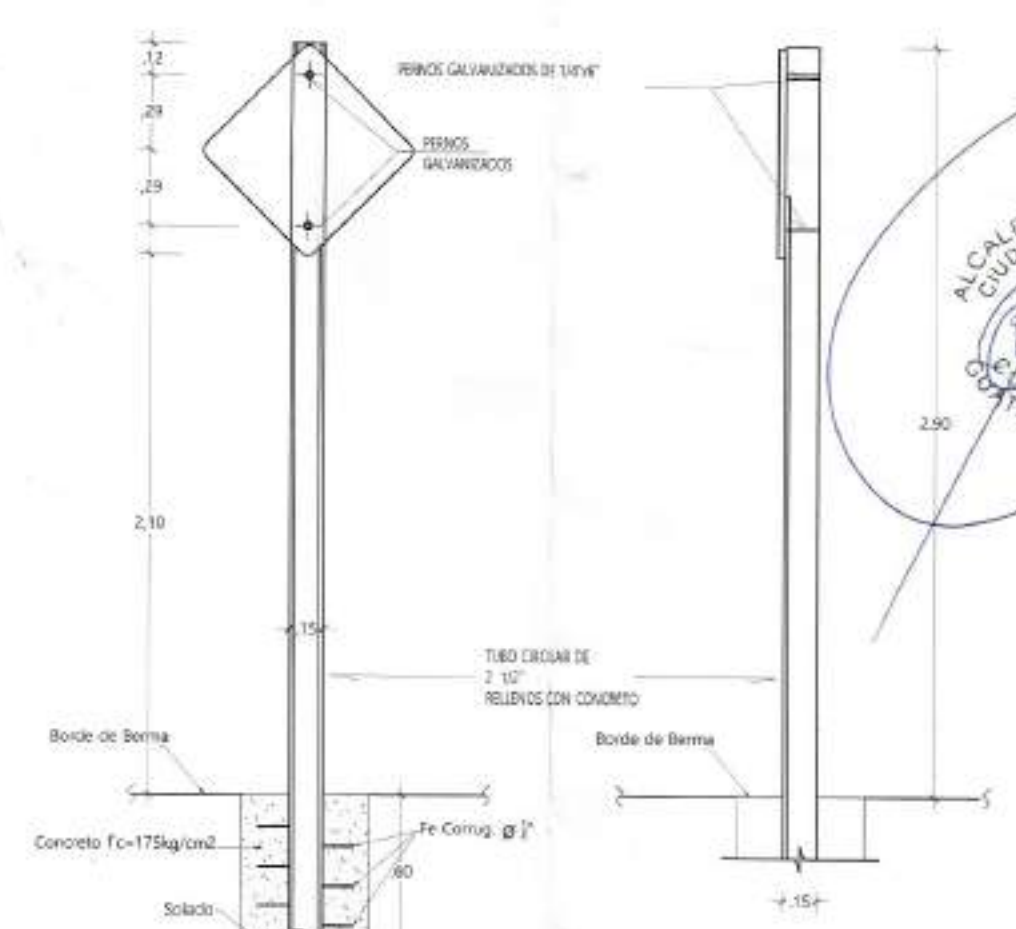

DISENO ESTRUCTURAL DE LOS POSTES PARA SEÑALIZACION PREVENTIVA Y REGLAMENTARIA
Escala 1:25



ADMINISTRACION
2024 - 2028

MUNICIPALIDAD DE
COBAN, A.V.
Dirección de Perfilación y
Elaboración de proyectos

PROYECTO:
MEJORAMIENTO CAMINO RURAL
(PAVIMENTO RIGIDO) CASERIO GUALOM
SAXYANTZUUL, COBAN, ALTA VERAPAZ

No. SNIP:
353086

UBICACIÓN:
CASERIO GUALOM SAXYANTZUUL
COBAN ALTA VERAPAZ

CONTIENE:
**PLANO DE
SEÑALIZACIÓN
VERTICAL**

DISEÑO:
DIRECCIÓN DE PERFILACION Y
ELABORACIÓN DE PROYECTOS

DIBUJO:
DIRECCIÓN DE PERFILACION Y
ELABORACIÓN DE PROYECTOS

CALCULO:
DIRECCIÓN DE PERFILACION Y
ELABORACIÓN DE PROYECTOS

Vo. Bo.:

TABLA DE VOLÚMENES DE CORTE Y RELLENO						
ESTACIÓN	ÁREA DE RELLENO	ÁREA DE CORTE	VOLUMEN DE RELLENO	VOLUMEN DE CORTE	VOL. ACUM. DE RELLENO	VOL ACUM. DE CORTE
0+020.00	2.06	0.11	0.00	0.00	0.00	0.00
0+040.00	0.03	0.19	20.62	2.92	20.62	2.92
0+060.00	0.95	0.00	9.78	1.86	30.40	4.78
0+080.00	0.18	0.05	11.48	0.52	41.88	5.30
0+100.00	0.65	0.00	8.11	0.50	50.00	5.80
0+120.00	0.20	0.00	8.34	0.03	58.34	5.83
0+140.00	0.00	0.37	2.02	3.69	60.36	9.51
0+160.00	0.06	0.12	0.60	4.72	60.96	14.23
0+180.00	0.17	0.00	2.26	1.14	63.22	15.37
0+200.00	1.92	0.00	20.88	0.00	84.10	15.37
0+220.00	1.37	0.00	32.91	0.00	117.01	15.37
0+240.00	4.14	0.00	55.09	0.00	172.10	15.37
0+260.00	0.85	0.00	50.03	0.00	222.13	15.37
0+280.00	0.84	0.00	16.92	0.00	239.05	15.37
0+300.00	0.58	0.00	14.30	0.00	253.35	15.37
0+320.00	0.28	0.00	8.64	0.03	261.99	15.40
0+340.00	3.17	0.00	34.50	0.03	296.49	15.42
0+360.00	1.17	0.00	43.27	0.00	339.76	15.42
0+380.00	1.36	0.00	25.32	0.00	365.08	15.42
0+400.00	0.00	0.51	13.63	5.09	378.71	20.51

TABLA DE VOLÚMENES DE CORTE Y RELLENO						
ESTACIÓN	ÁREA DE RELLENO	ÁREA DE CORTE	VOLUMEN DE RELLENO	VOLUMEN DE CORTE	VOL. ACUM. DE RELLENO	VOL ACUM. DE CORTE
0+420.00	0.00	0.34	0.03	8.31	378.74	28.82
0+440.00	0.53	0.00	5.42	3.29	384.15	32.11
0+460.00	0.00	0.29	5.40	2.94	389.55	35.05
0+480.00	1.45	0.00	14.26	2.94	403.81	37.99
0+500.00	0.00	0.55	14.68	5.47	418.49	43.46
0+520.00	0.00	1.13	0.00	16.72	418.49	60.18
0+540.00	0.58	0.00	5.78	11.27	424.27	71.45
0+560.00	0.00	0.99	5.77	9.94	430.04	81.39
0+580.00	0.00	0.71	0.00	17.09	430.04	98.48
0+600.00	0.00	0.66	0.00	13.72	430.04	112.20

430.04112.20

TABLA DE VOLÚMENES

SIN ESCALA



ADMINISTRACION
2024 - 2028

MUNICIPALIDAD DE
COBAN, A.V.
Dirección de Perfilación y
Elaboración de proyectos

PROYECTO:
MEJORAMIENTO CAMINO RURAL
(PAVIMENTO RIGIDO) CASERIO GUALOM
SAXYANQTZUUL, COBAN, ALTA VERAPAZ

No. SNIP:
353086

UBICACIÓN:
CASERIO GUALOM SAXYANQTUUL
COBAN ALTA VERAPAZ


CONTIENE:
CUADRO DE
VOLÚMENES

DISEÑO:
DIRECCIÓN DE PERFILACION Y
ELABORACIÓN DE PROYECTOS





DIBUJO:
DIRECCIÓN DE PERFILACION Y
ELABORACIÓN DE PROYECTOS

CALCULO:
DIRECCIÓN DE PERFILACION Y
ELABORACIÓN DE PROYECTOS

Vo. Bo. :

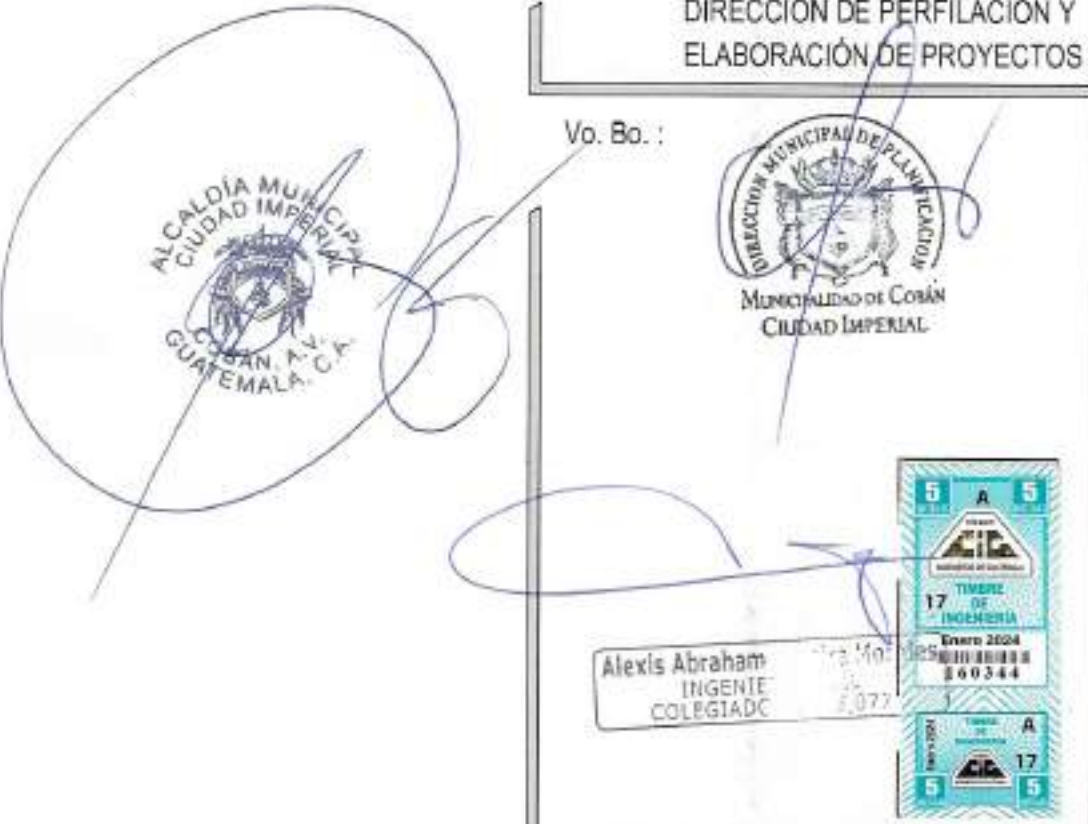

ESCALA 1/7.5

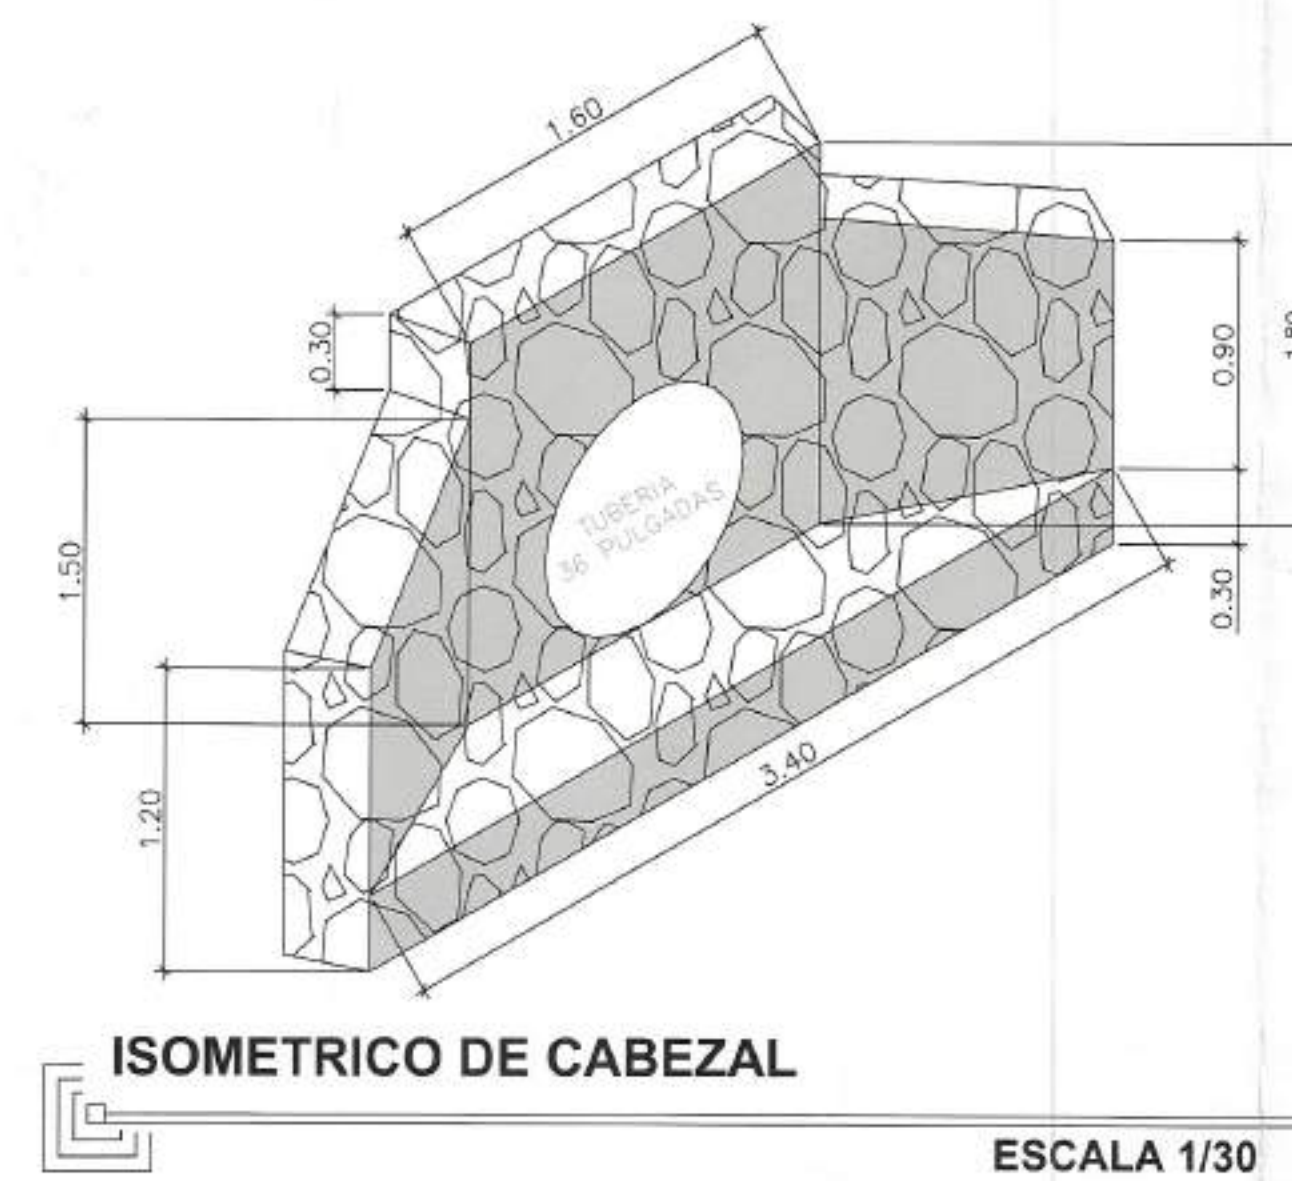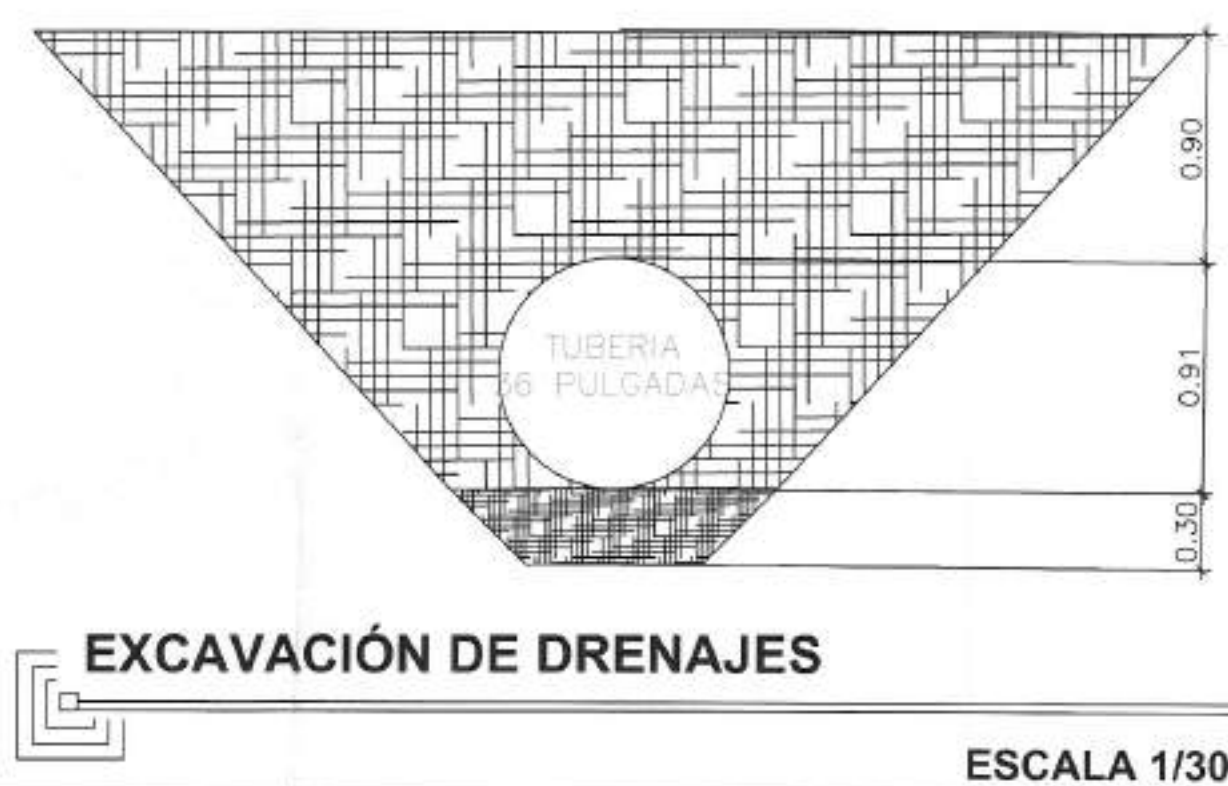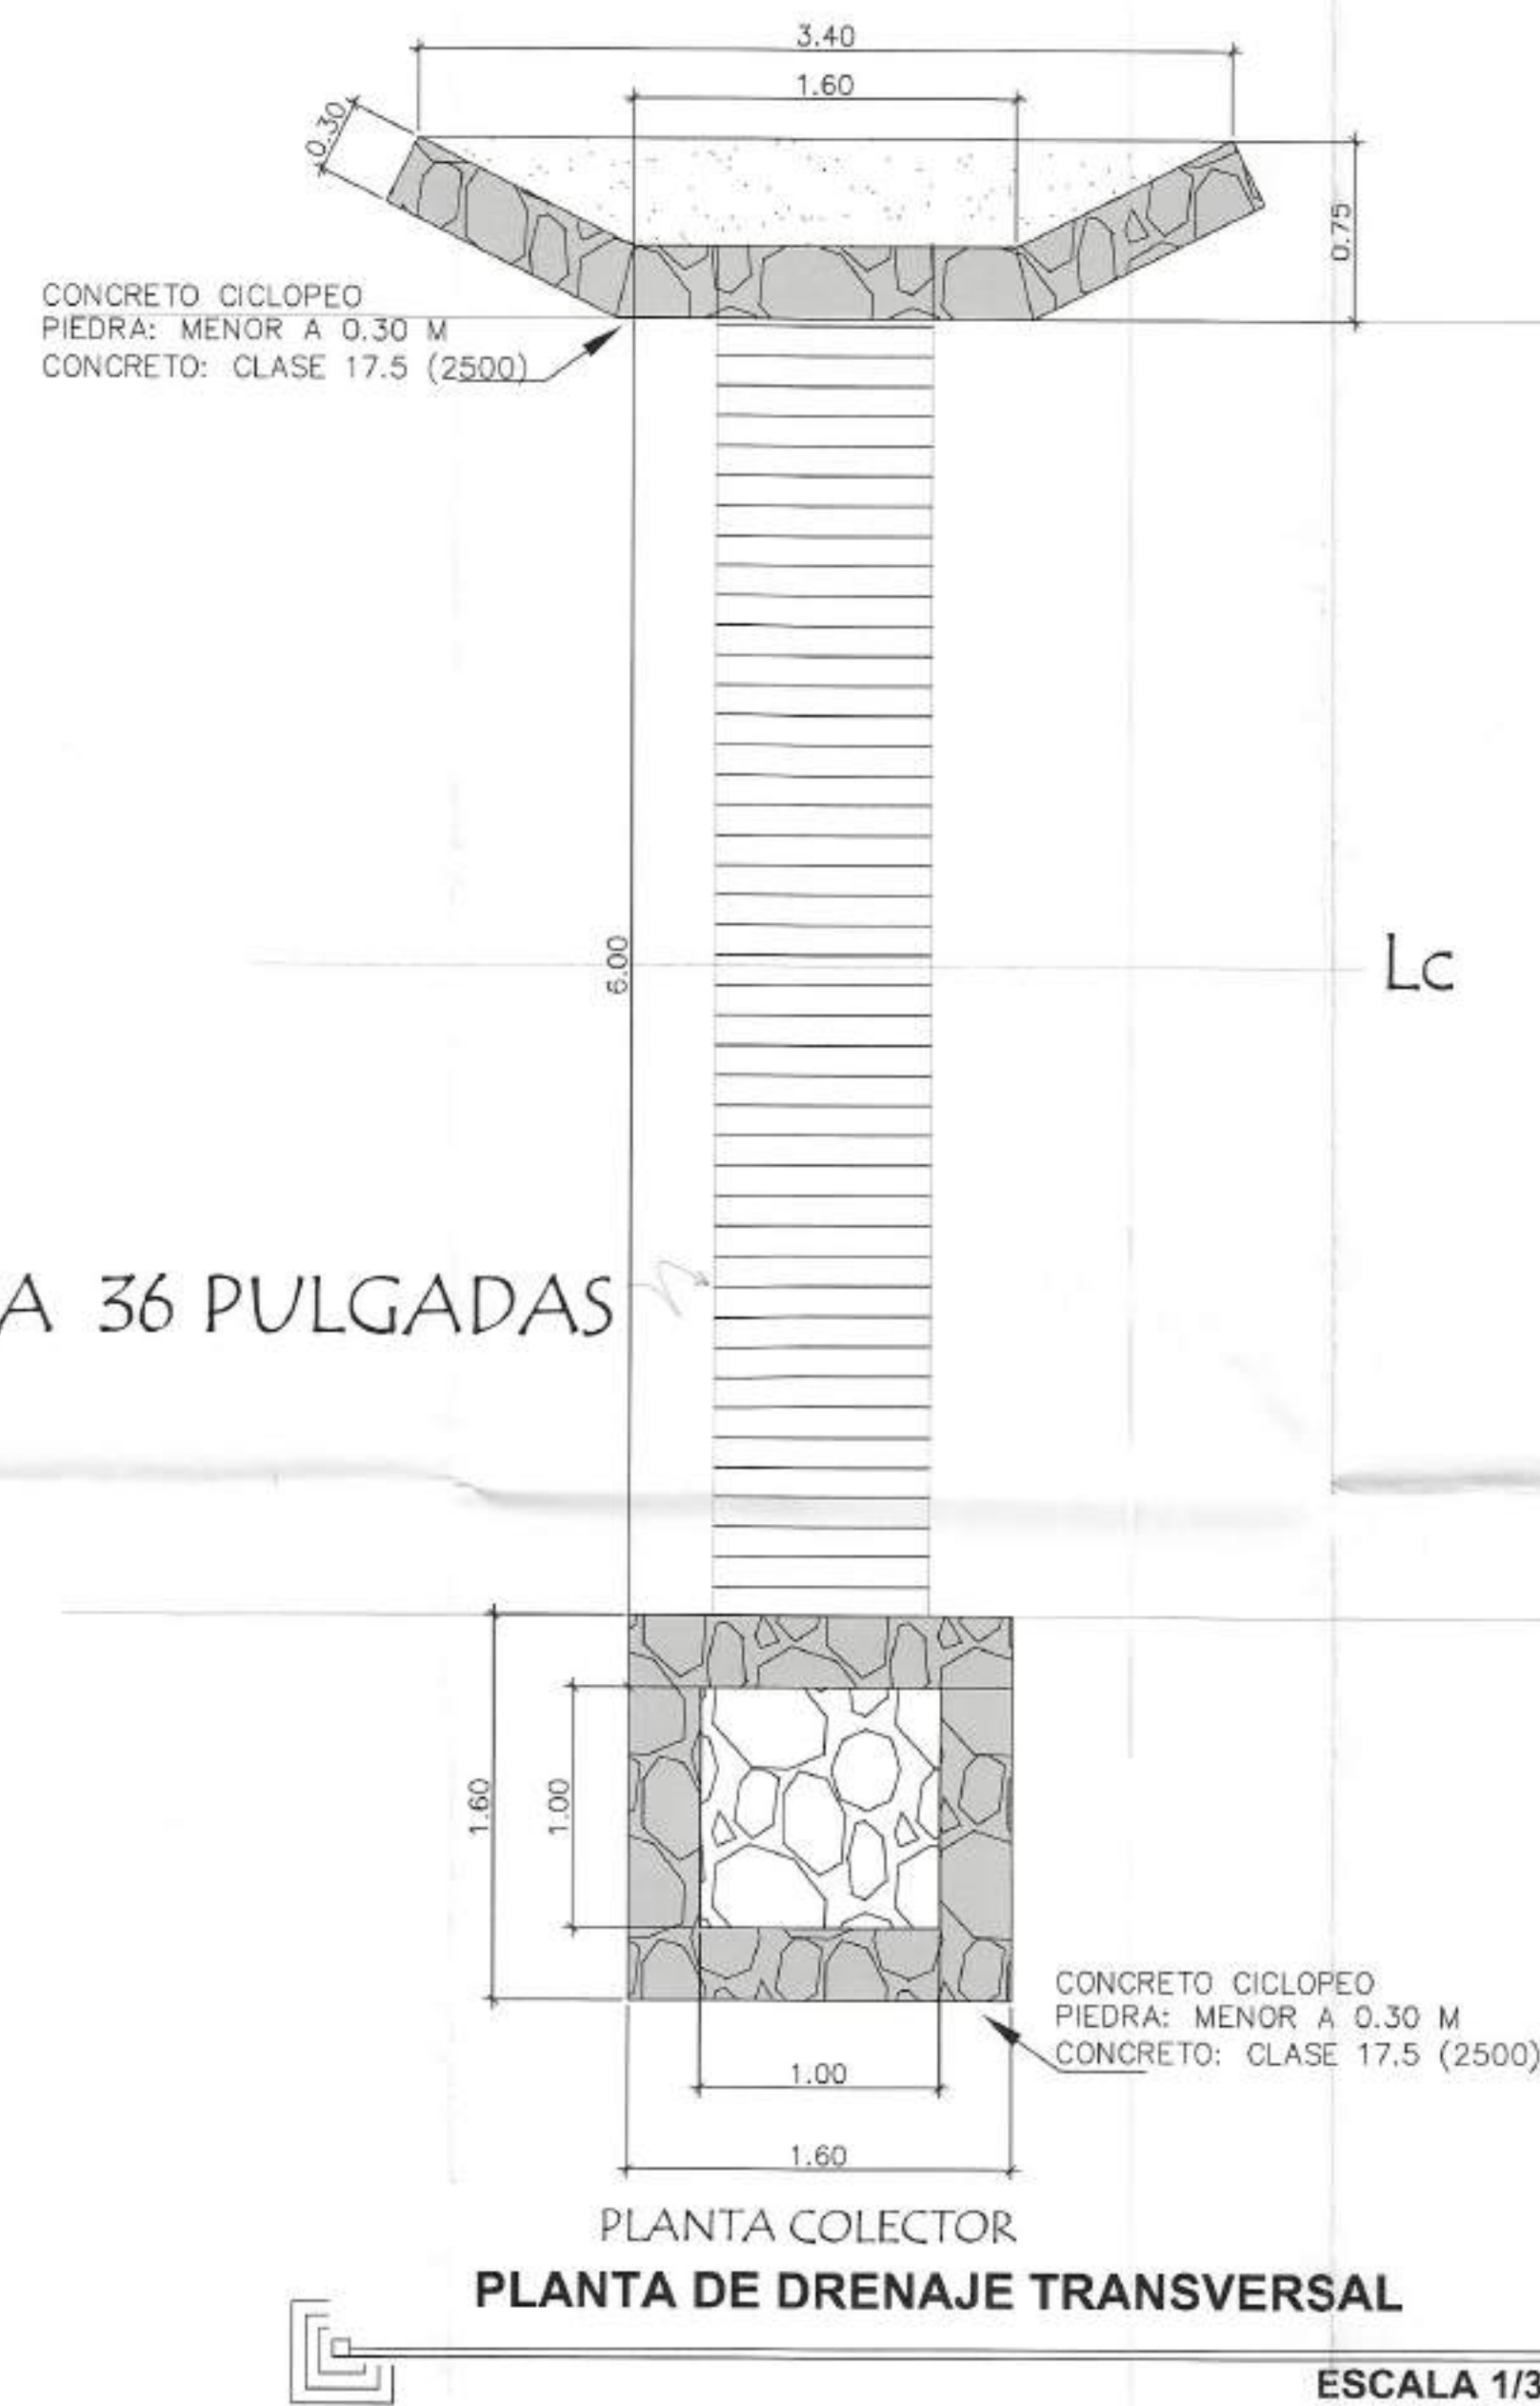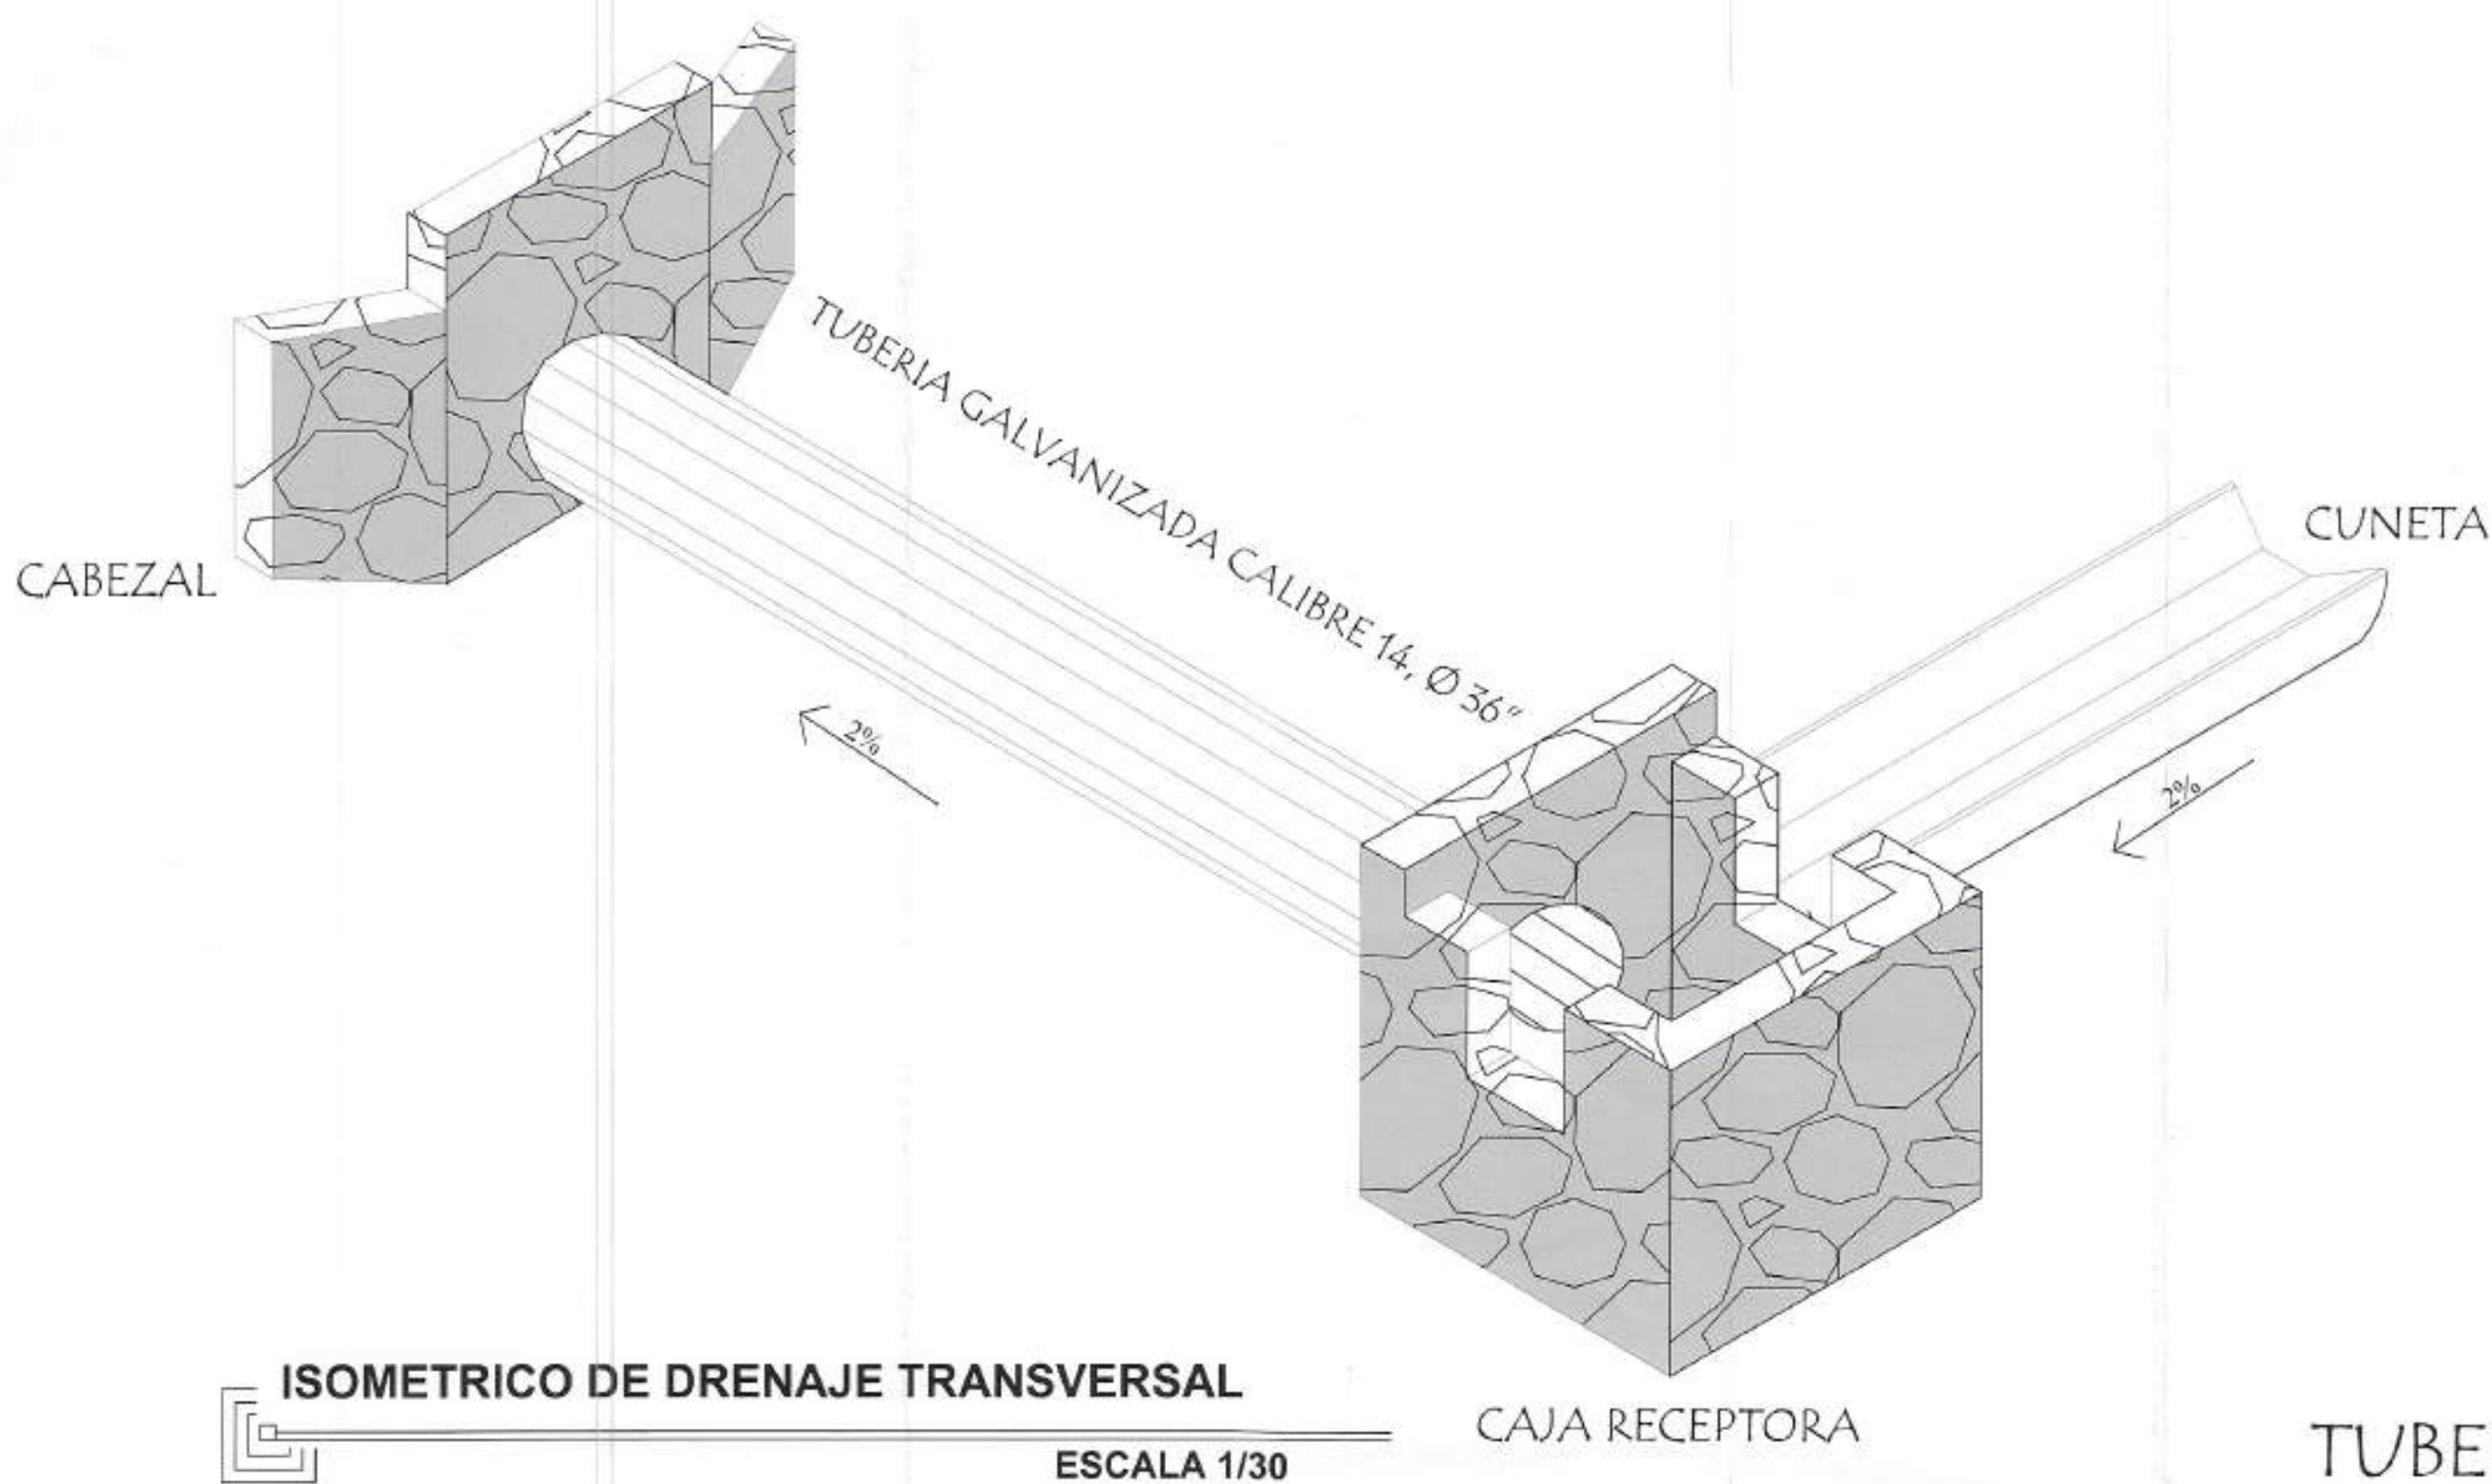

ADMINISTRACION
2024 - 2028

MUNICIPALIDAD DE
COBAN, A.V.
Dirección de Perfilación y
Elaboración de proyectos

PROYECTO:
MEJORAMIENTO CAMINO RURAL
(PAVIMENTO RIGIDO) CASERIO GUALOM
SAXYANQTZUUL, COBAN, ALTA VERAPAZ

No. SNIP:
353086

UBICACIÓN:
CASERIO GUALOM-SAXYANQTUUL
COBAN ALTA VERAPAZ

CONTIENE:
**DETALLE DE
DRENAJES
TRANSVERSALES**

DISEÑO:
DIRECCIÓN DE PERFILACION Y
ELABORACIÓN DE PROYECTOS

DIBUJO:
DIRECCIÓN DE PERFILACION Y
ELABORACIÓN DE PROYECTOS

CALCULO:
DIRECCIÓN DE PERFILACION Y
ELABORACIÓN DE PROYECTOS

Vo. Bo.:
ALCALDIA MUNICIPAL
CIUDAD DE COBAN
GUATEMALA, G.



ARQUITECTO
ESTRUTURISTA
INGENIERO
MAGNITUD:
610 M.
FECHA:
AGOSTO - 2025
ESCALA:
INDICADA

HOJA A-1
10/10